


MATZAV ZOR


EXPERIENCE


Alon Marec, Sahim Mohamed


Sommaire

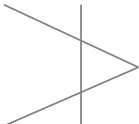

 **L'EXISTANT**

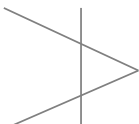 **L'ESQUISSE**

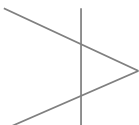 **L'APS**

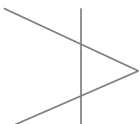 **L'APD**

Note d'intention



Le projet est situé au restaurant Marahja Grill, situé à Nanterre, repose sur un concept sensoriel inspiré du changement d'état de la chaleur. Notre restaurant est basé sur la consommation de viande.

Au début notre projet devait être inspiré du volcan, mais nous n'avons pas trouvé d'inspiration dans cela cependant nous avons retenu la chaleur en élément principal. En étudiant celle-ci nous avons retenu ses différentes phases avec scénographiquement les trois états de la matière solide, liquide et gazeux afin de créer une expérience immersive au sein du restaurant. La **séparation**, la **tension** et le **transfert** sont nos maîtres mots. L'espace est divisé en trois zones distinctes, chacune représentant un état.

l'histoire des restaurants immersives

QUELQUES DATES ...

1987



NAISSANCE DU RESTAURANT À THÈME MODERNE

Ouverture du Rainforest Cafe aux États-Unis : un restaurant où le décor, les sons et l'ambiance recréent une forêt tropicale immersive.

2005



EXPÉRIENCE SENSORIELLE TOTALE

À Berlin ouvre Dans le Noir ?, où les clients mangent dans l'obscurité complète, pour se concentrer sur les sens du goût et de l'odorat.

2015



IMMERSION NUMÉRIQUE ET ARTISTIQUE

Le restaurant Ultraviolet à Shanghai utilise projections, sons, parfums et lumières pour transformer chaque plat en expérience immersive.

2020



IMMERSION TECHNOLOGIQUE

Les restaurants utilisent réalité virtuelle et la scénographie pour créer des expériences culinaires multisensorielles dans plusieurs villes du monde.

Benchmarking

Enigma



Identité Visuelle : Paysage de glace et d'eau. Utilisation massive de résine translucide, de verre martelé et d'inox pour créer un univers monochrome gris-bleuté. **Style** : Futurisme organique . Les parois semblent être en mouvement, évoquant la fluidité et le changement d'état (fusion). **Expérience** : Le client déambule dans un labyrinthe de reflets et de transparences. La matière n'a plus de limites nettes, illustrant parfaitement le concept de "Transfert" thermique.

Alchemist




Identité Visuelle : Scénographie immersive sous un dôme planétaire. Contrastes entre l'obscurité totale et des projections vaporeuses de gaz, d'aurores boréales et de fumée. **Style** : Une cuisine qui met l'accent sur les sensations et les images plutôt que sur le lieu lui-même. C'est une architecture faite d'émotions et de moments éphémères. **Expérience** : Les repères dans l'espace disparaissent. Le repas devient un passage vers quelque chose de plus abstrait. C'est l'expression du "gazeux".

Under



Identité Visuelle : Un grand bloc de béton brut, incliné, qui s'enfonce dans la mer comme une épave ou un rocher. Sa forme est simple et forte, faite de matériaux lourds. **Style** : Un bâtiment de style brutaliste au bord de la mer, conçu par Snøhetta. Il utilise des matériaux très solides pour résister à la force des éléments. **Expérience** : Une sensation de protection et de solidité. La grande fenêtre crée un contraste entre l'intérieur solide et l'extérieur fluide. C'est le point de départ de la matière avant sa transformation.

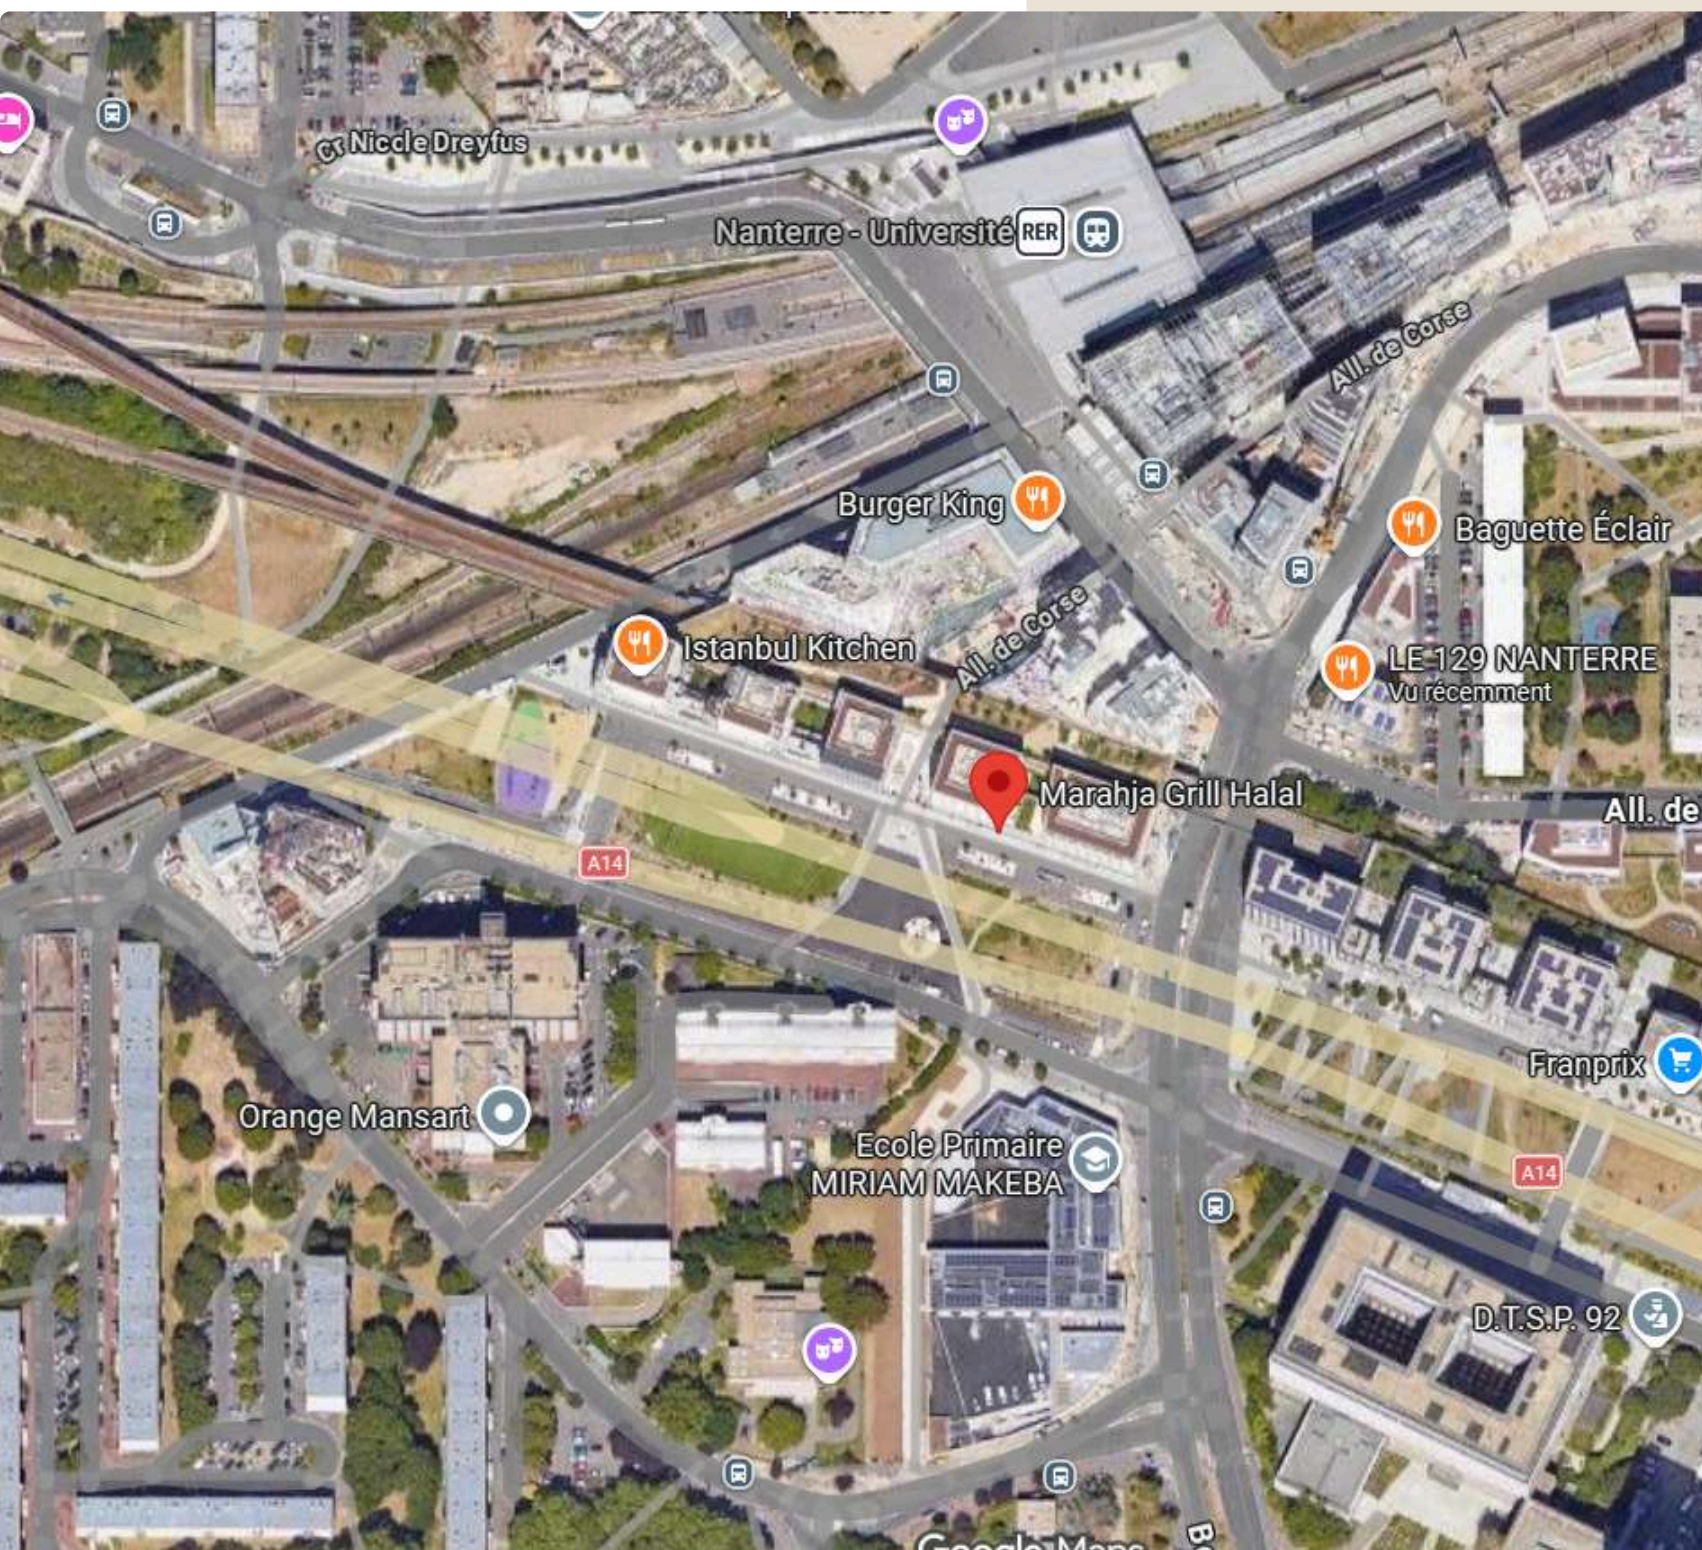

Existant

Plan de situation

25 Terr de l'Université, Nanterre
92000

DIRECTION GÉNÉRALE DES FINANCES
PUBLIQUES ----- EXTRAIT DU
PLAN CADASTRAL -----

Département :
HAUTS DE SEINE

Section : AF Feuille :
000 AF 01

Échelle d'origine : 1/1000
Échelle d'édition : 1/1250

Date d'édition : 06/02/2026
(fuseau horaire de Paris)


Coordonnées en projection : RGF93CC49

Le plan visualisé sur cet extrait est géré par le
centre des impôts foncier suivant : Service
Départemental des Impôts Fonciers PTGC des
Hauts-de-Seine 7 Bd des Bouvets 92741 92741
NANTERRE cedex tél. 01 41 37 83 00 -fax
sdif92.ptgc@dgfip.finances.gouv.fr

Cet extrait de plan vous est délivré par :

cadastre.gouv.fr

©2017 Ministère de l'Action et des Comptes
publics

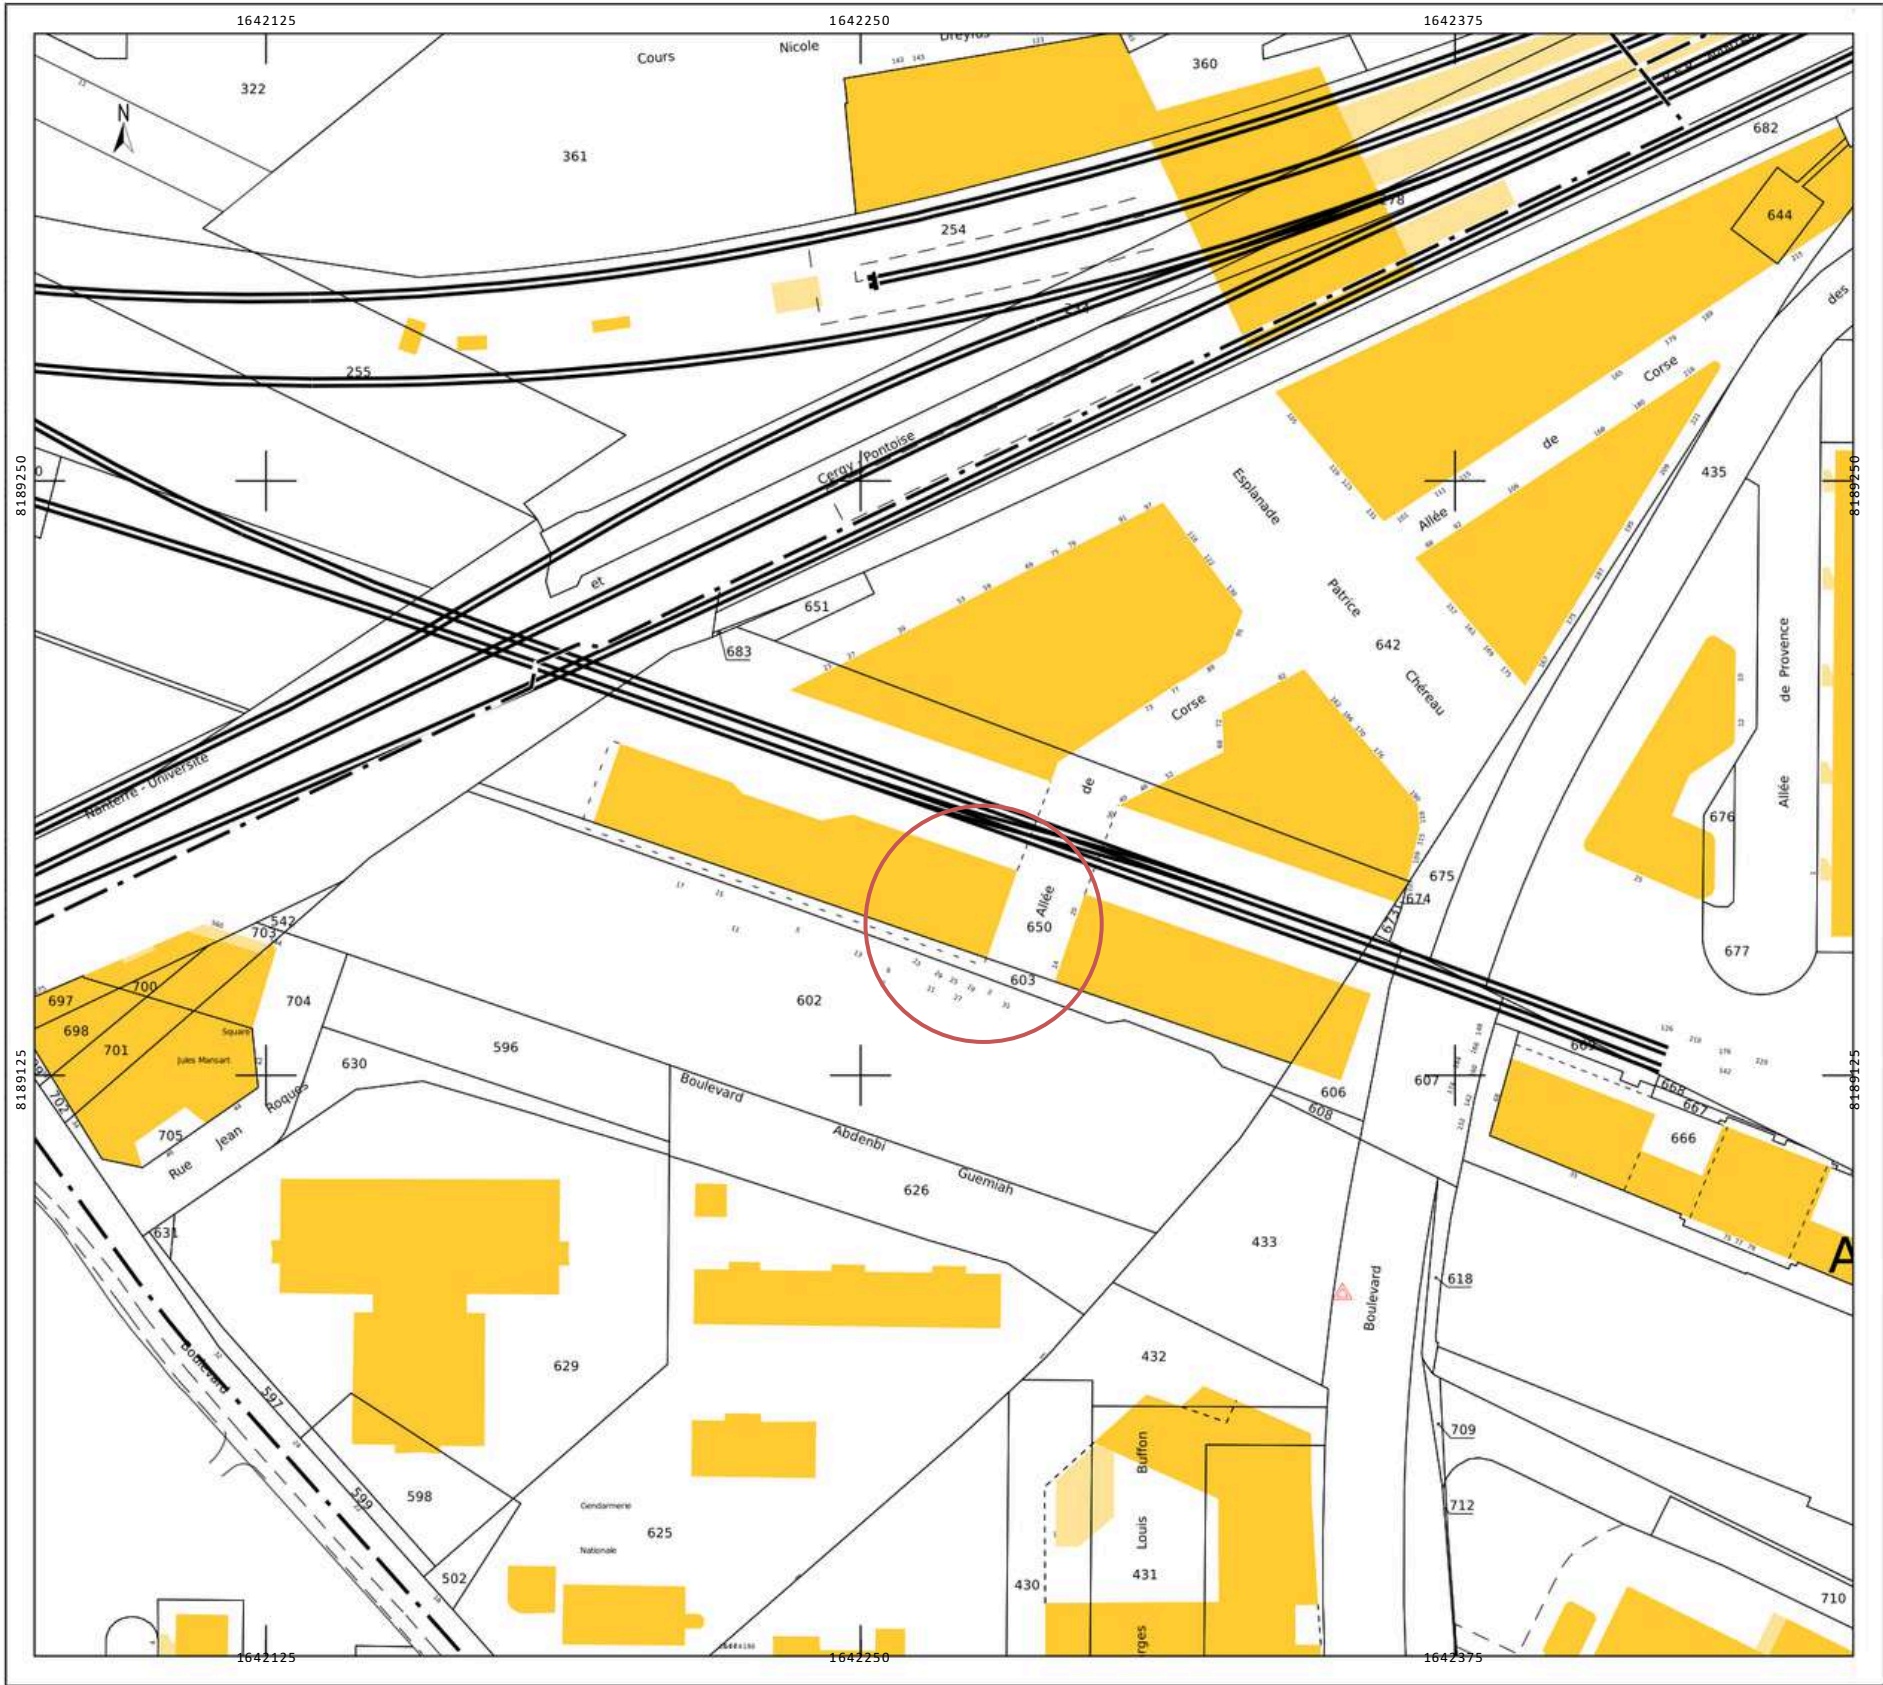


Photos

EXISTANT



Plan EDL





EXISTANT

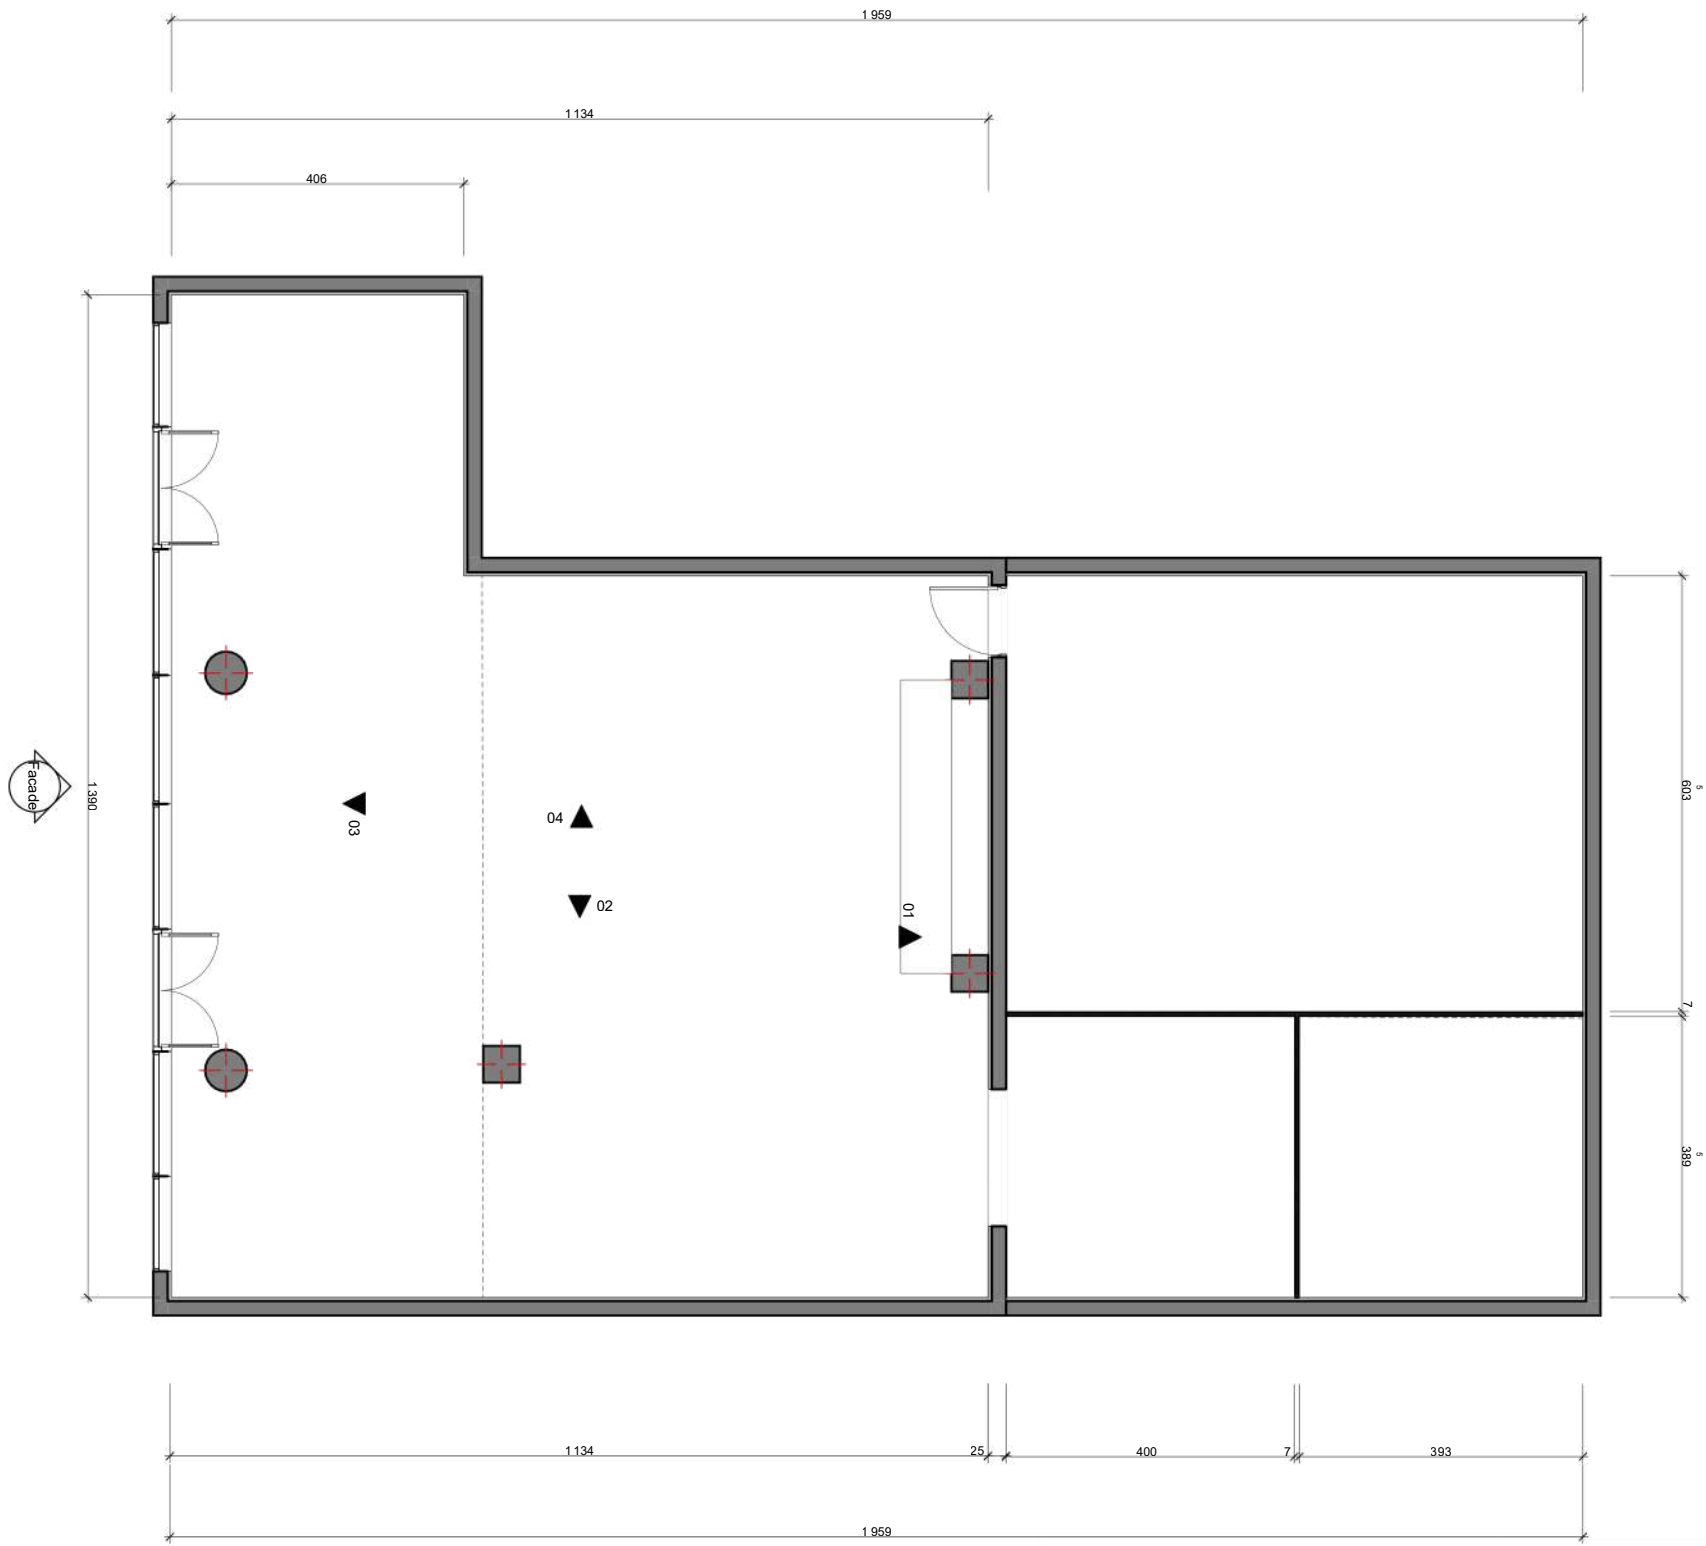

Ouvrage : Restaurant immersif 15 Terr. de l'Université, 92000 Nanterre		Maître d'ouvrage: Léa Froger			Maître d'oeuvre Alon Marec / Mohamed Sahim 12 rue Anatole France , 92000 Nanterre		
N° de plan: 4	Titre: Plan existant	Echelle : 1:50	Format : A3	N° de projet : 1	Destinateur: Alon / Mohamed	Date : 12/03/2026	Etat du projet : Existant

Elevations


EXISTANT

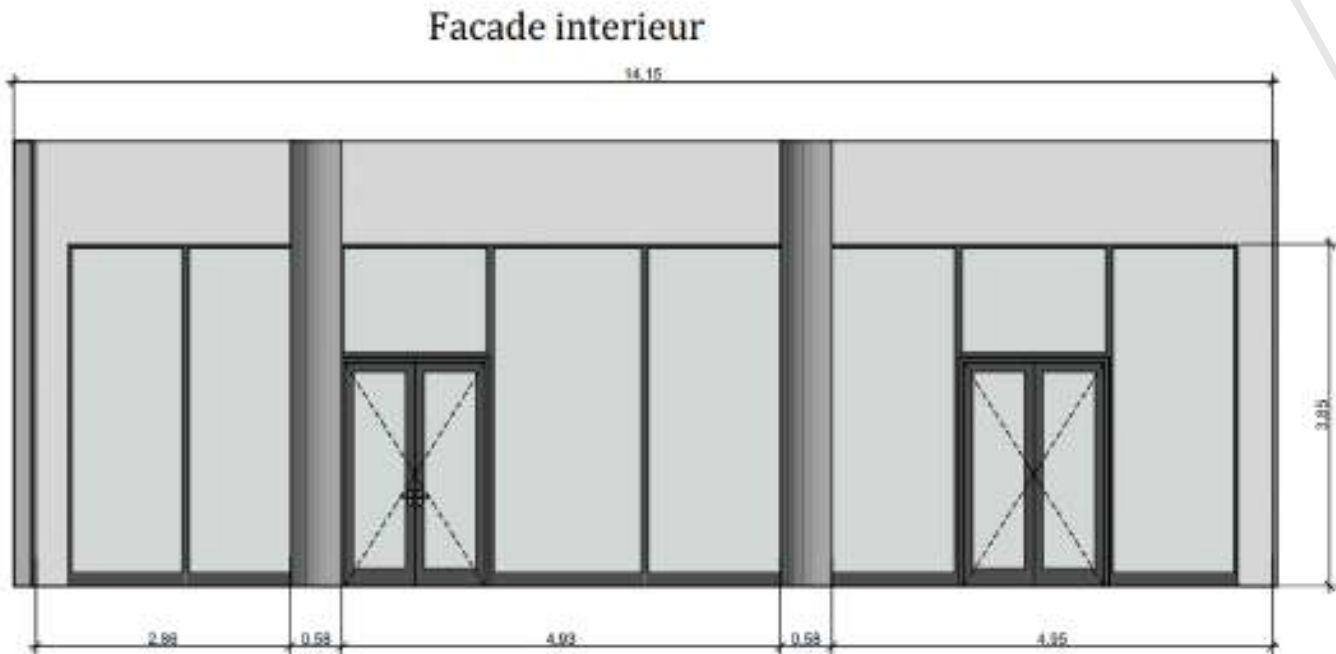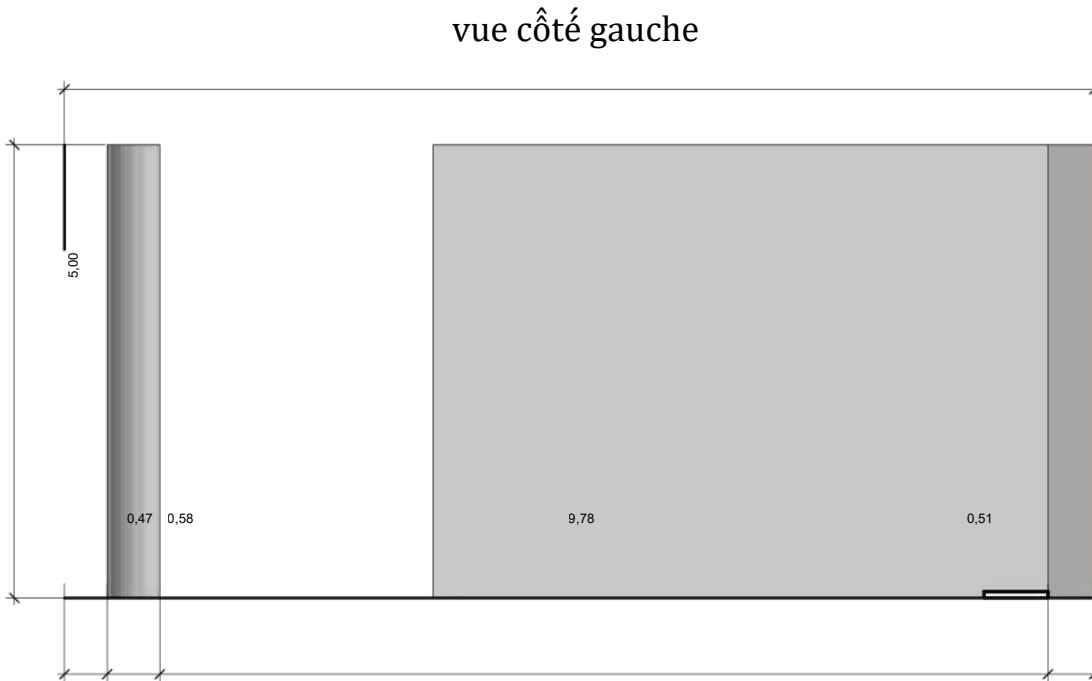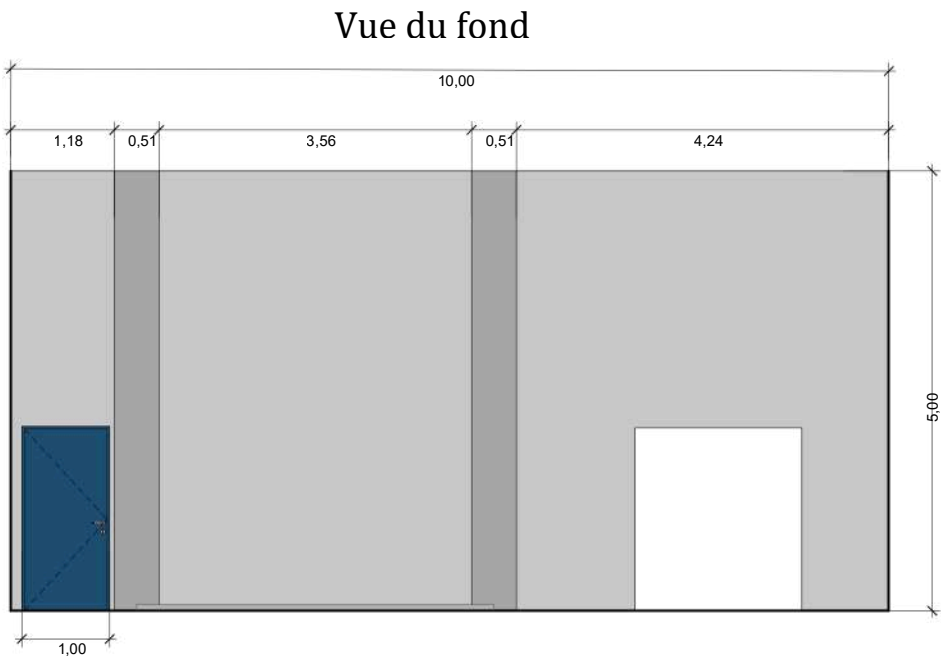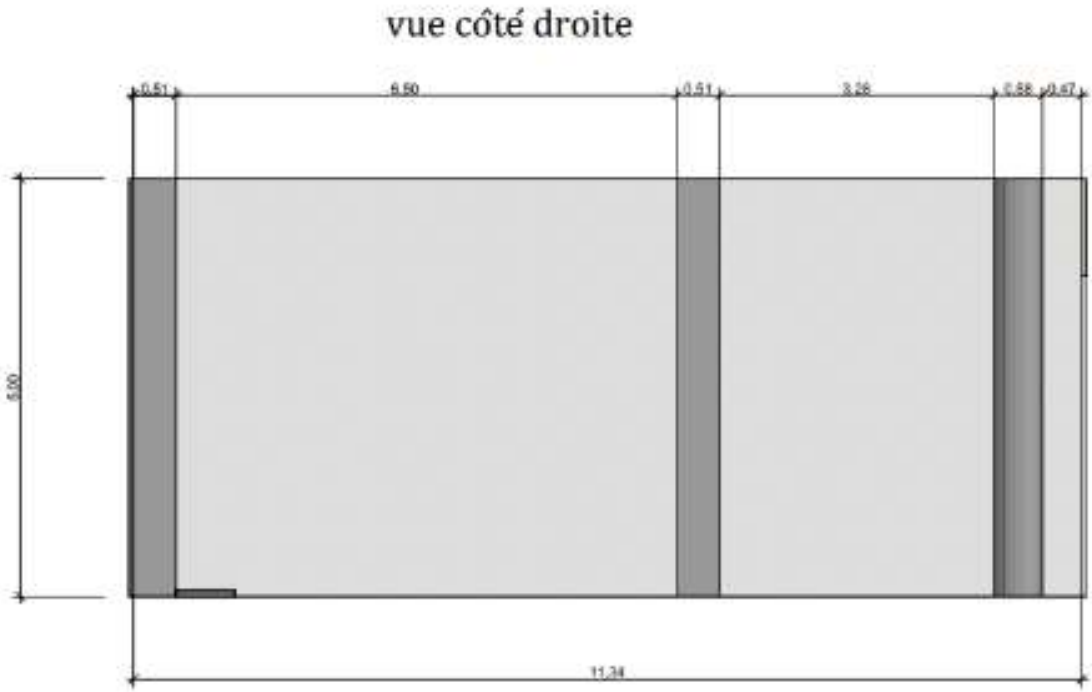

Ouvrage : Restaurant immersif 15 Terr. de l'Université, 92000 Nanterre		Maître d'ouvrage: Léa Froger			Maître d'oeuvre Alon Marec / Mohamed Sahim 12 rue Anatole France , 92000 Nanterre		
N° de plan:	Titre:	Echelle :	Format :	N° de projet :	Dessinateur:	Date :	Etat du projet :
2	Elévations	1:50	A3	1	Alon / Mohamed	12/03/2026	Existant


Façade

EXISTANT

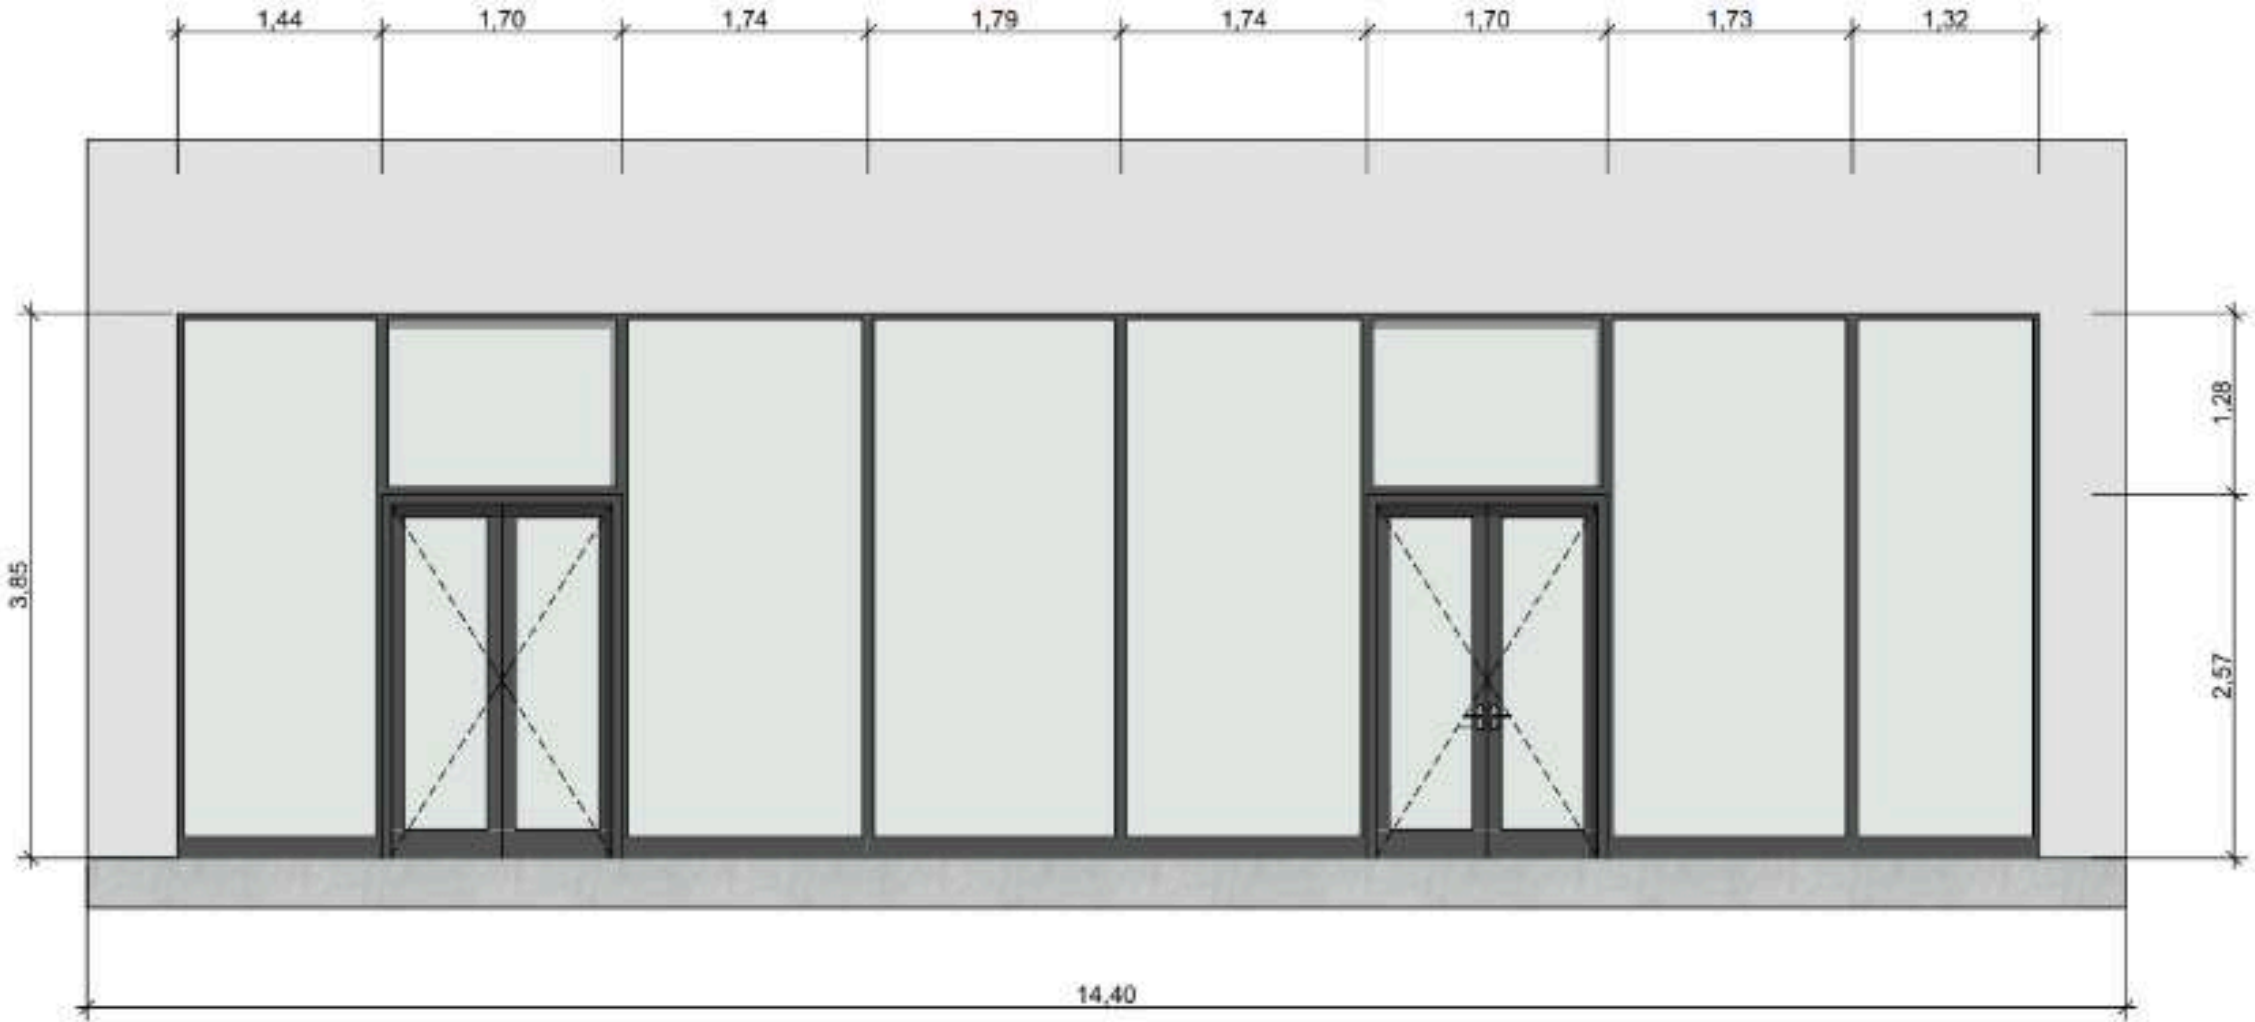


Ouvrage : Restaurant immersif 15 Terr. de l'Université, 92000 Nanterre		Maitre d'ouvrage: Léa Froger			Maitre d'oeuvre Alon Marec / Mohamed Sahim 12 rue Anatole France , 92000 Nanterre		
N° de plan: 3	Titre: Facade	Echelle : 1:50	Format : A3	N° de projet : 1	Dessinateur: Alon / Mohamed	Date : 12/03/2026	Etat du projet : Existant

Moodboard

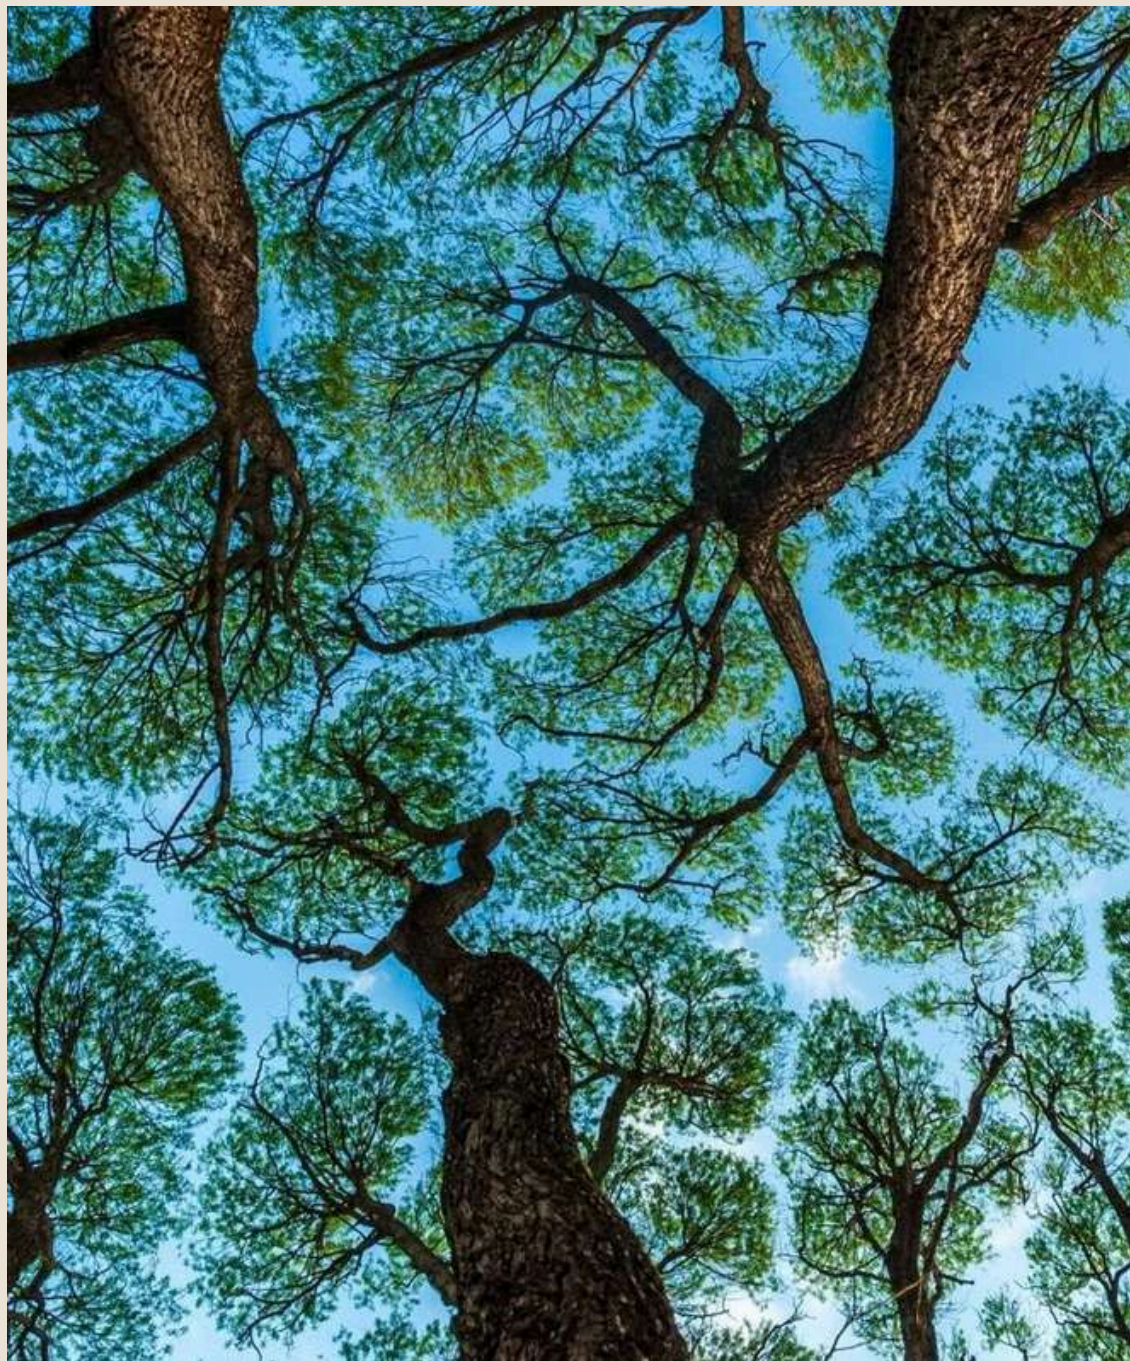

Séparation

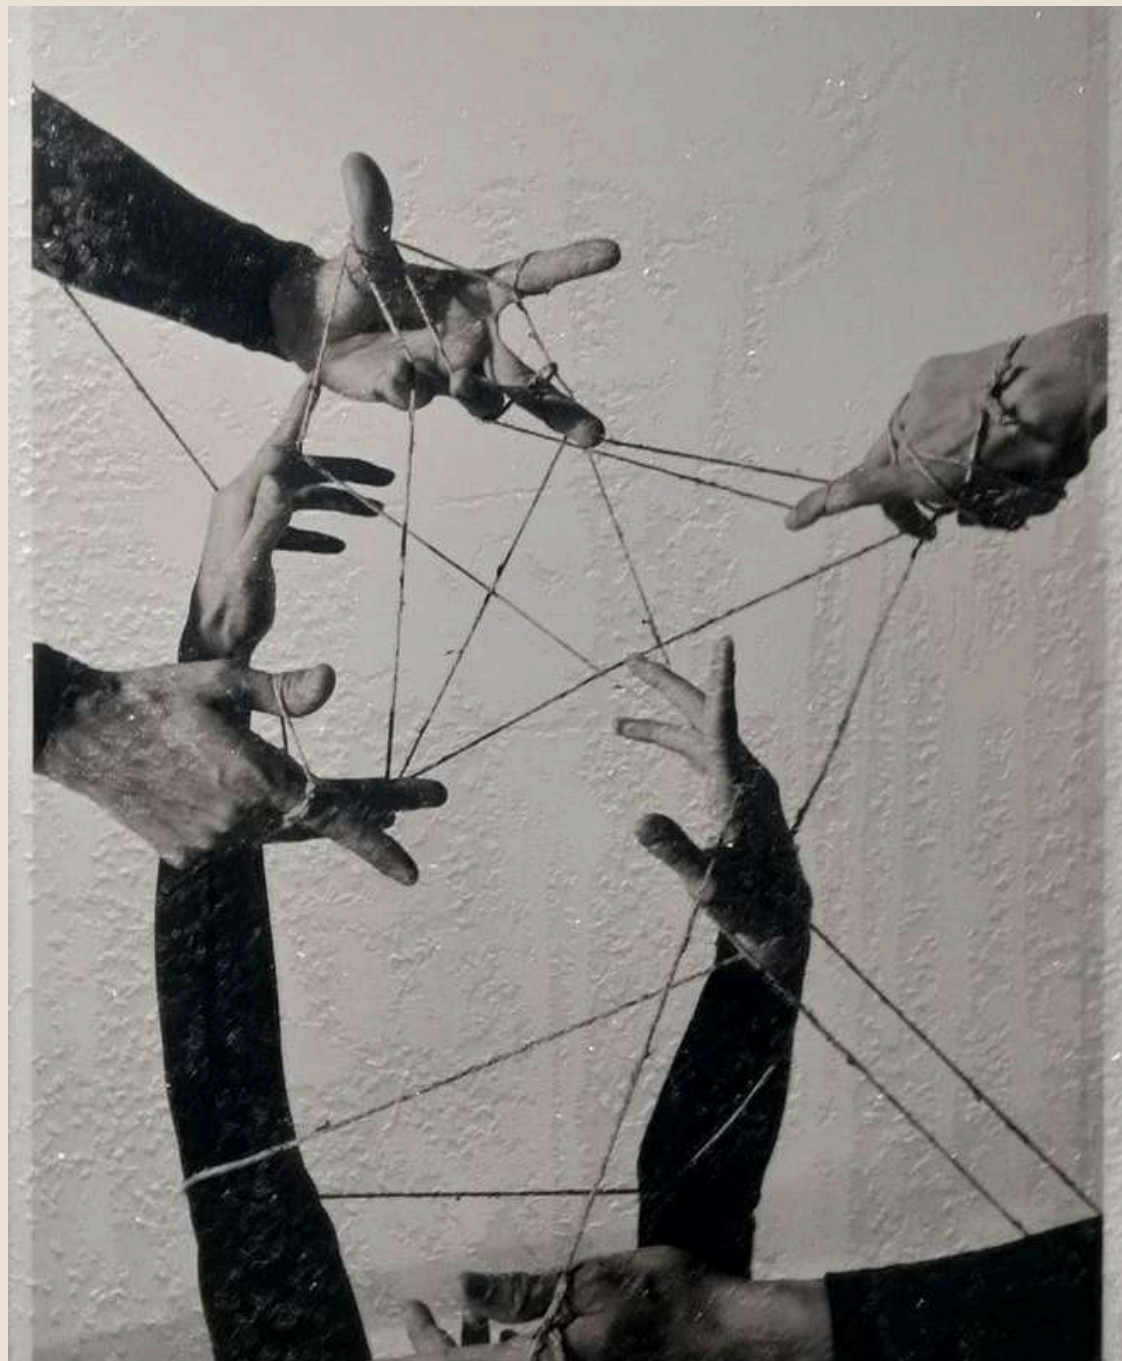


Tension




Transfert

Croquis maquette


L'objectif était de donner une forme architecturale aux trois états de la matière solide, liquide et gazeux en les reliant au thème central du projet : la chaleur, élément fondamental du restaurant et du geste culinaire.

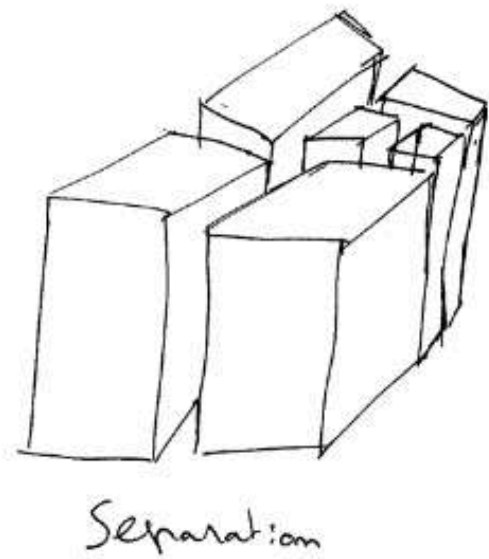

Séparation

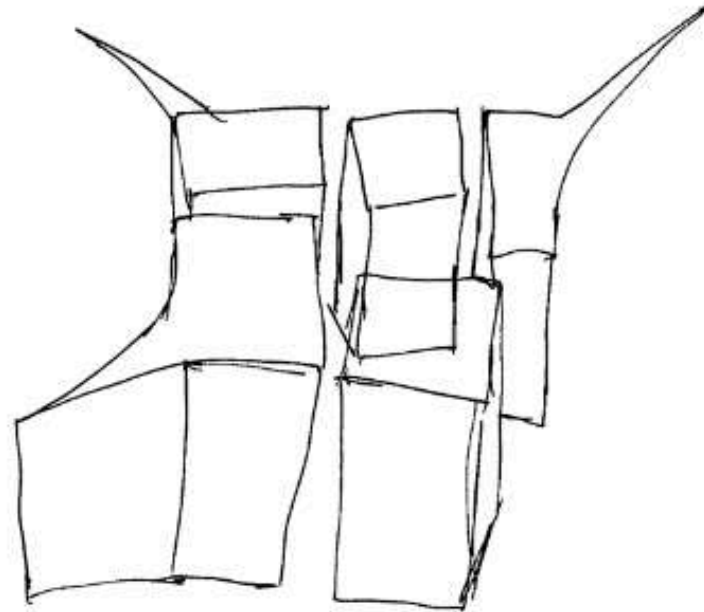

Tension dans la
séparation

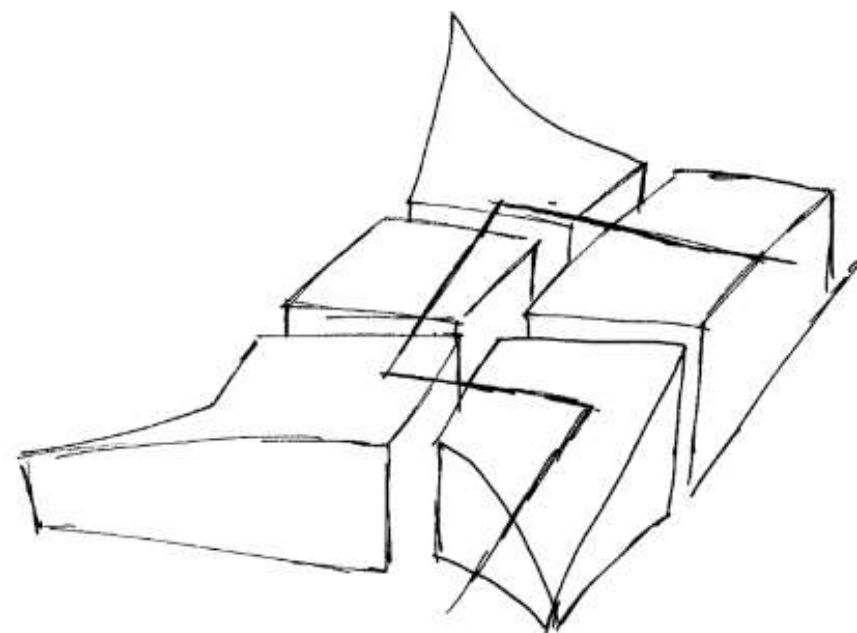

Transition

■ Dans ce premier dessin, nous travaillons l'idée de masse et de fragmentation, caractéristiques du solide. Les volumes sont compacts, ancrés, presque immobiles. La **séparation** entre les blocs symbolise la stabilité et la rigidité du solide.

■ Le deuxième croquis explore la transition : on n'est plus dans la rigidité, mais pas encore dans la légèreté. Les formes commencent à se déformer, à s'étirer.

La **tension** représente l'énergie de la chaleur en train d'agir sur la matière. Les surfaces deviennent plus souples, les volumes s'ouvrent.

■ Le dernier croquis traduit l'état gazeux, symbolisé par des formes beaucoup plus légères et expansives. Les volumes se déploient, s'étirent, se libèrent.

On sent le **transfert**, l'idée de dispersion.

La Maquette final



SEPARATION

TENSION

TRANSFERT



Béton ciré

Continuité et sobriété, base
minérale uniforme



verre orangé

Transparence et immersion,
diffusion de la lumière chaude




Textile gris

Confort et douceur, équilibre avec
les matières brutes



Bois noyer

Chaleur et profondeur, présence
naturelle et enveloppante

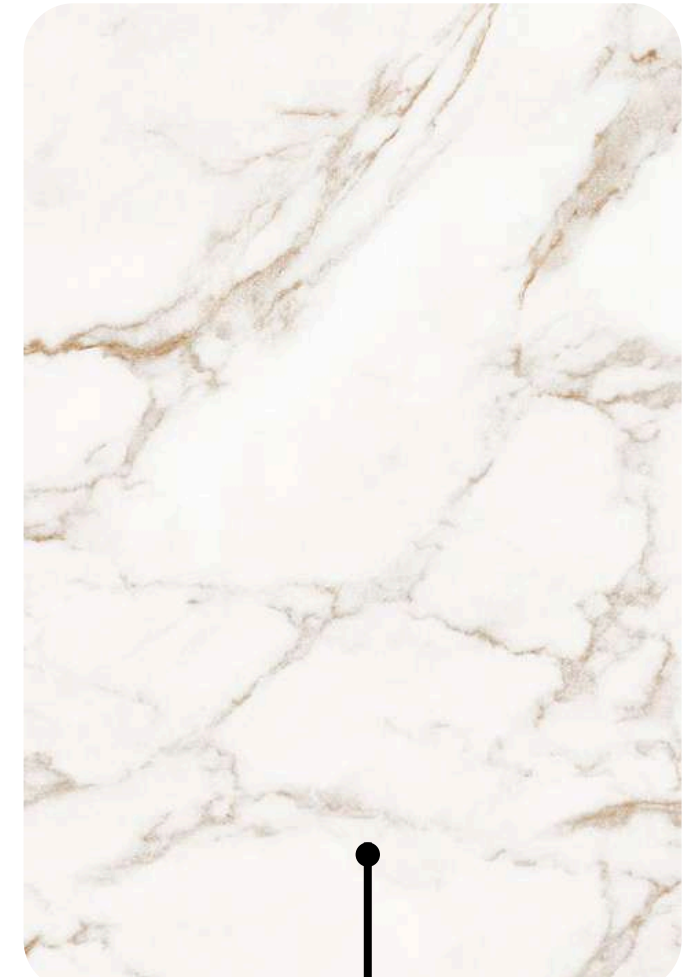


Marbre blanc

Élégance et contraste, surface
minérale structurée

Plan

ZOONNING RDC

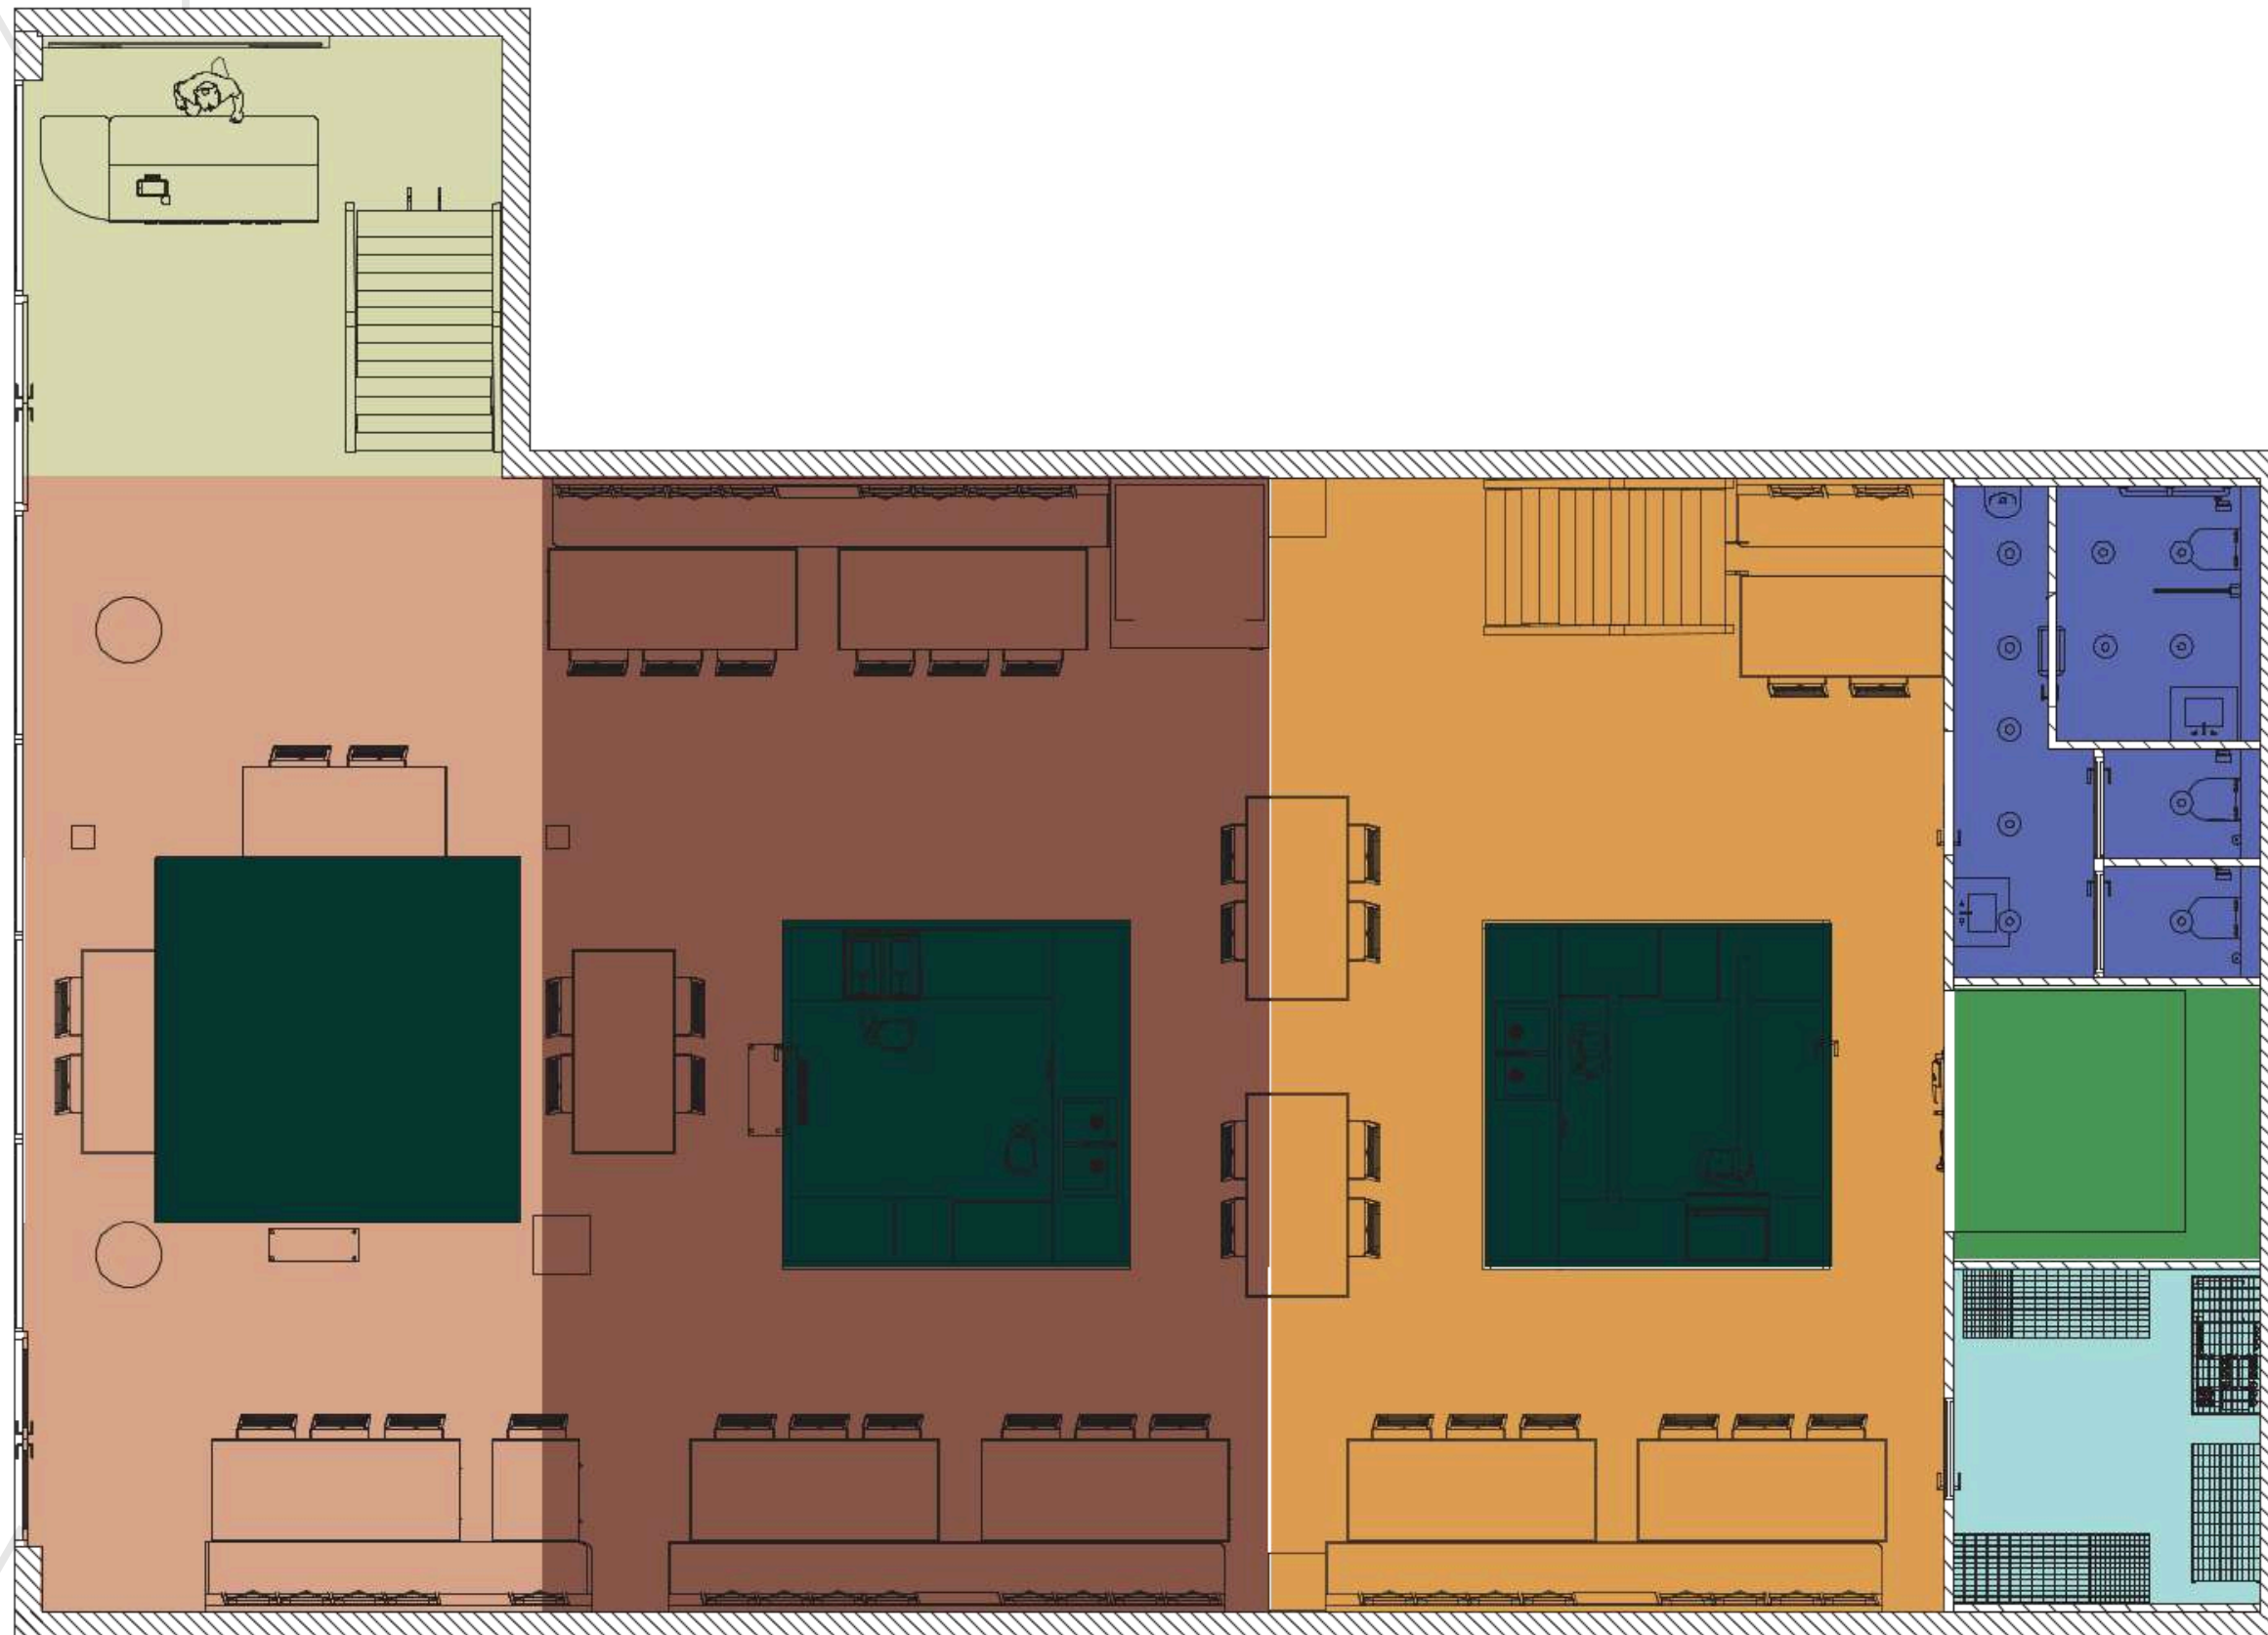

ESPACE D'ACCEUIL



ESPACE DE DÉGUSTATION - ÉTAT GAZEUX



ESPACE DE DÉGUSTATION - ÉTAT LIQUIDE



ESPACE DE DÉGUSTATION - ÉTAT SOLIDE



TOILETTES / TOILETTE PMR



CHAMBRE FROIDE




RÉSERVE



CUISINES

Plan

ZOONNING R+1

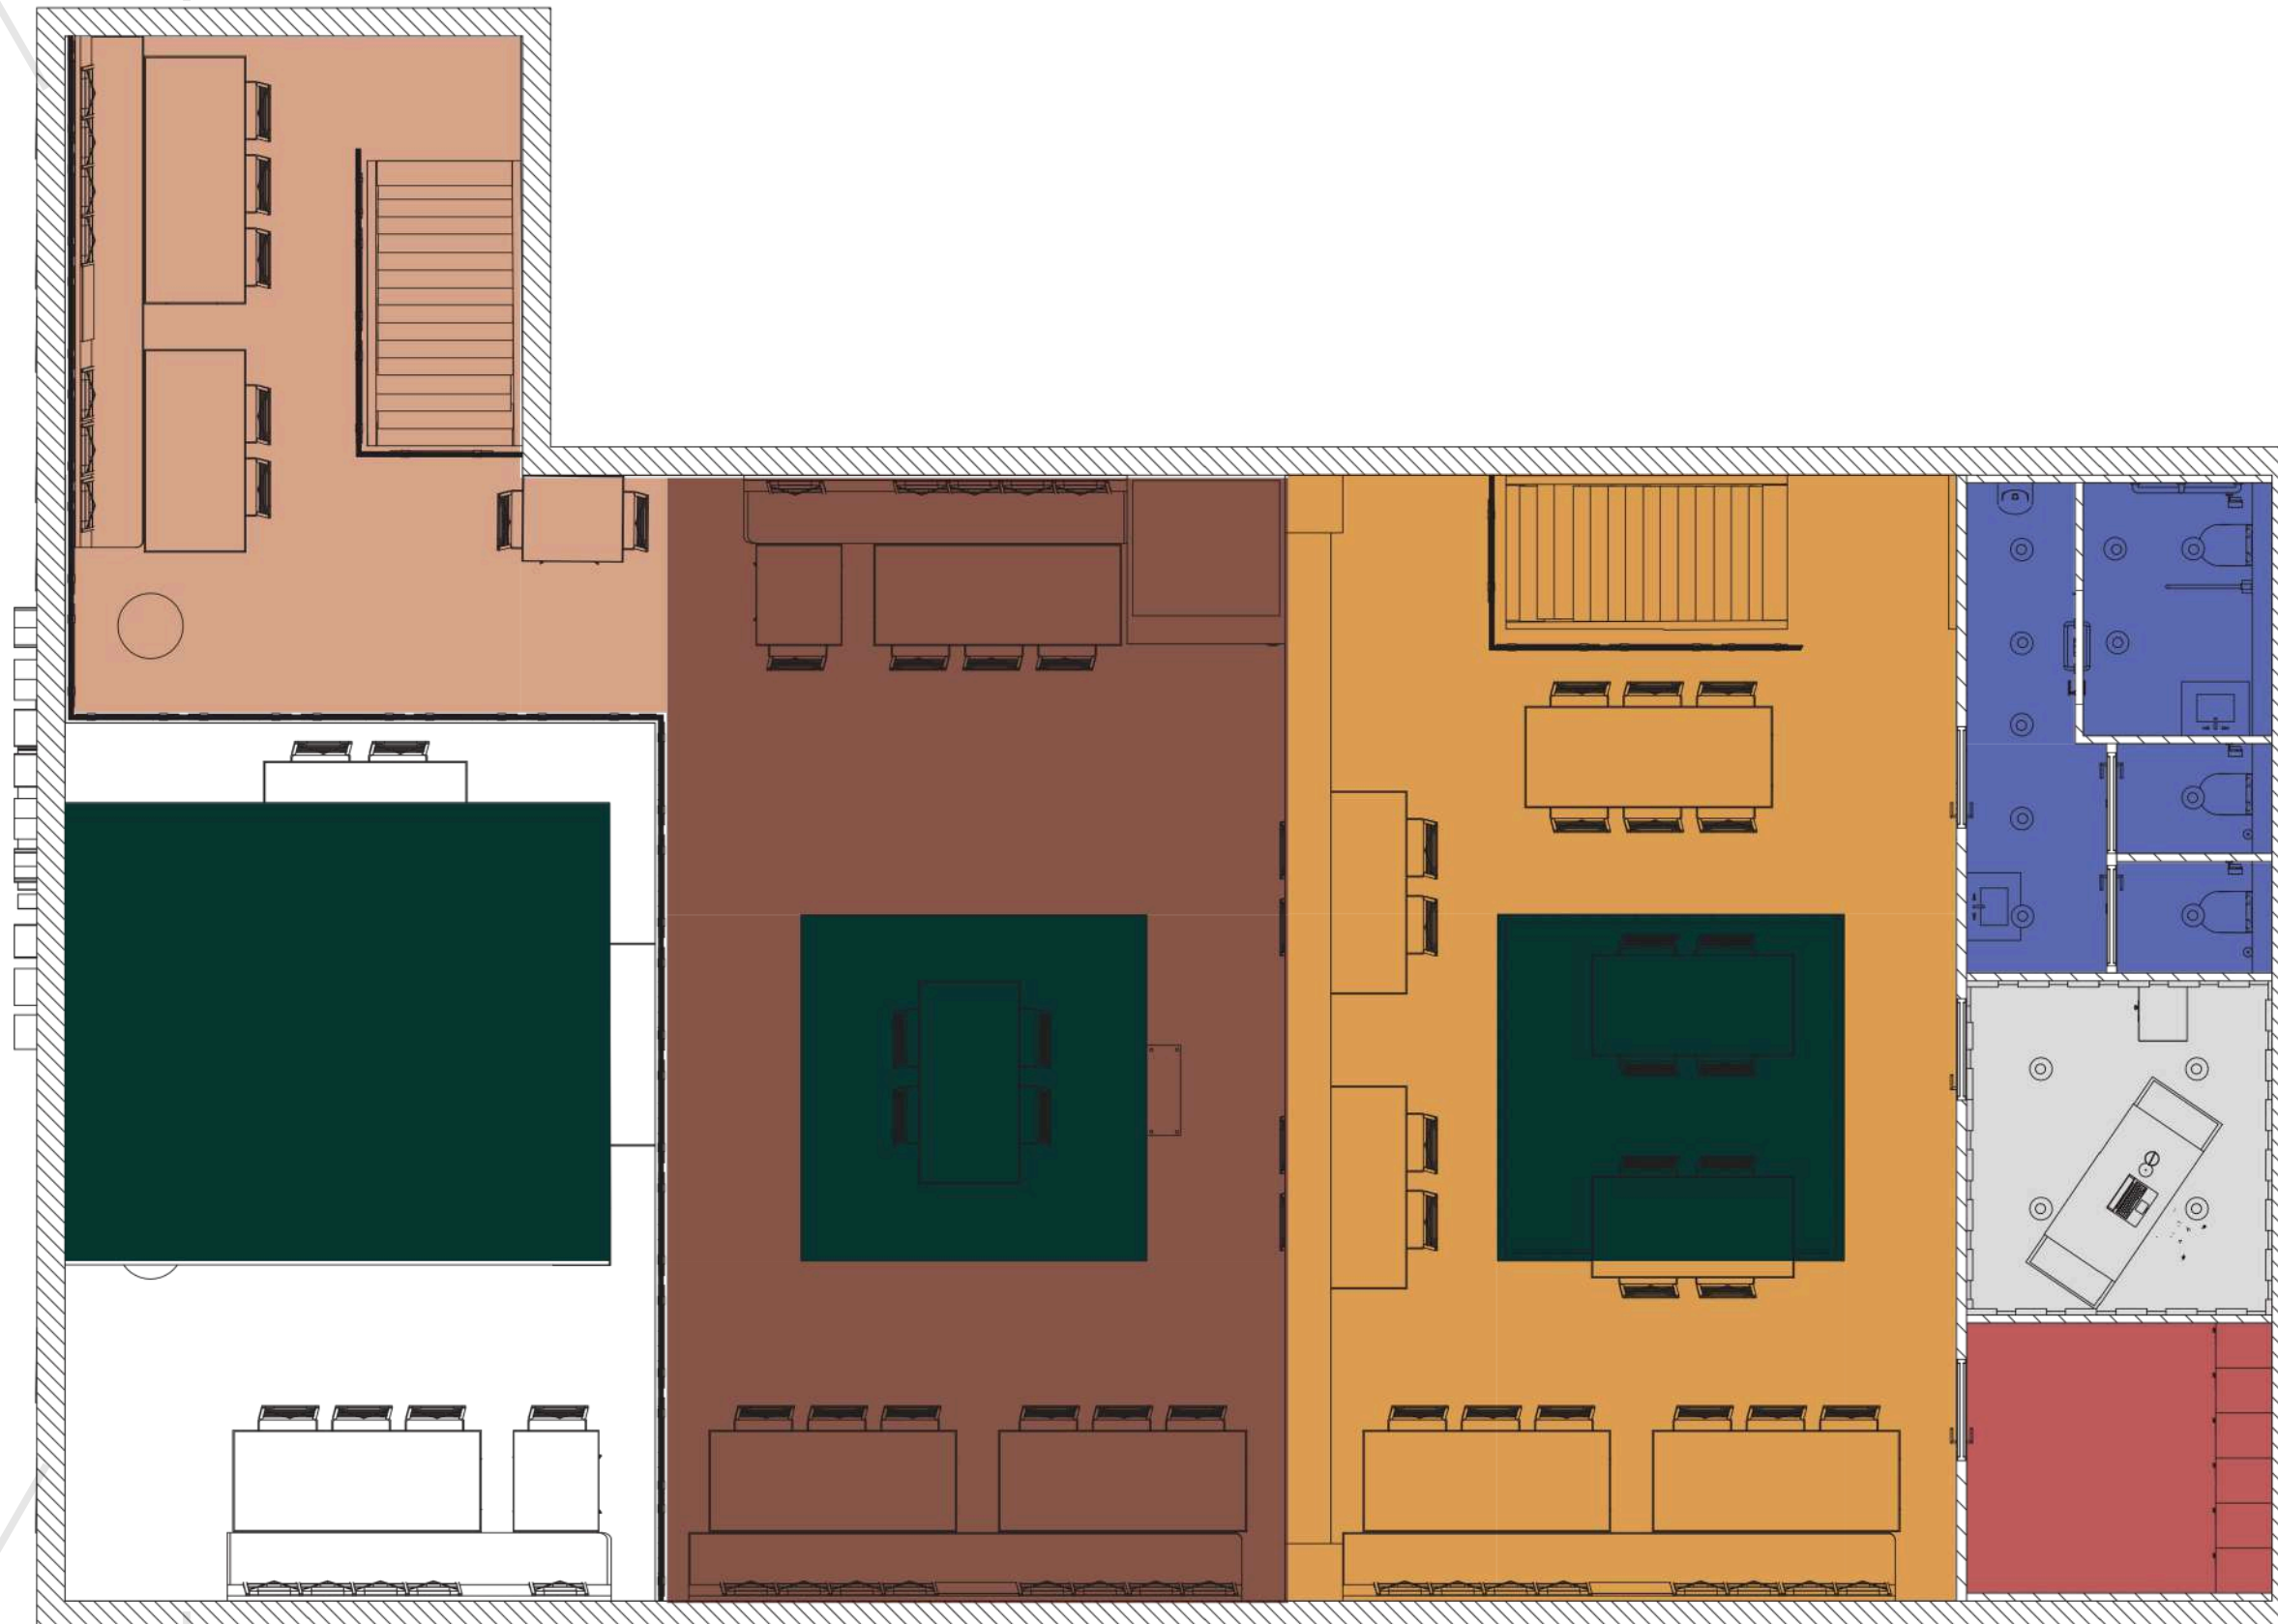

ESPACE DÉGUSTATION - ETAT GAZEUX



ESPACE DÉGUSTATION - ETAT LIQUIDE



ESPACE DÉGUSTATION - ETAT SOLIDE



TOILETTES / TOILETTE PMR



BUREAU



VESTIAIRE



CUISINES

Plan

PROJETÉ RDC



Ouvrage MATSAV ZOR 25 Terr de l'université,92000 Nanterre		Maitre d'oeuvre Léa Froger		Maitre D'ouvrage Marec Alon / Sahim Mohamed 12 rue Anatole France ,92000 Nanterre	
Titre Plan projeté RDC		Echelle A3	Format 1/50	Date 30/04/2026	Etat du projet Projeté

Plan


PROJETÉ R+1



Ouvrage MATSAV ZOR 25 Terr de l'université,92000 Nanterre		Maitre d'oeuvre Léa Froger		Maitre D'ouvrage Marec Alon / Sahim Mohamed 12 rue Anatole France ,92000 Nanterre	
Titre Plan projeté R+1		Echelle A3	Format 1/50	Date 30/04/2026	Etat du projet Projeté

Plan

COTER RDC

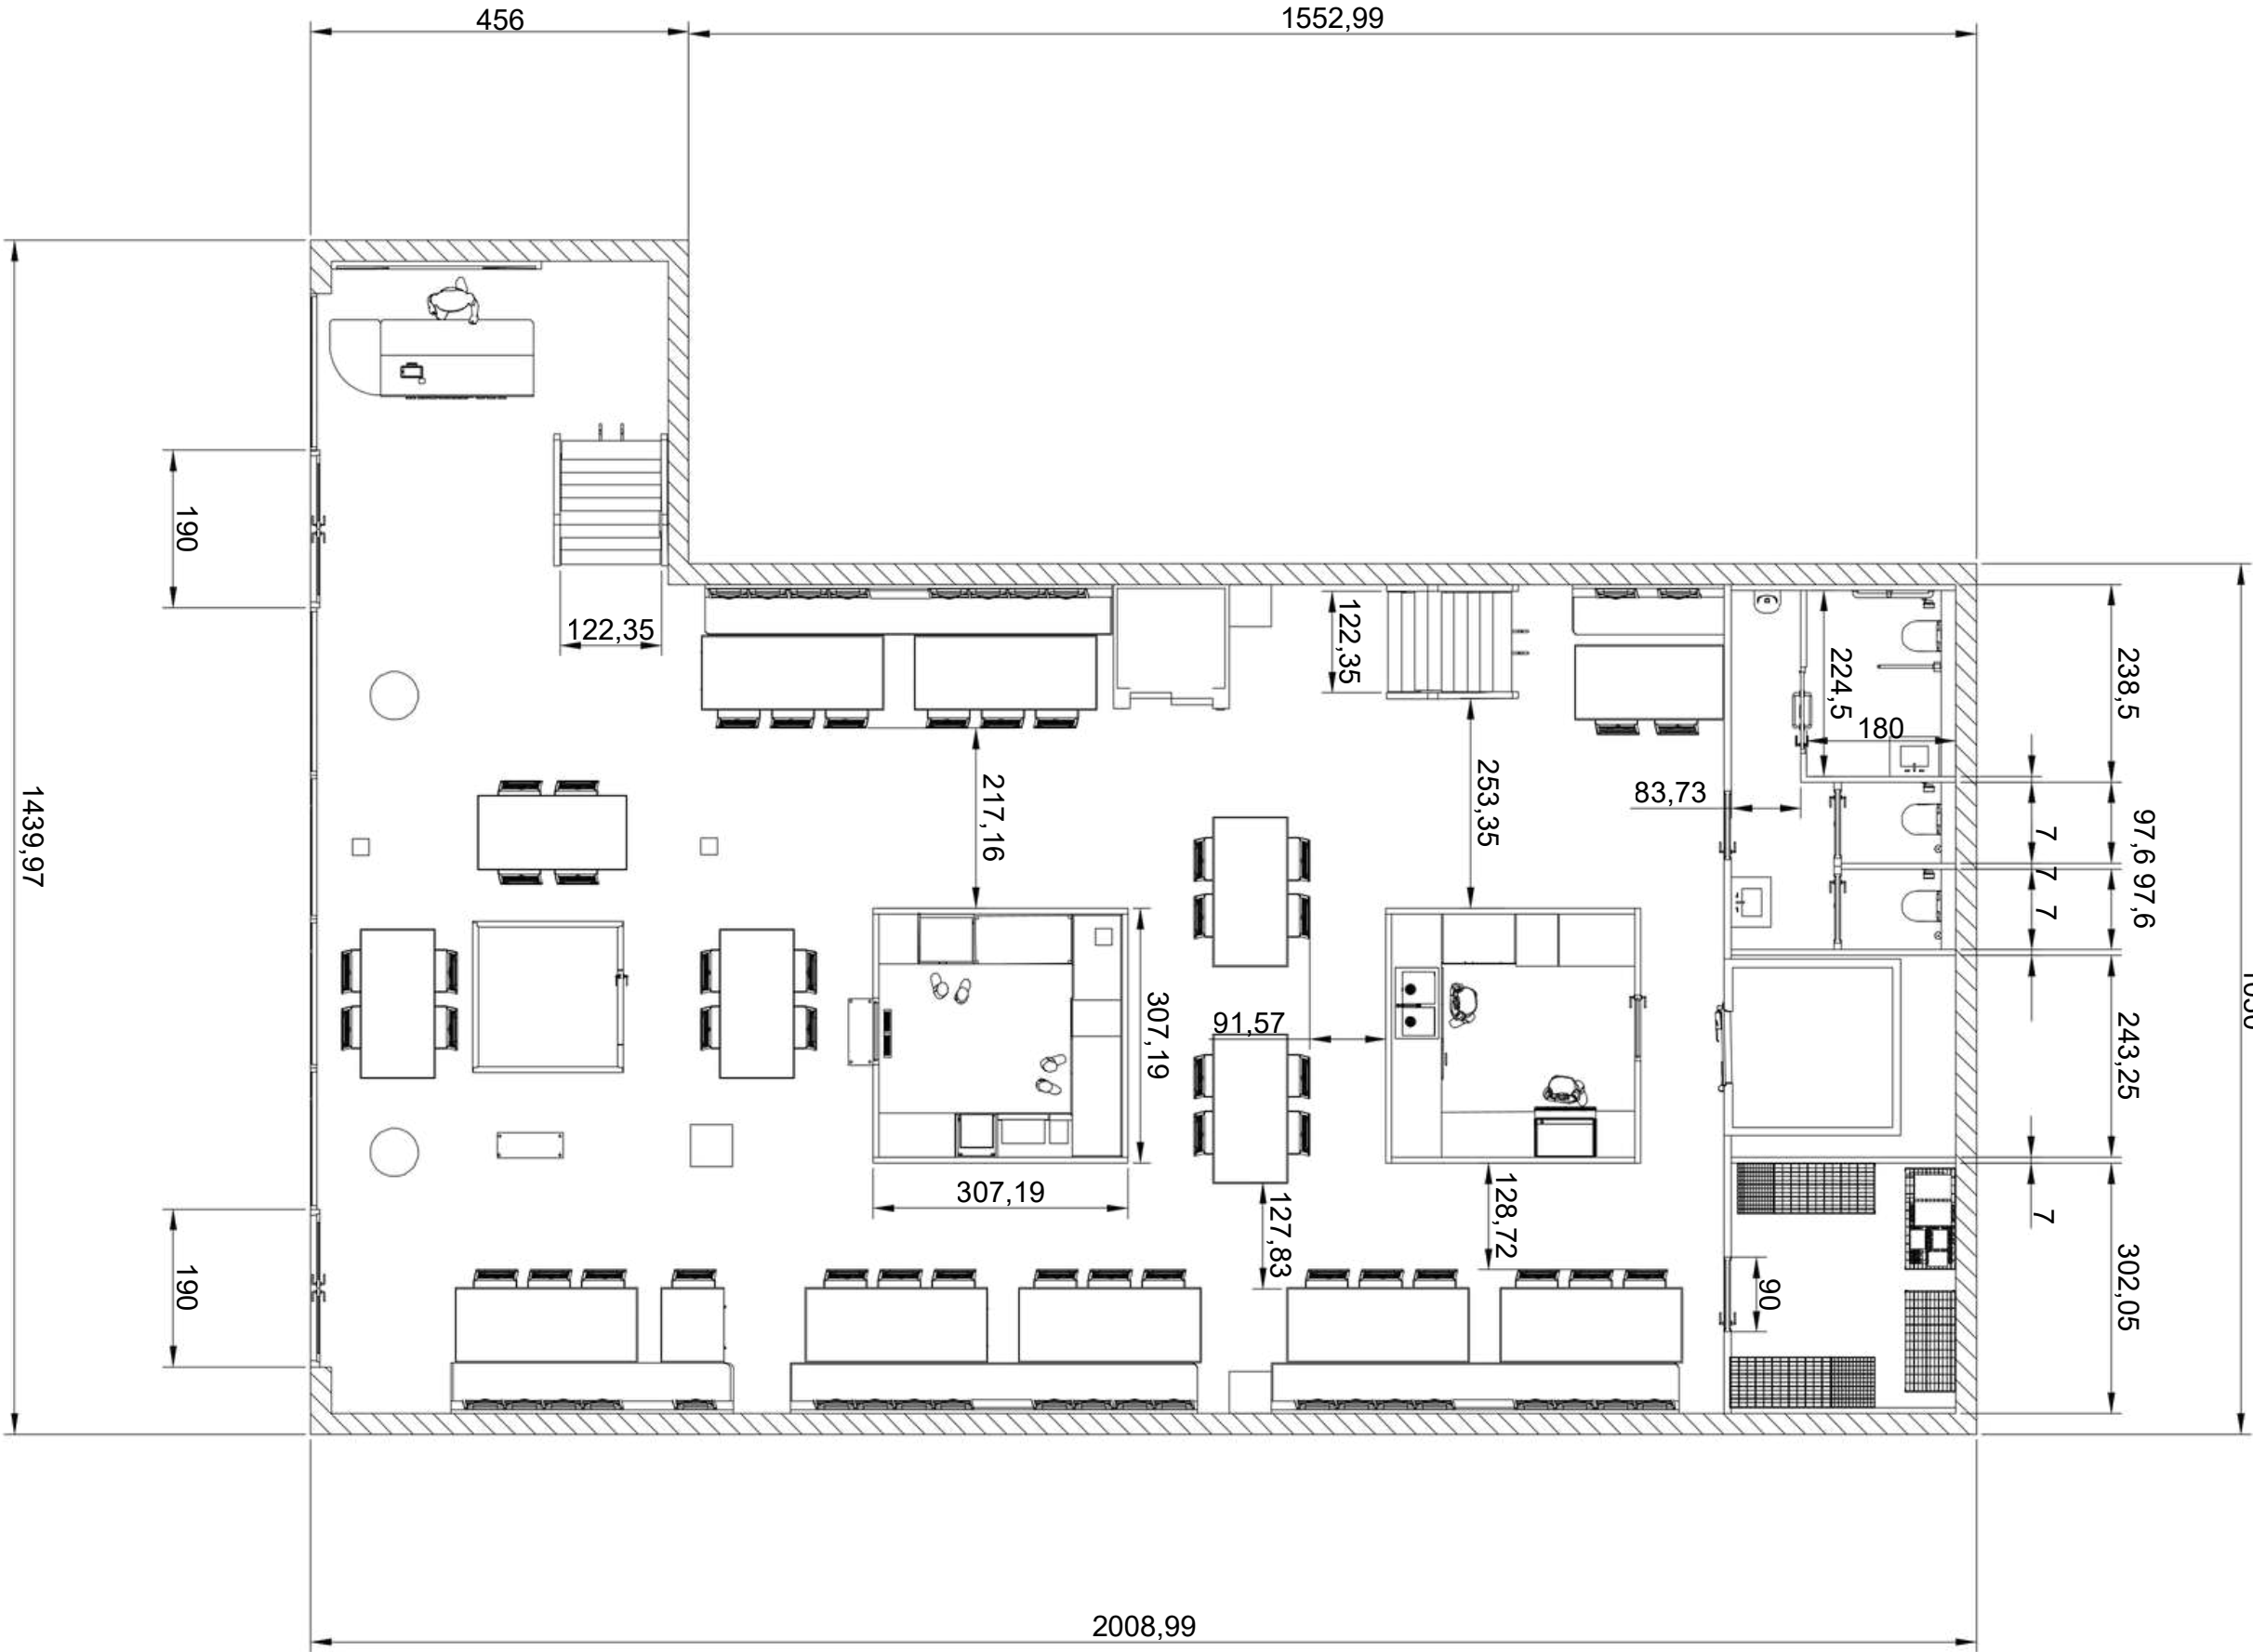

Ouvrage
MATSAV ZOR
25 Terr de l'université,92000 Nanterre

Maitre d'oeuvre
Léa Froger

Maitre D'ouvrage
Marec Alon / Sahim Mohamed
12 rue Anatole France ,92000 Nanterre

Titre
Plan coter RDC

Echelle
A3


Format
1/50

Date
30/04/2026


Etat du projet
Projeté

Plan

COTER R+1

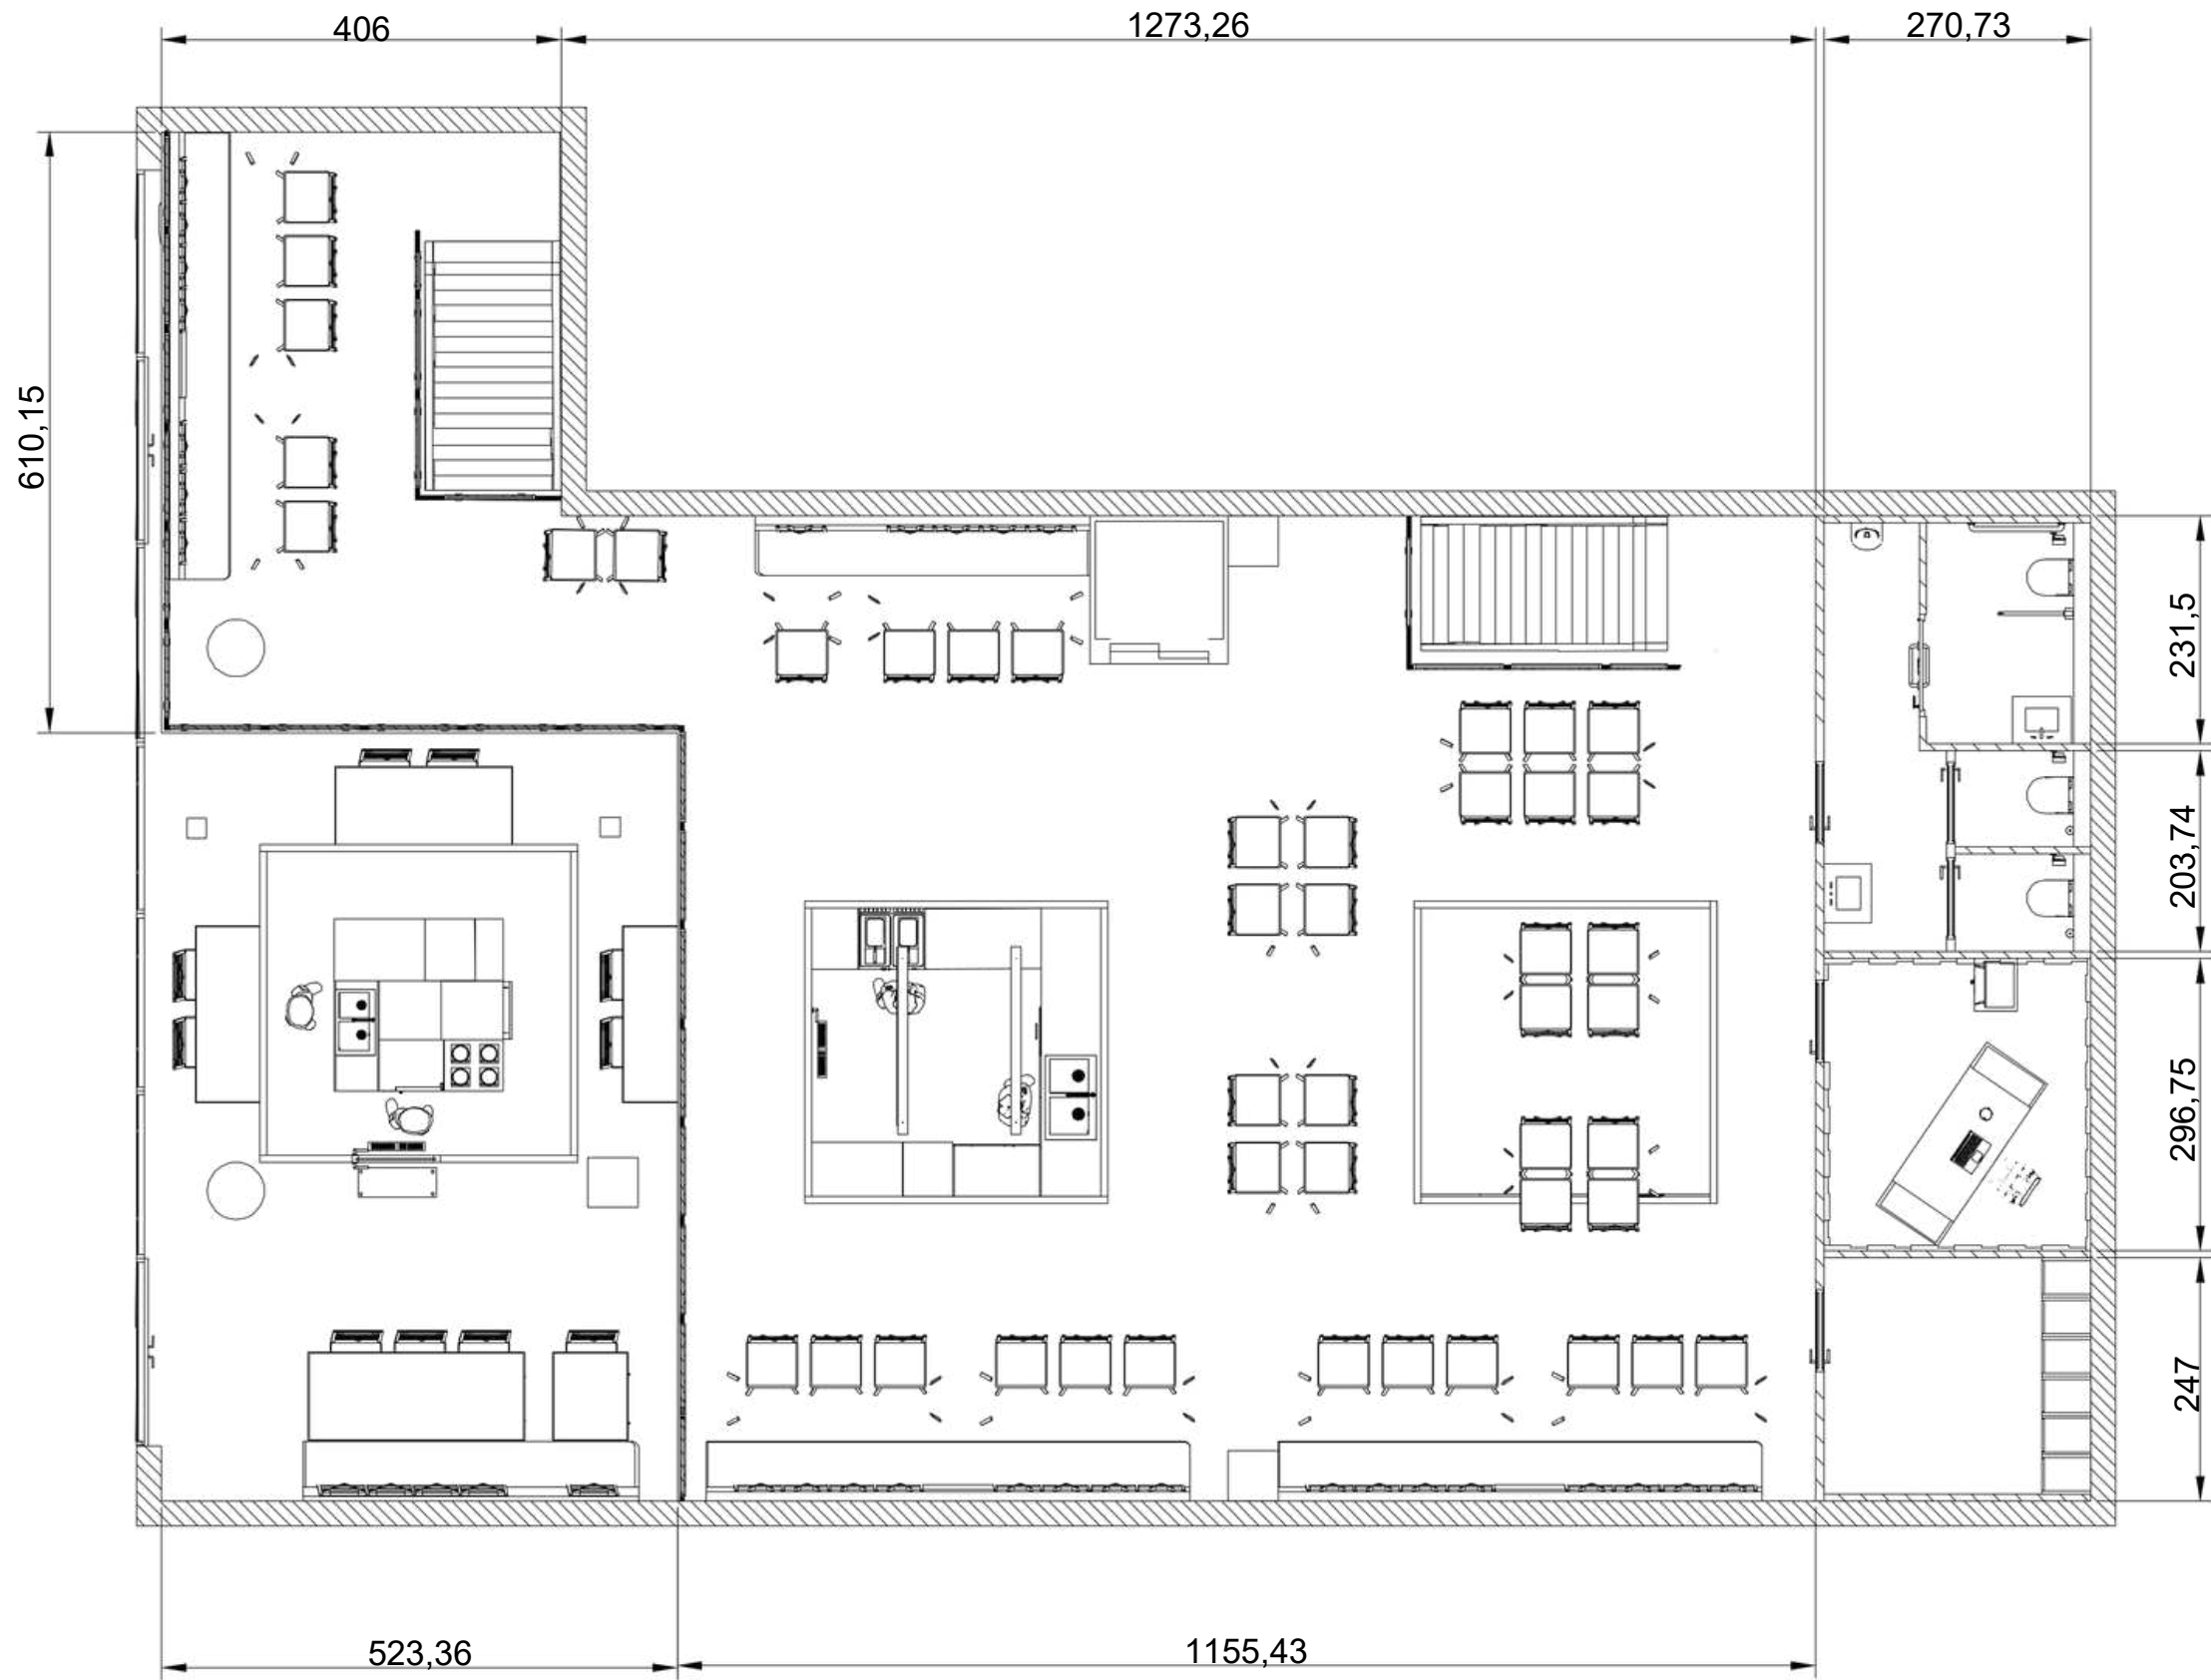

Ouvrage MATSAV ZOR 25 Terr de l'université,92000 Nanterre		Maitre d'oeuvre Léa Froger		Maitre D'ouvrage Marec Alon / Sahim Mohamed 12 rue Anatole France ,92000 Nanterre	
Titre Plan coter R+1		Echelle A3	Format 1/50	Date 30/04/2026	Etat du projet Projeté

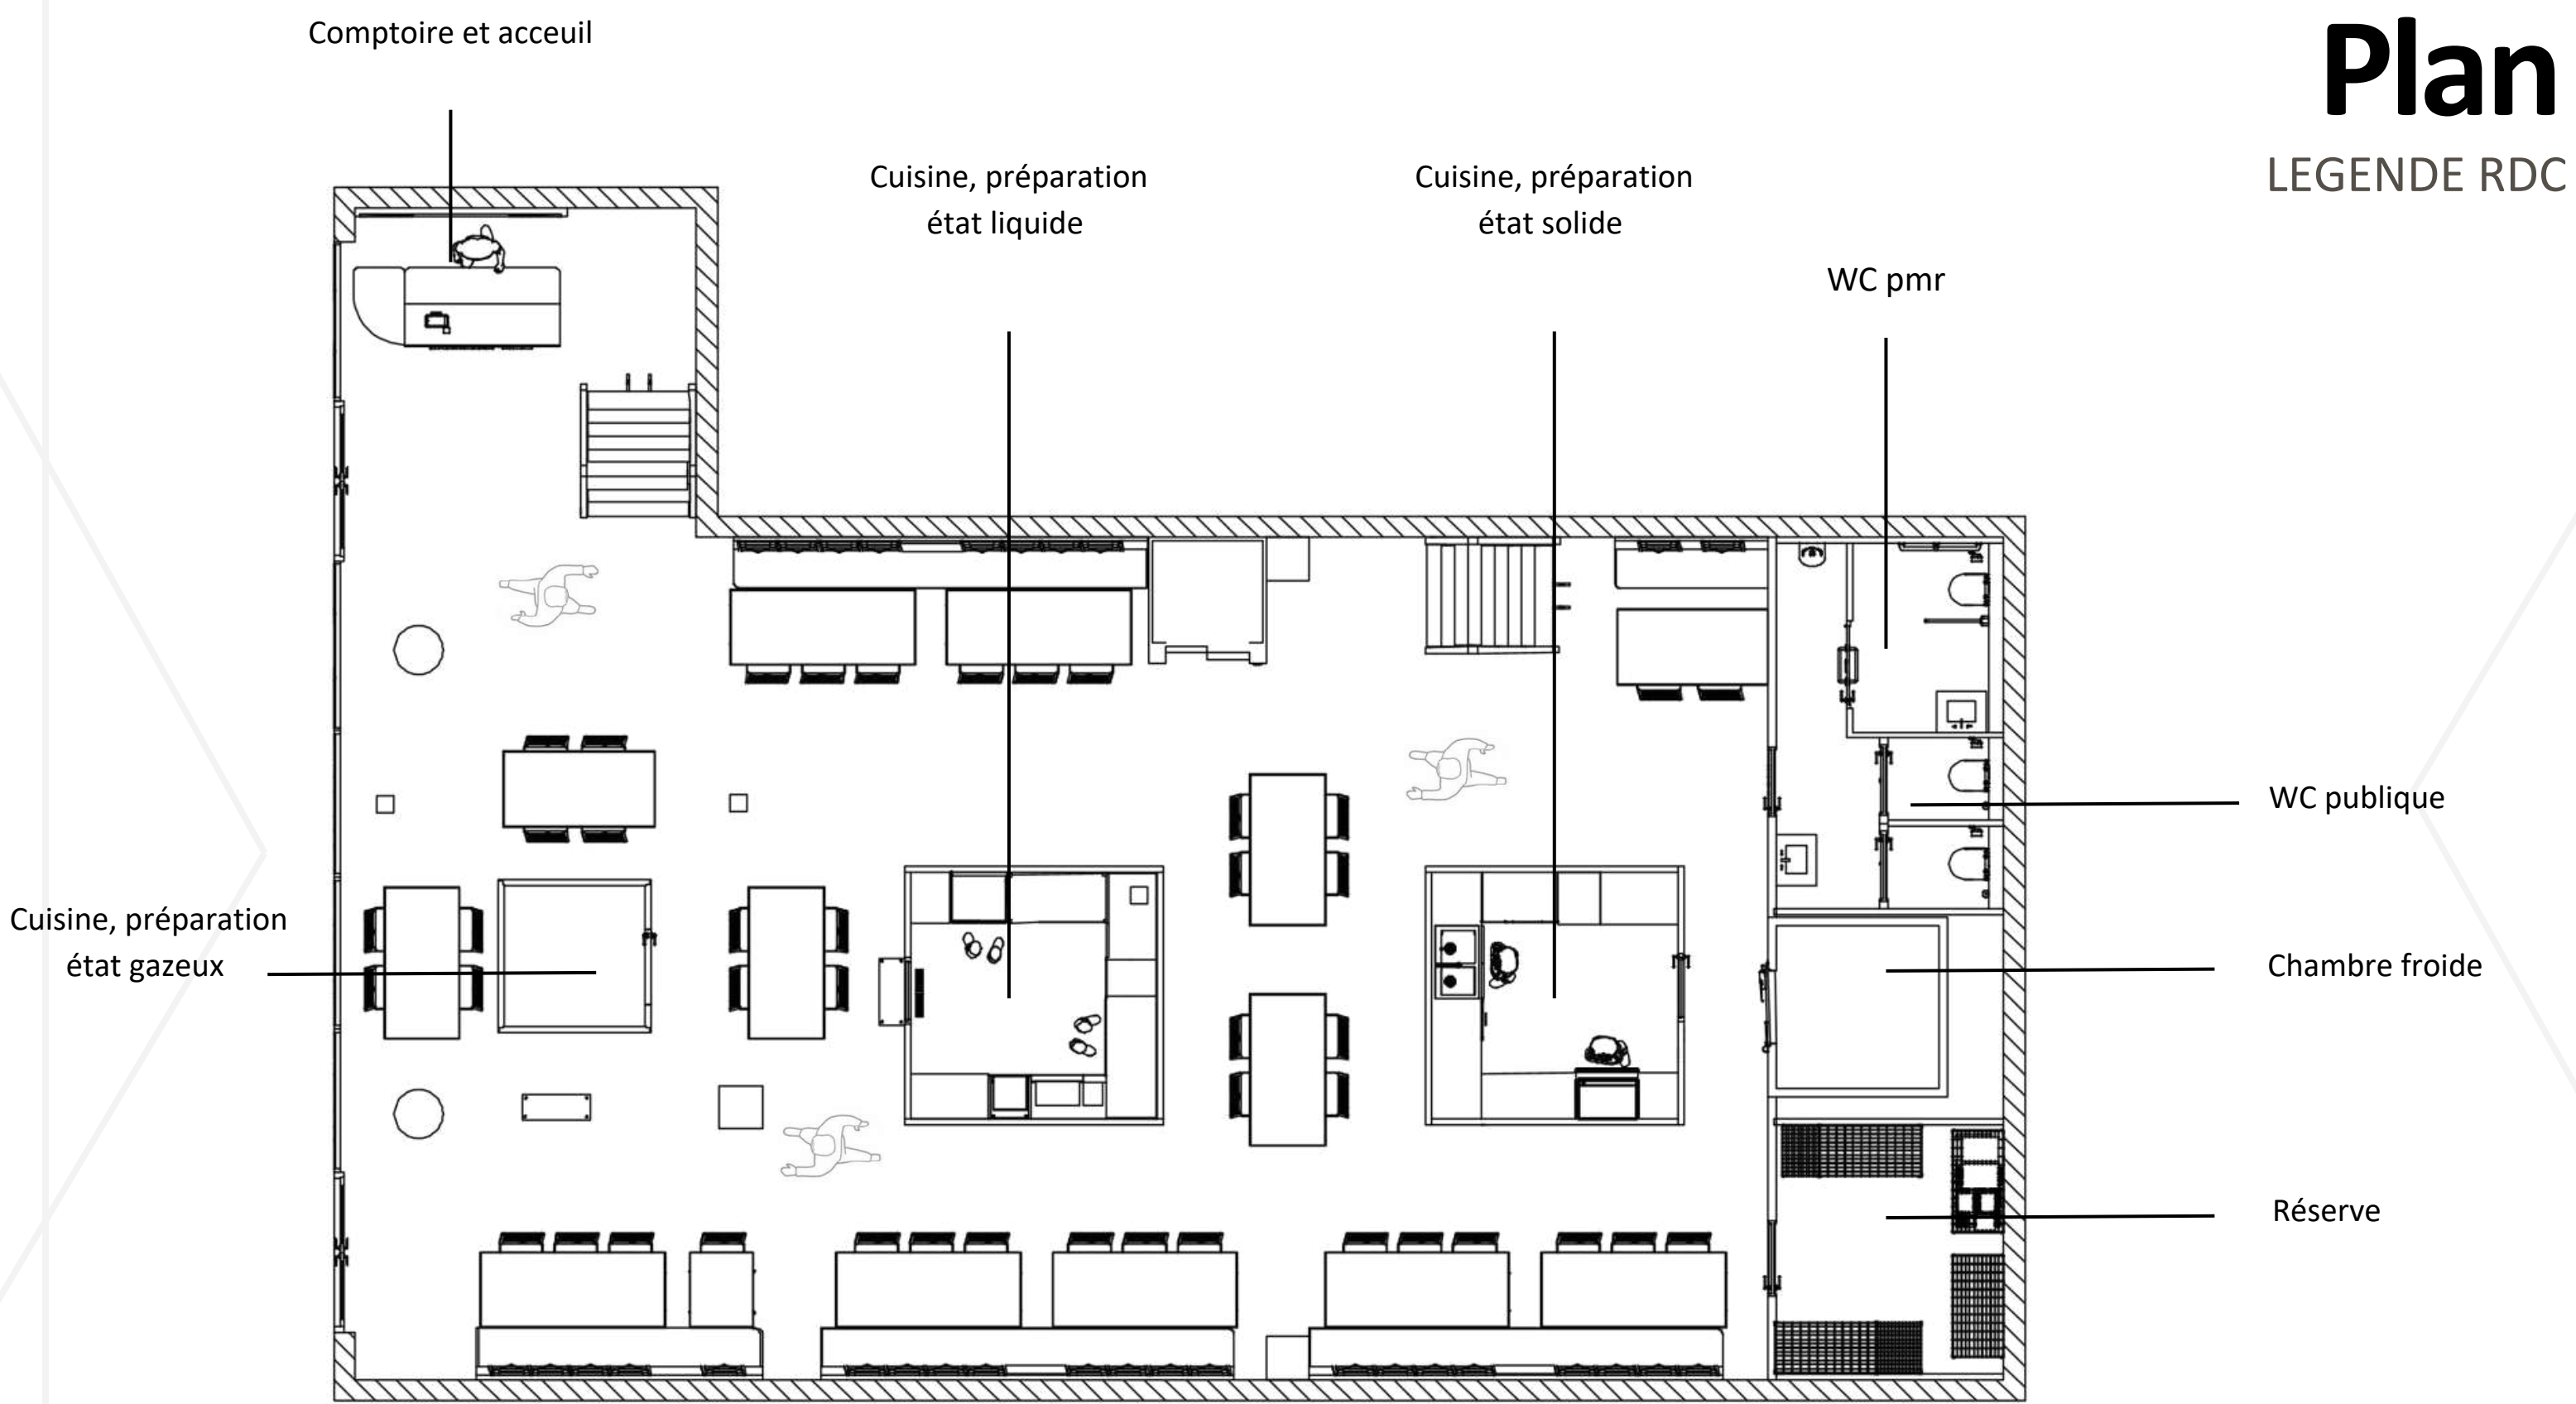


Plan

LEGENDE RDC

Ouvrage MATSAV ZOR 25 Terr de l'université,92000 Nanterre		Maitre d'oeuvre Léa Froger		Maitre D'ouvrage Marec Alon / Sahim Mohamed 12 rue Anatole France ,92000 Nanterre	
Titre Plan légendé RDC		Echelle A3	Format 1/50	Date 30/04/2026	Etat du projet Projeté

Plan

LEGENDE R+1

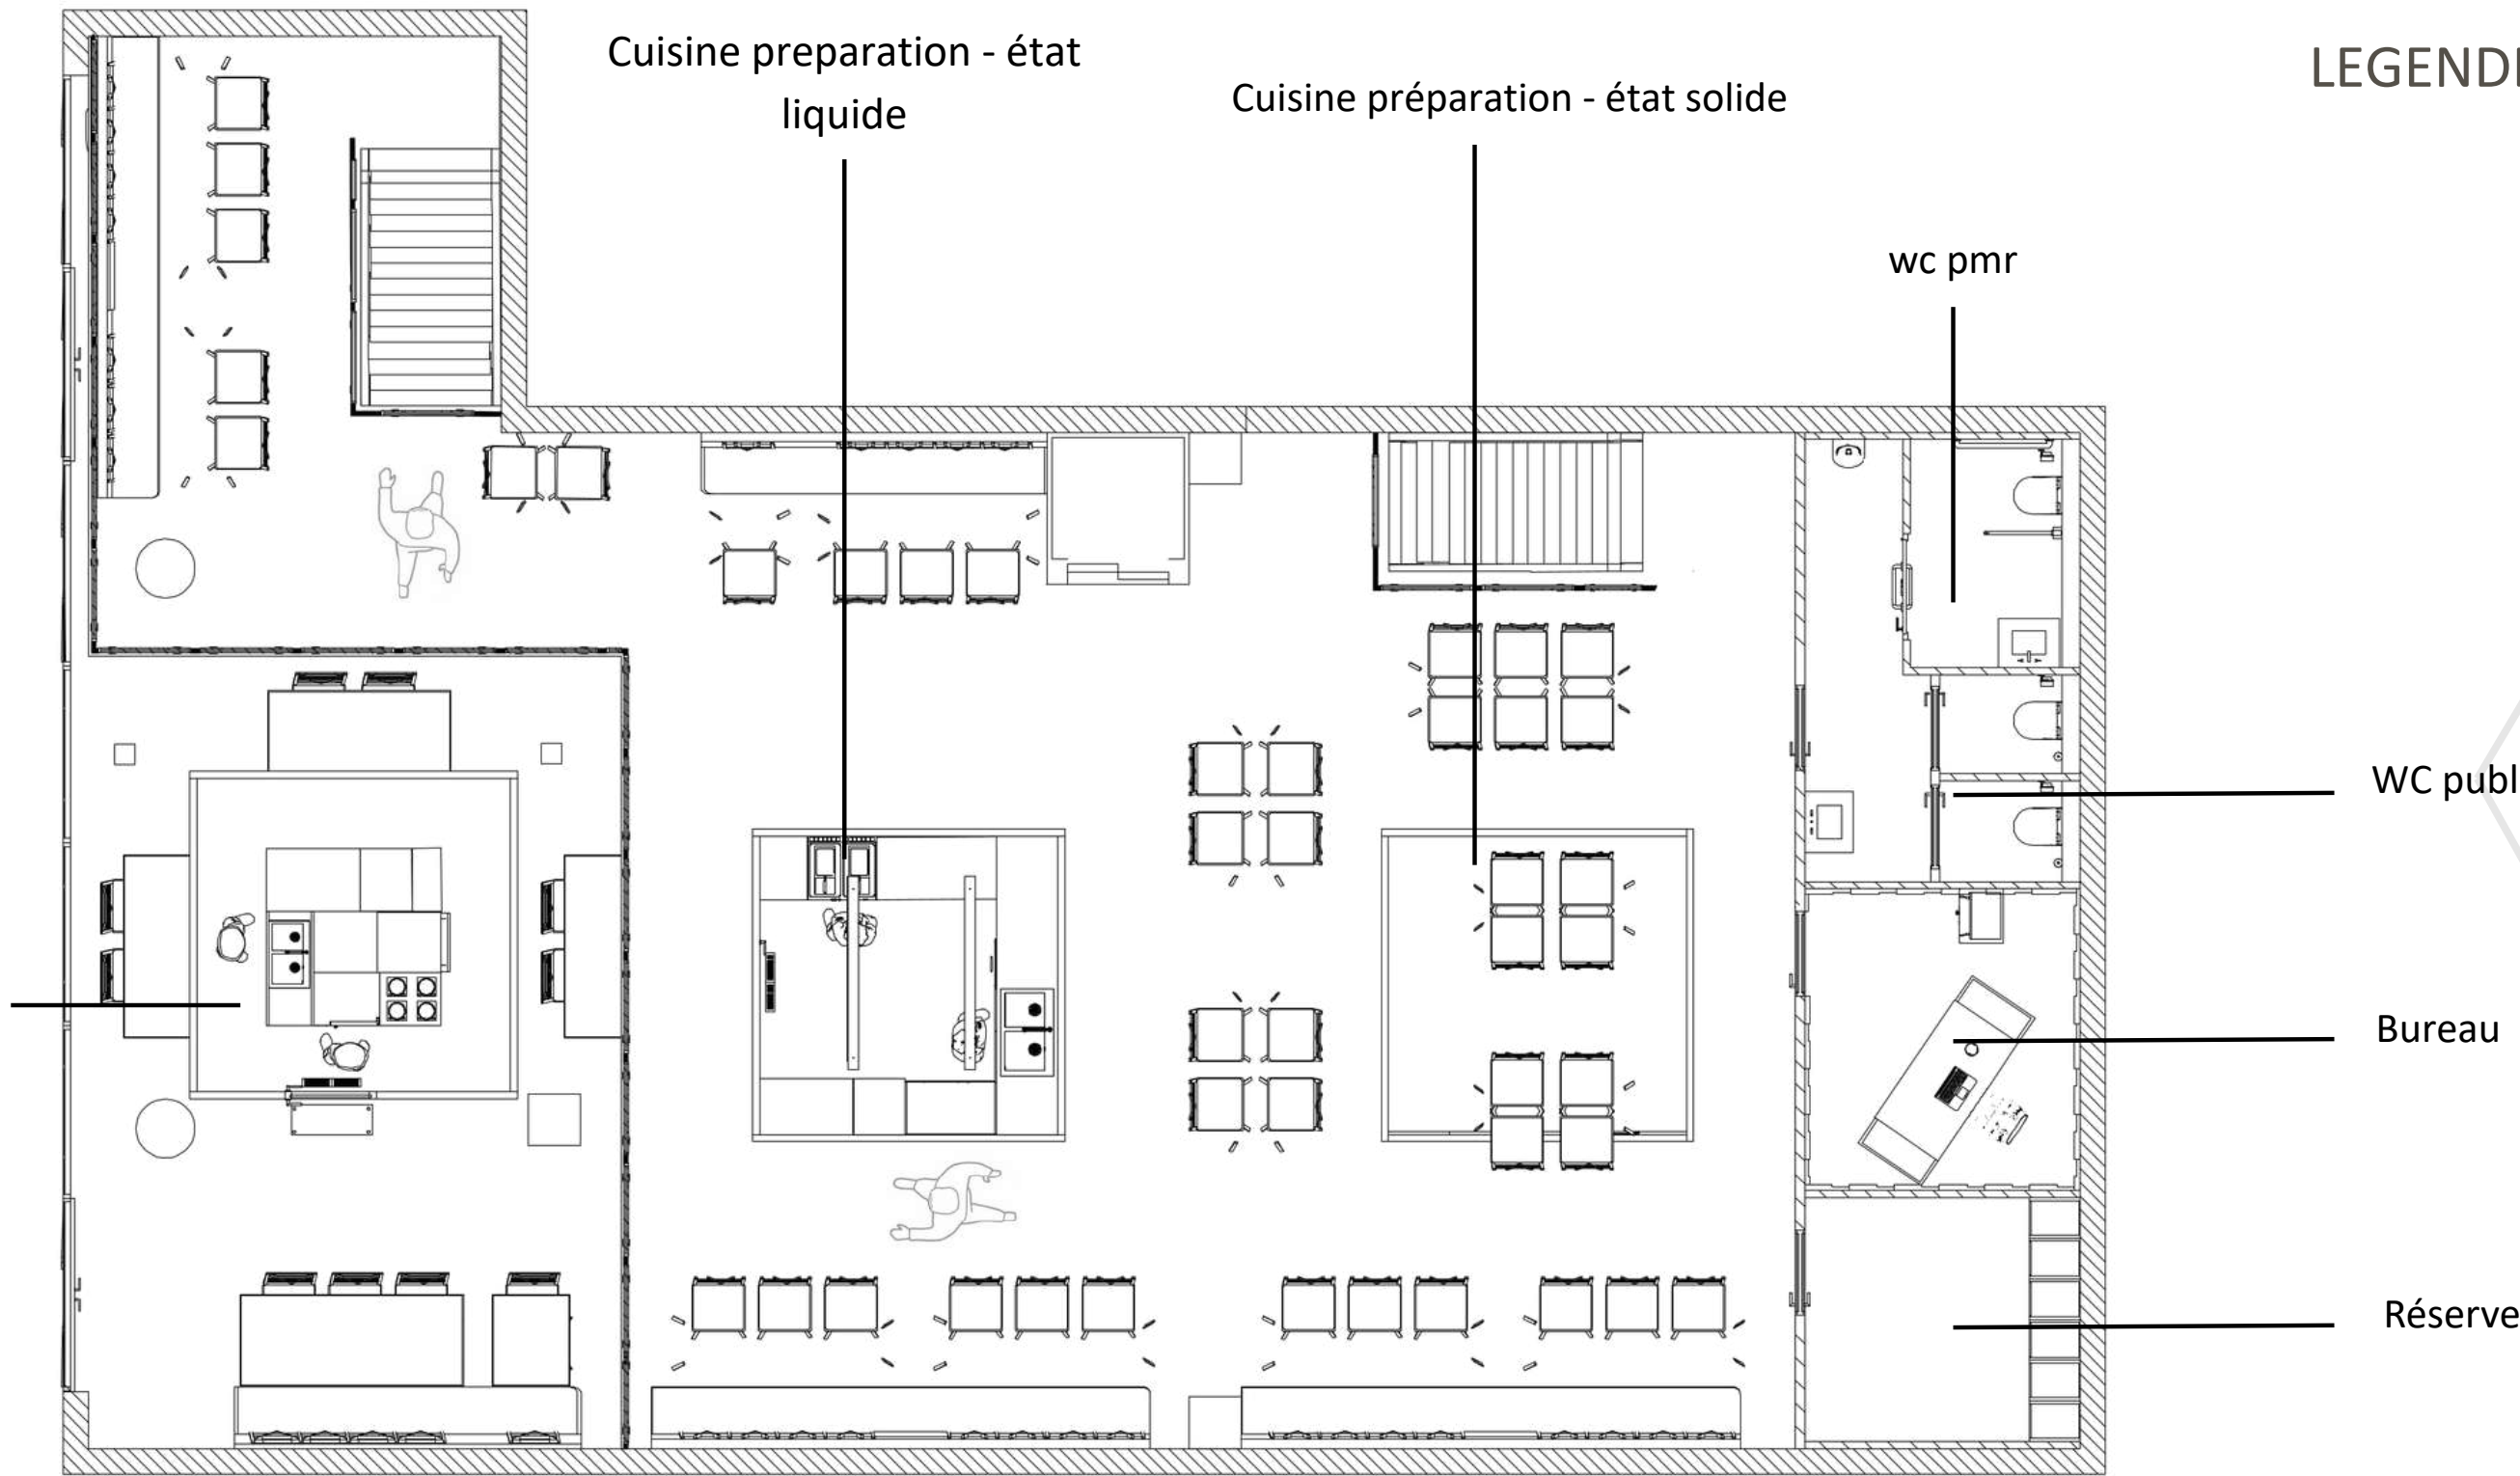


Ouvrage MATSAV ZOR 25 Terr de l'université,92000 Nanterre		Maitre d'oeuvre Léa Froger		Maitre D'ouvrage Marec Alon / Sahim Mohamed 12 rue Anatole France ,92000 Nanterre	
Titre Plan legendé R+1		Echelle A3	Format 1/50	Date 30/04/2026	Etat du projet Projeté

Plan

MIS EN COULEUR RDC

Cuisine équipée du matériel
nécessaire à la préparation de
plats réalisés avec de la chaleur à
l'état gazeux

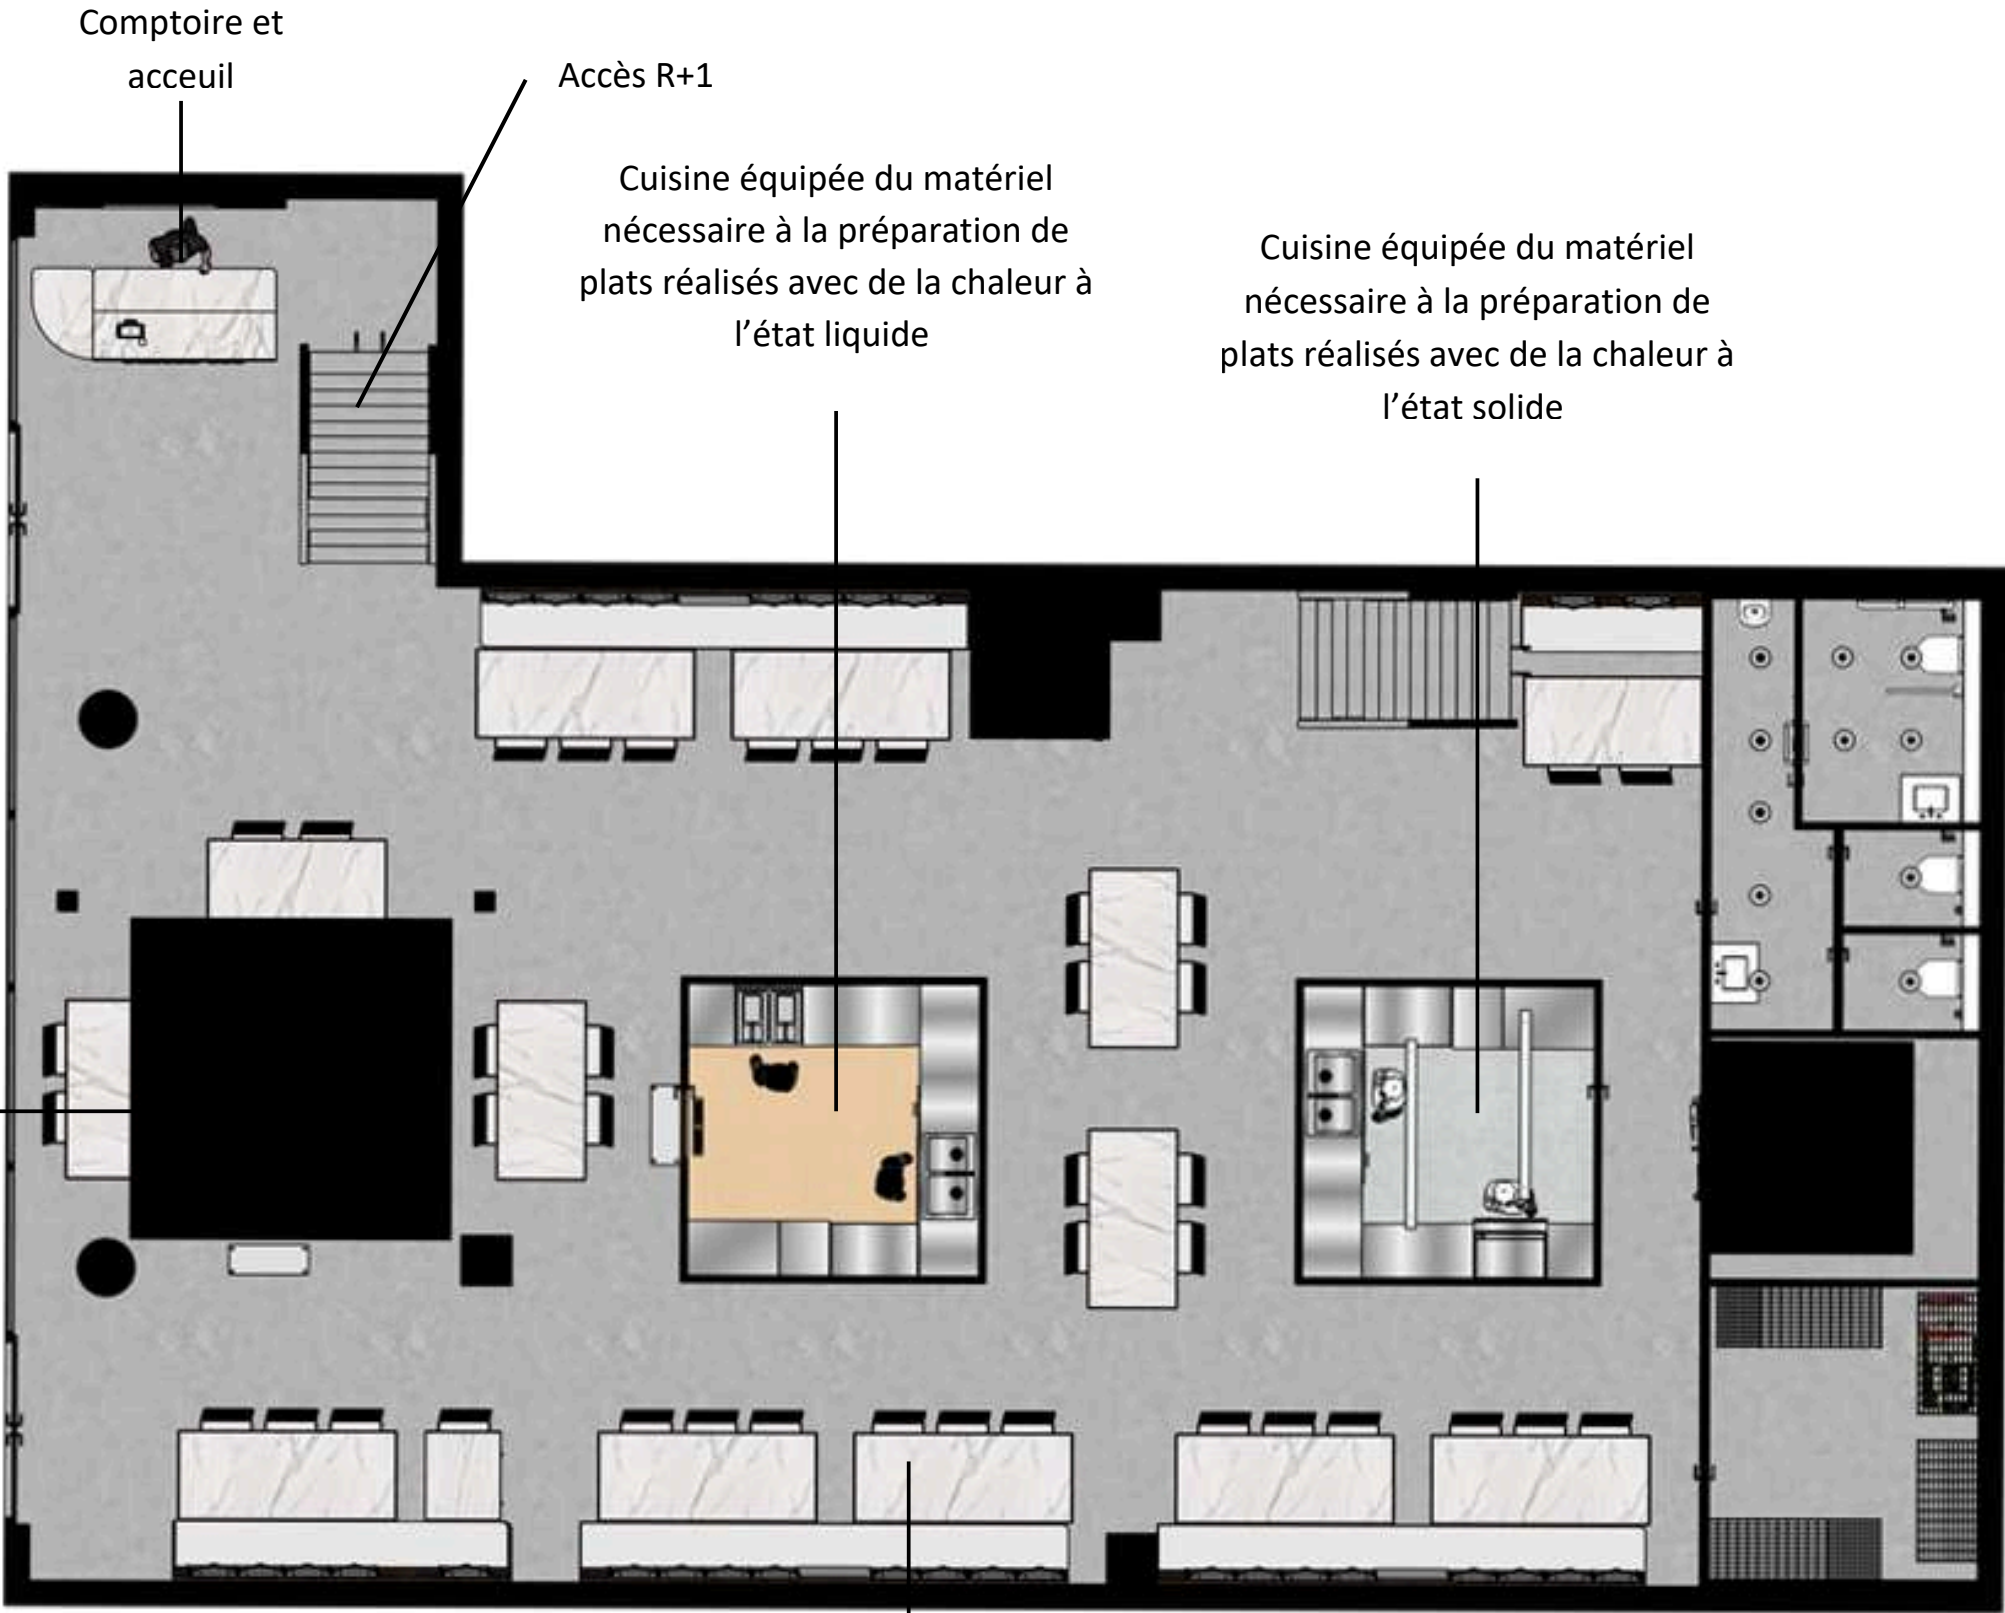

Accès R+1

Cuisine équipée du matériel
nécessaire à la préparation de
plats réalisés avec de la chaleur à
l'état liquide


Cuisine équipée du matériel
nécessaire à la préparation de
plats réalisés avec de la chaleur à
l'état solide

Espace de
dégustation

Ouvrage MATSAV ZOR 25 Terr de l'université,92000 Nanterre	Maitre d'oeuvre Léa Froger		Maitre D'ouvrage Marec Alon / Sahim Mohamed 12 rue Anatole France ,92000 Nanterre	
Titre Plan mis en couleurs RDC	Echelle A3	Format 1/50	Date 30/04/2026	Etat du projet Projeté

Plan

MIS EN COULEURS R+1

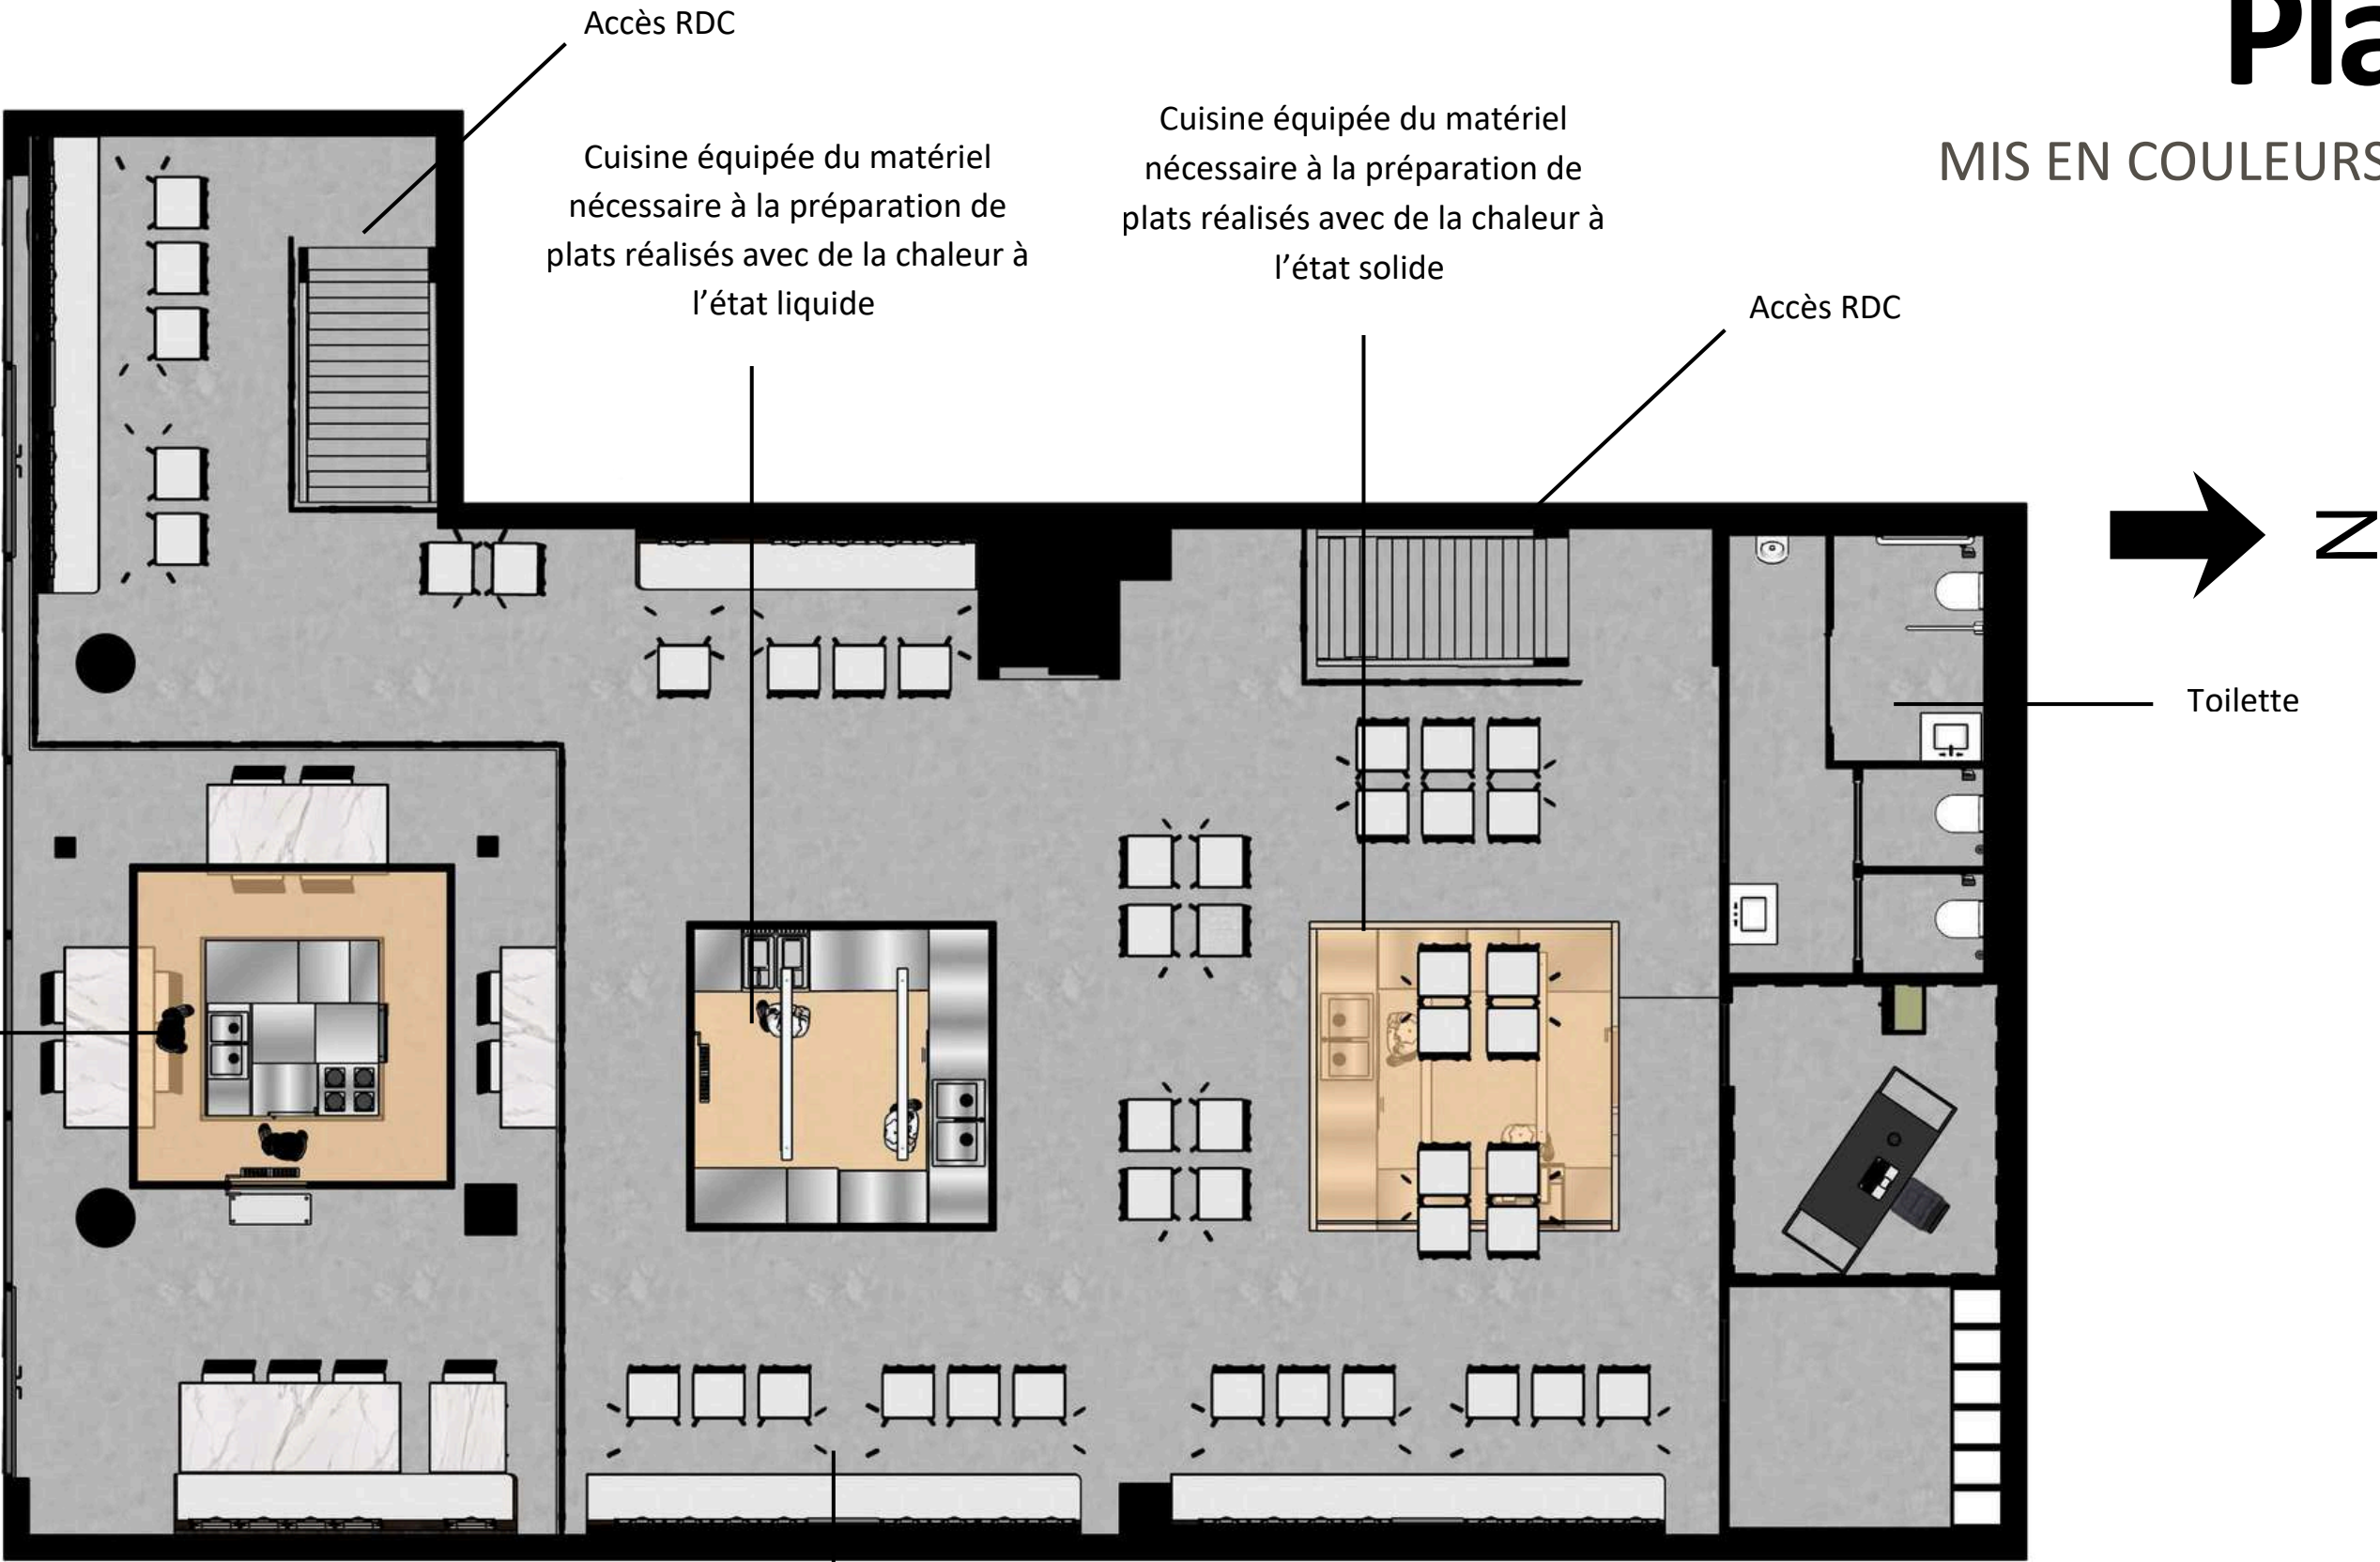

Cuisine équipée du matériel nécessaire à la préparation de plats réalisés avec de la chaleur à l'état gazeux

Cuisine équipée du matériel nécessaire à la préparation de plats réalisés avec de la chaleur à l'état liquide

Cuisine équipée du matériel nécessaire à la préparation de plats réalisés avec de la chaleur à l'état solide

Accès RDC


Toilette

Espace de dégustation

Ouvrage MATSAV ZOR 25 Terr de l'université,92000 Nanterre		Maitre d'oeuvre Léa Froger		Maitre D'ouvrage Marec Alon / Sahim Mohamed 12 rue Anatole France ,92000 Nanterre	
Titre Plan mis en couleurs R+ 1		Echelle A3	Format 1/50	Date 30/04/2026	Etat du projet Projeté

Plan


REVETEMENT MURAUX

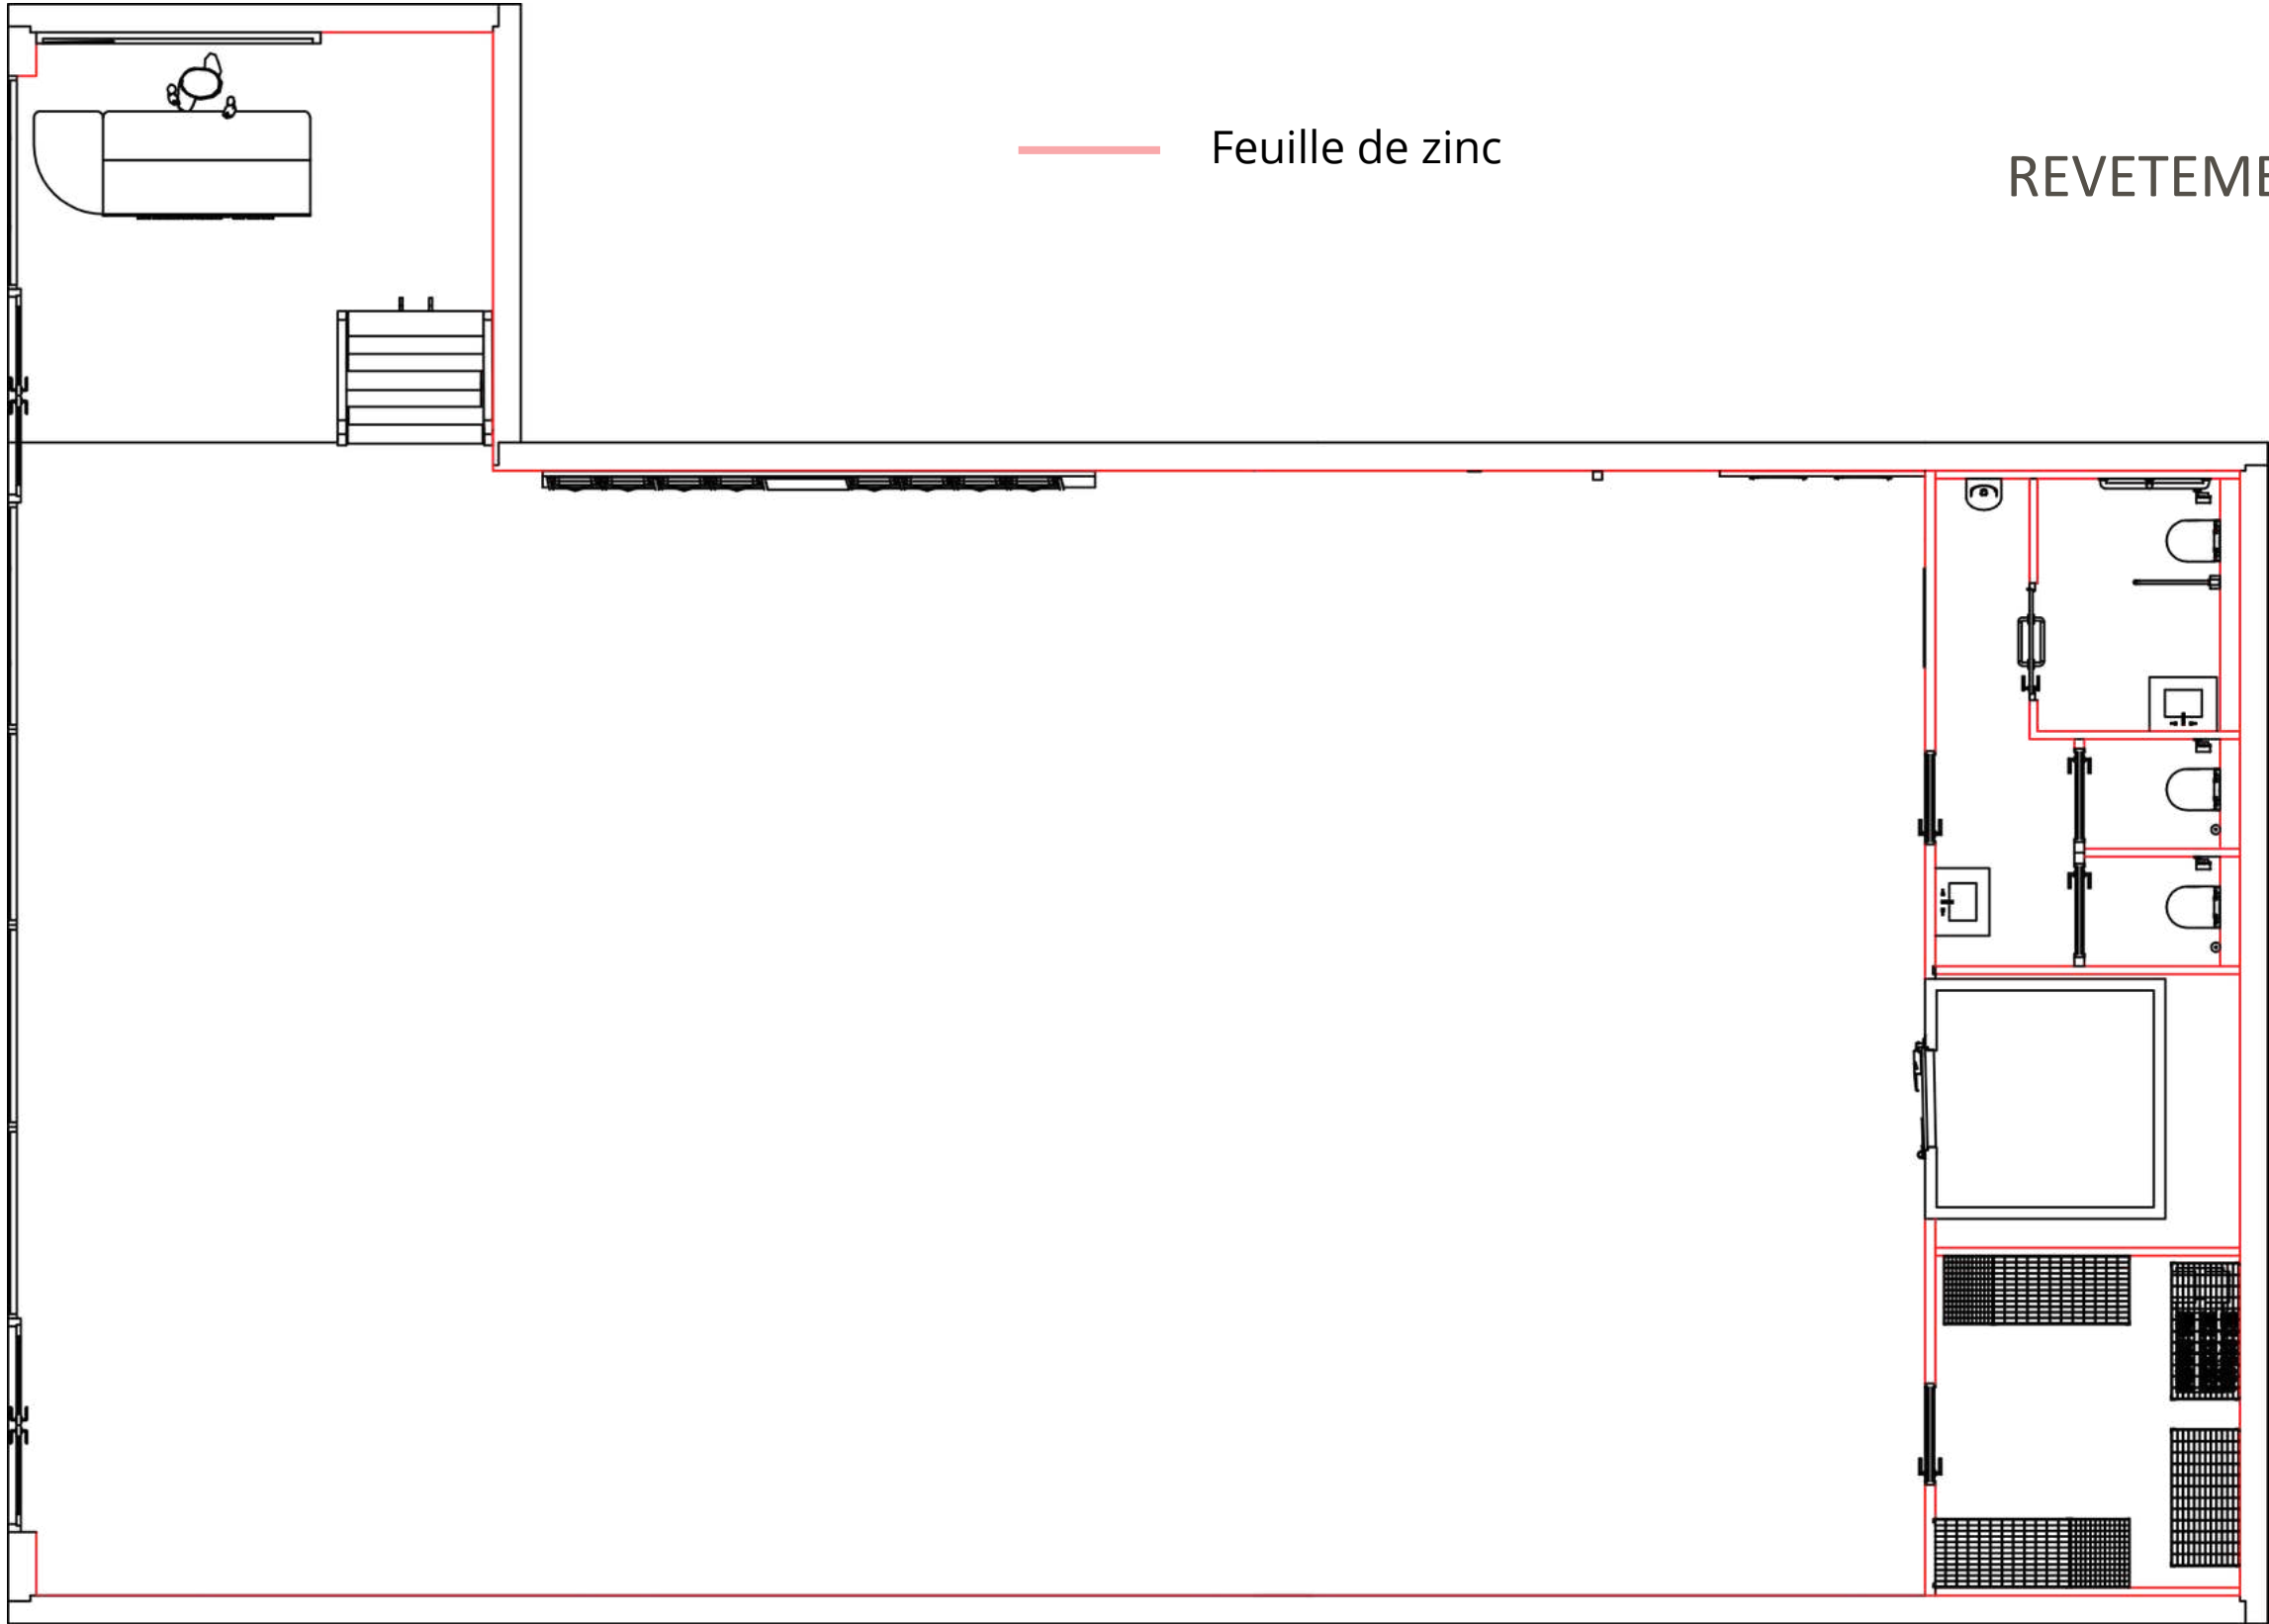

Ouvrage MATSAV ZOR 25 Terr de l'université,92000 Nanterre		Maitre d'oeuvre Léa Froger		Maitre D'ouvrage Marec Alon / Sahim Mohamed 12 rue Anatole France ,92000 Nanterre	
Titre Plan revetement muraux RDC	Echelle A3	Format 1/50	Date 30/04/2026	Etat du projet Projeté	

Plan


REVETEMENT MURAUX R+1

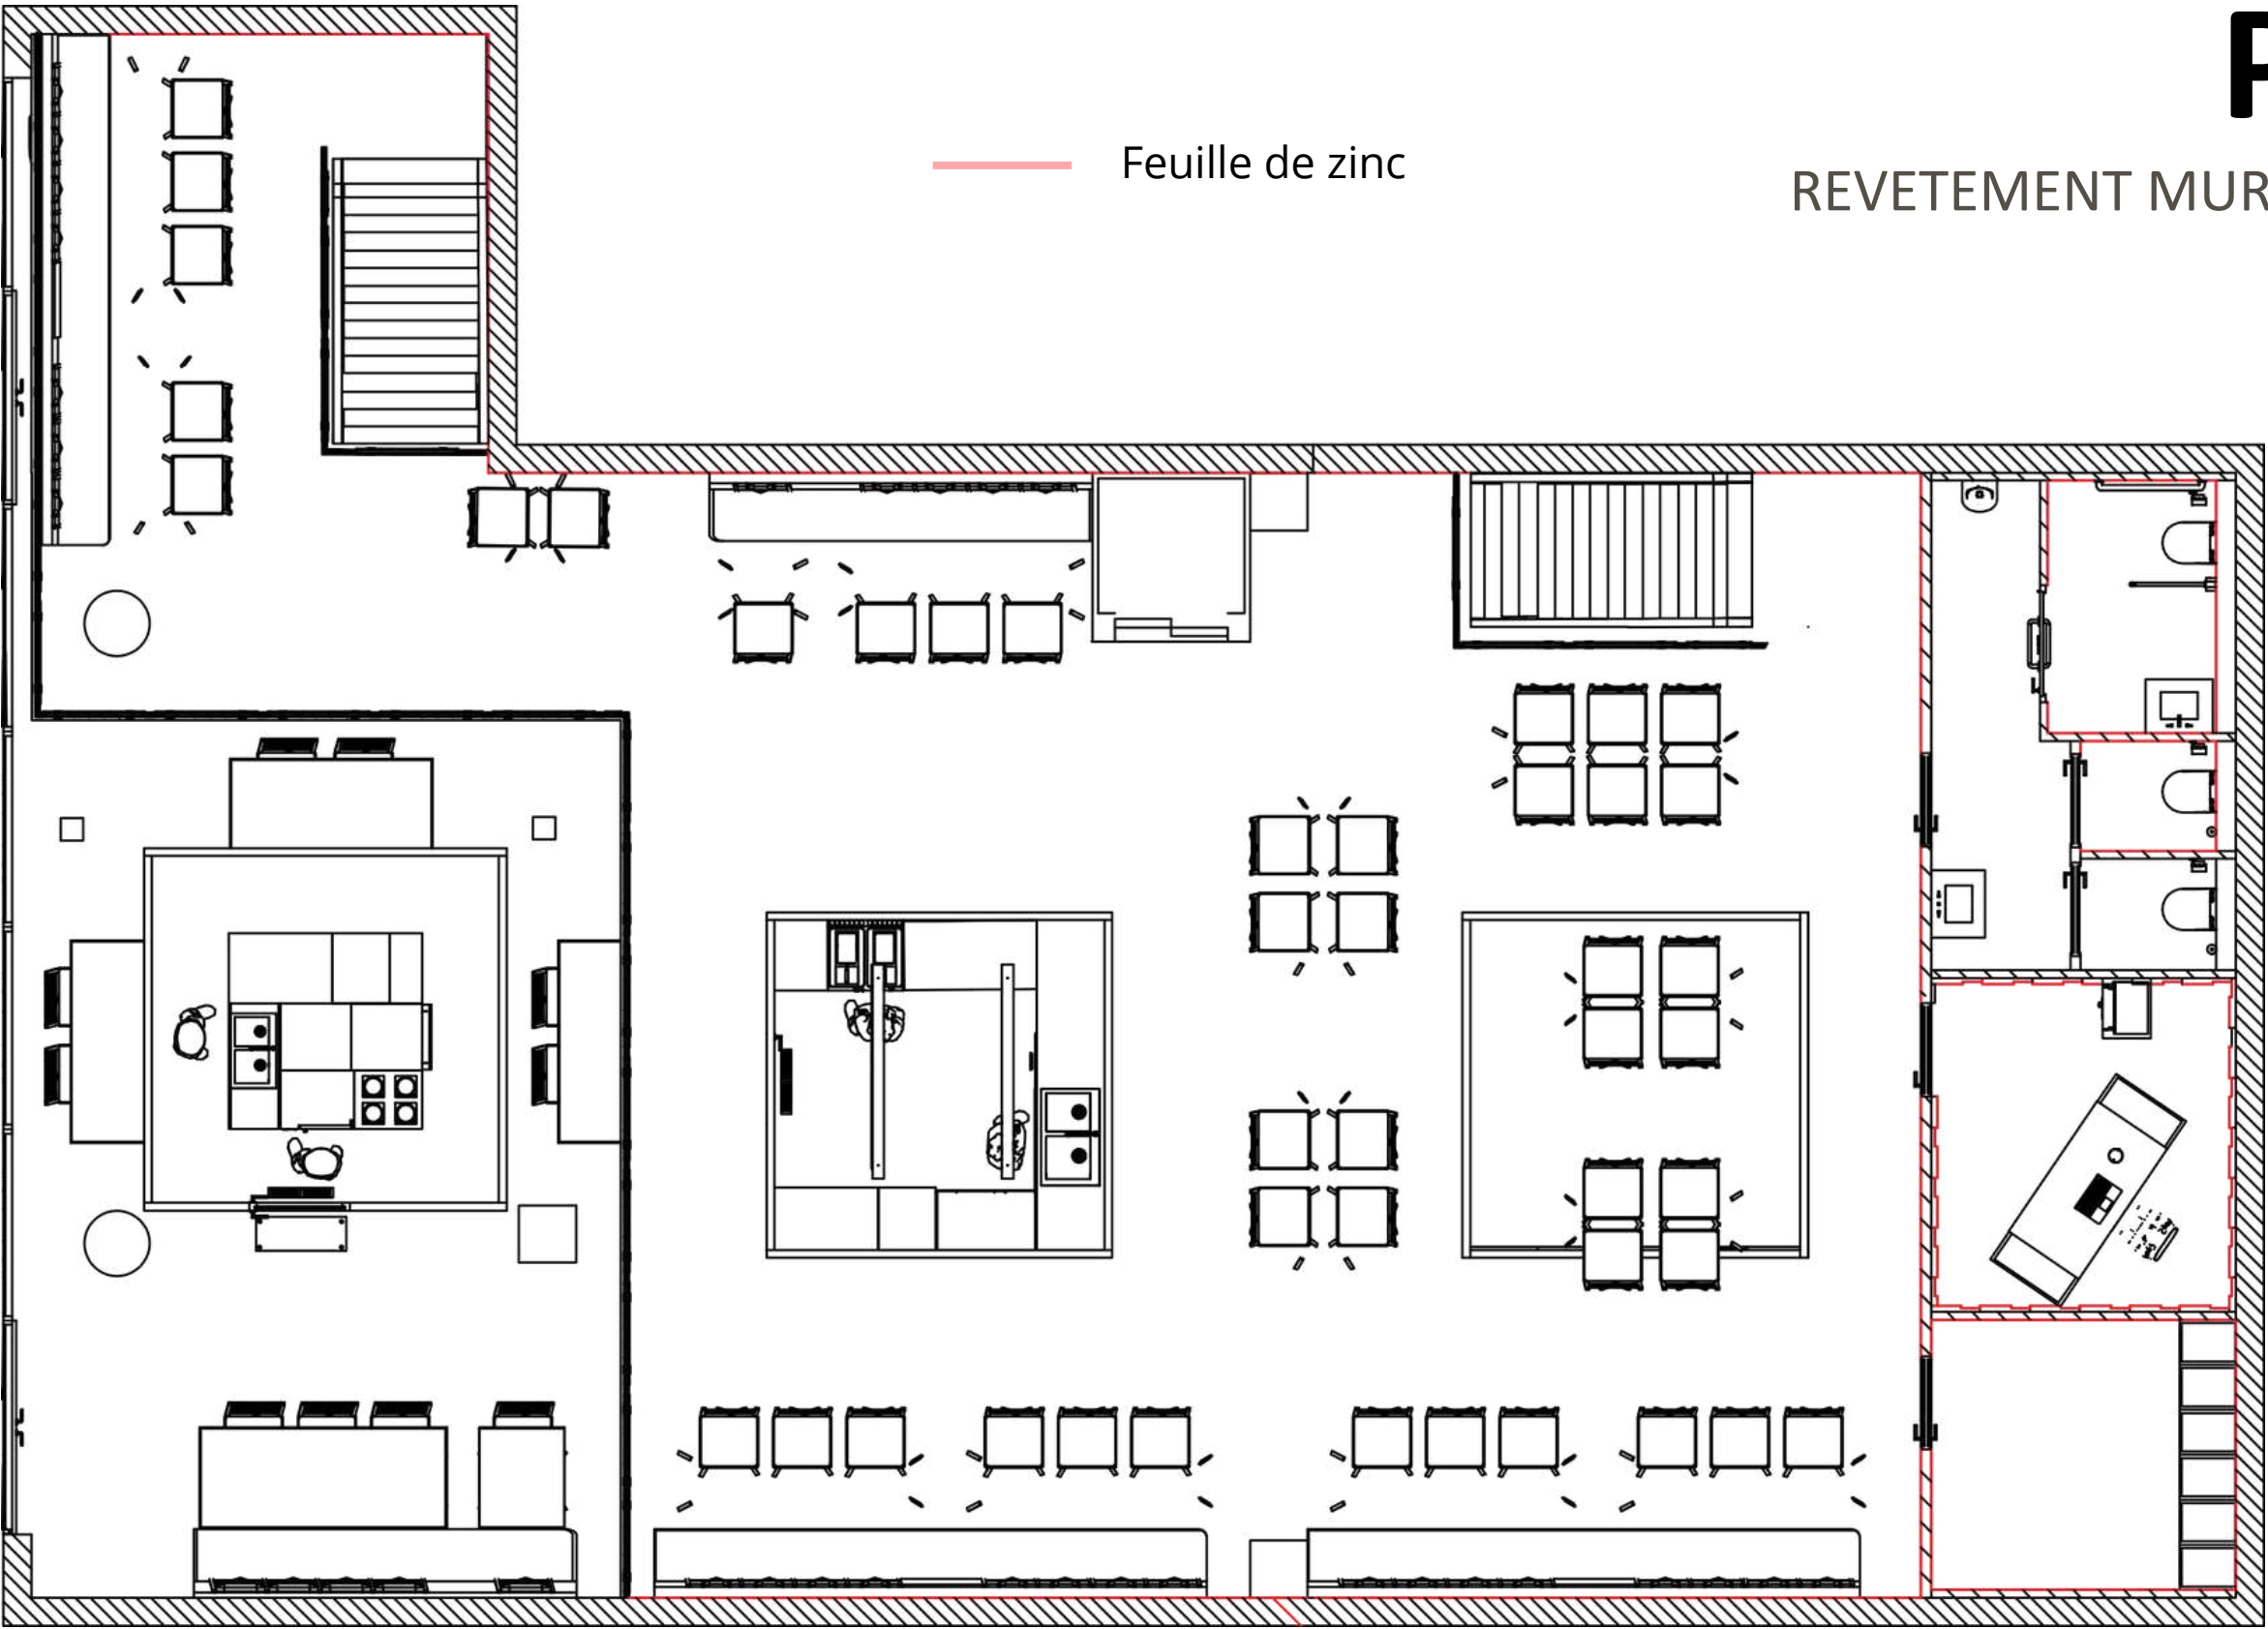

Ouvrage MATSAV ZOR 25 Terr de l'université,92000 Nanterre		Maitre d'oeuvre Léa Froger		Maitre D'ouvrage Marec Alon / Sahim Mohamed 12 rue Anatole France ,92000 Nanterre	
Titre Plan revetement muraux R+1	Echelle A3	Format 1/50	Date 30/04/2026	Etat du projet Projeté	

Plan


SOL RDC

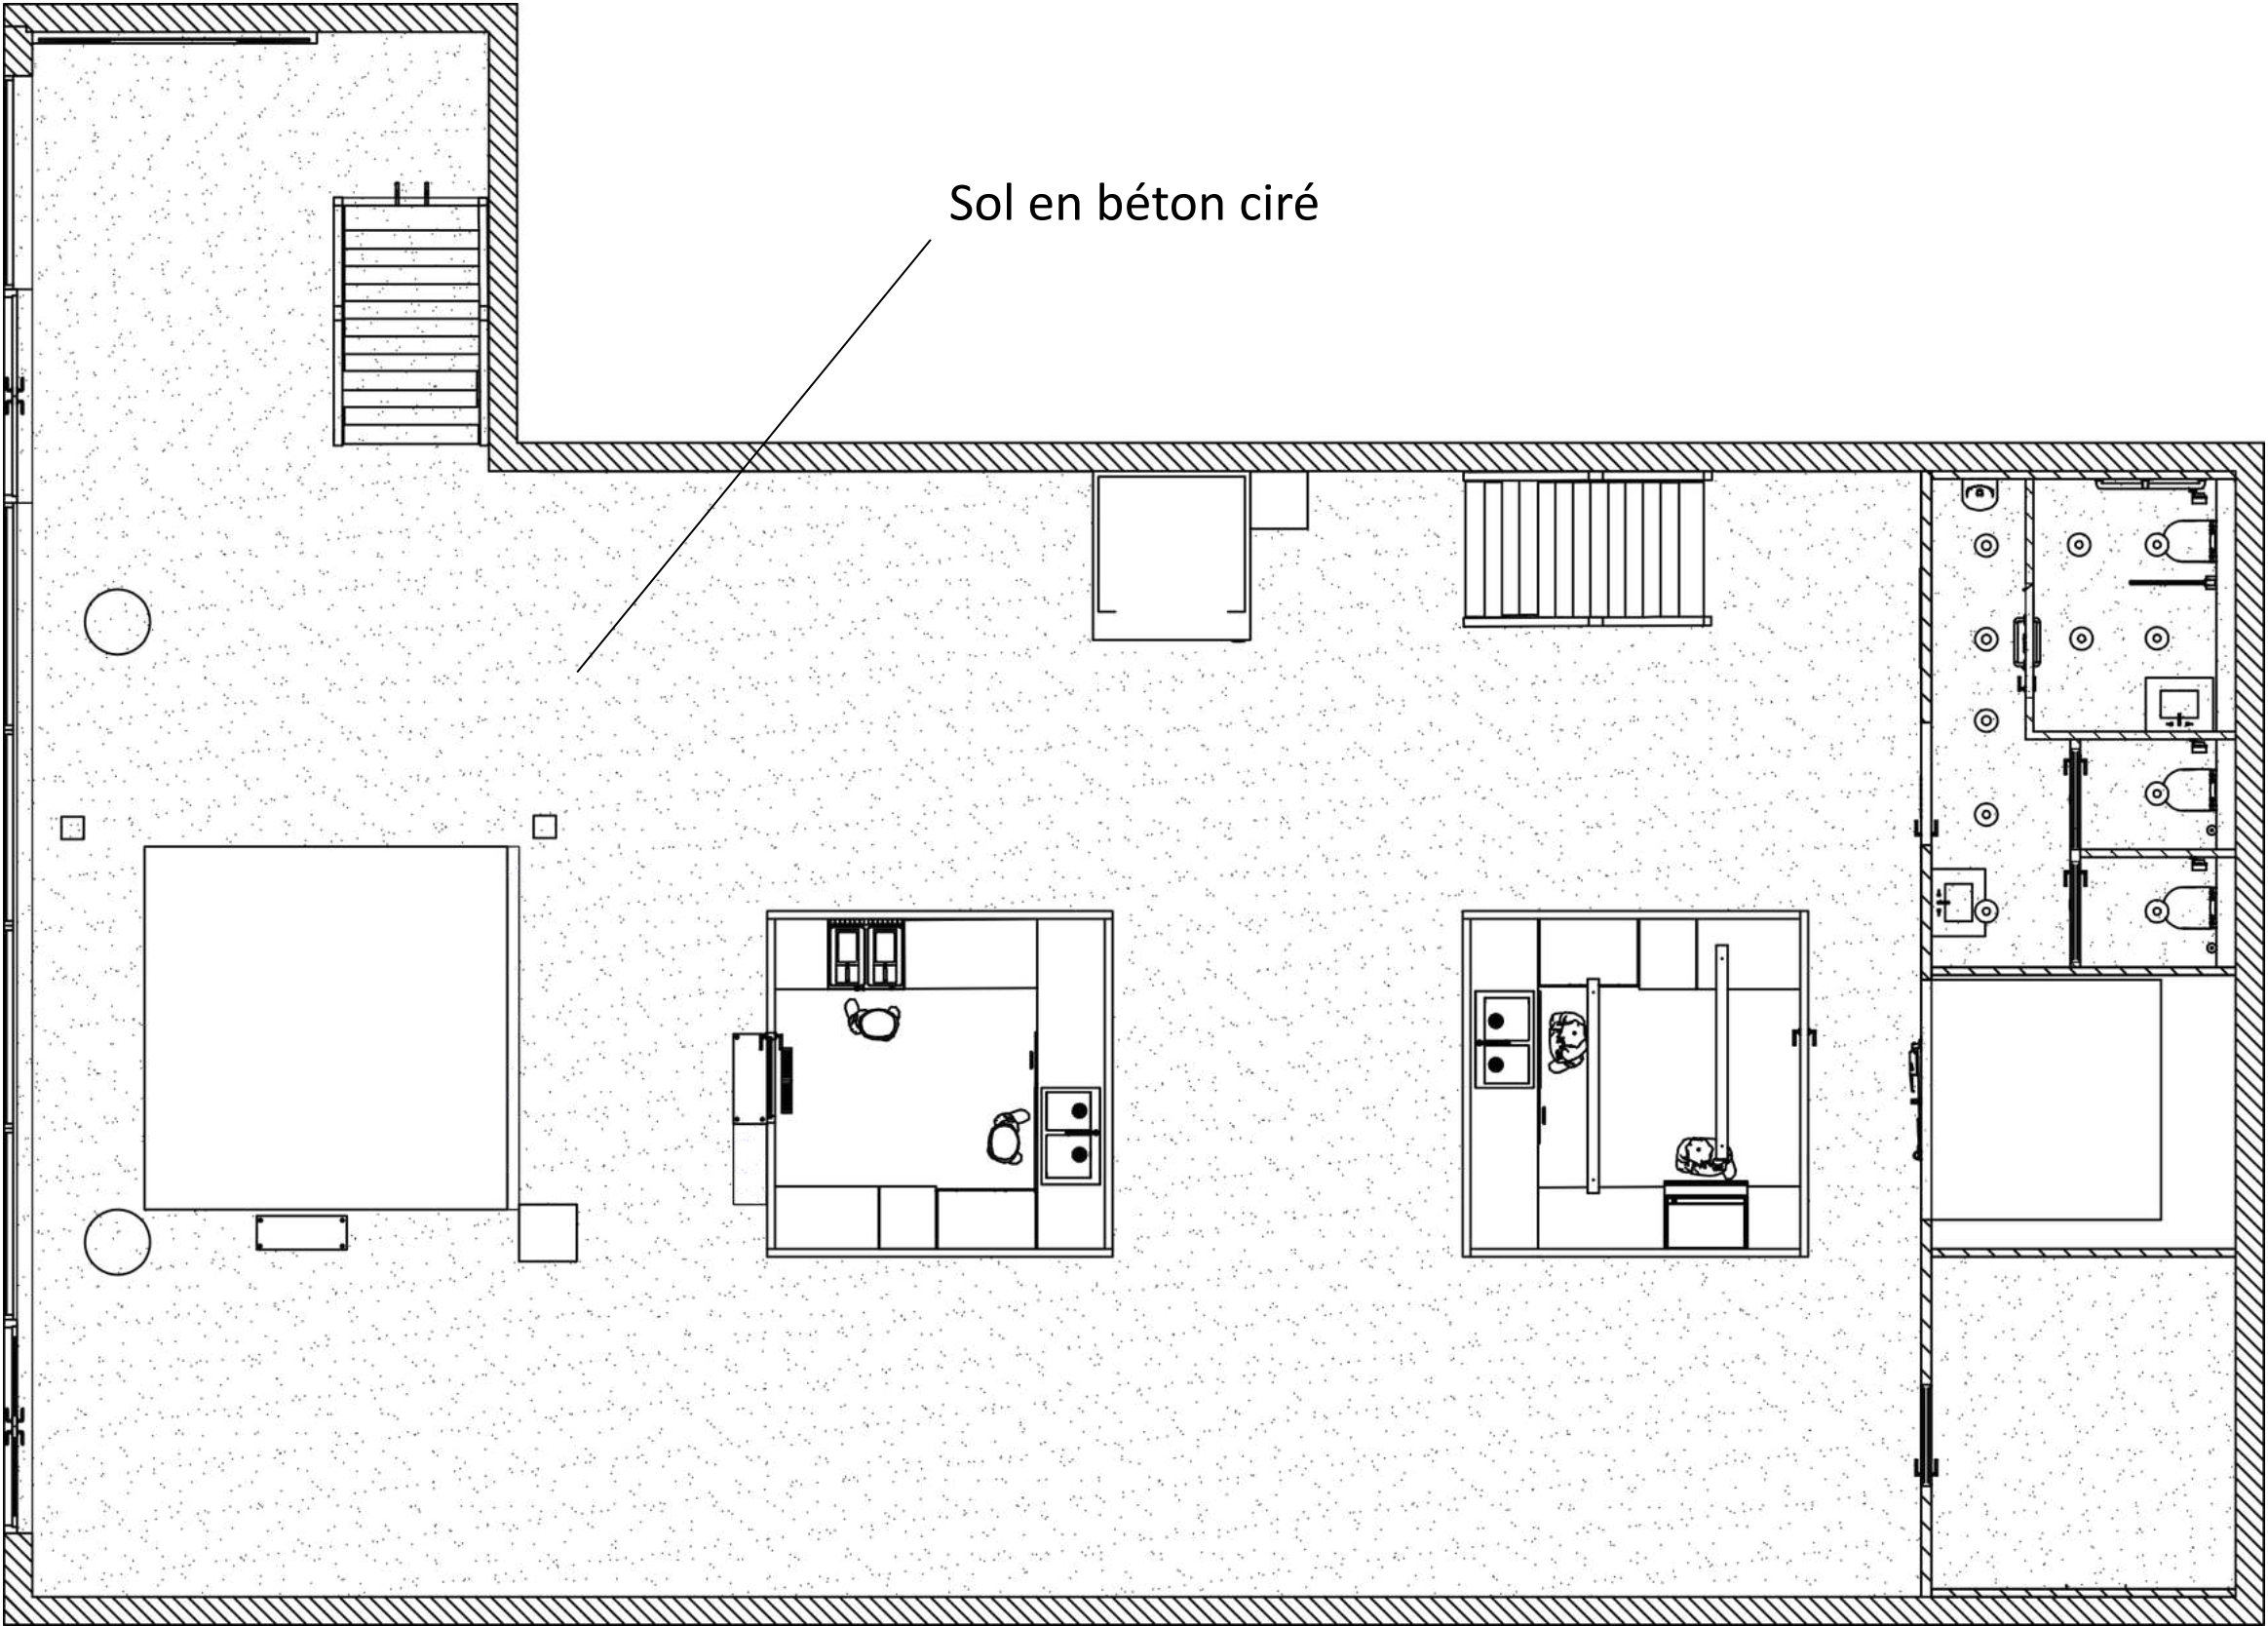

Ouvrage MATSAV ZOR 25 Terr de l'université,92000 Nanterre		Maitre d'oeuvre Léa Froger		Maitre D'ouvrage Marec Alon / Sahim Mohamed 12 rue Anatole France ,92000 Nanterre	
Titre Plan sol RDC		Echelle A3	Format 1/50	Date 30/04/2026	Etat du projet Projeté

Plan

SOL R+1

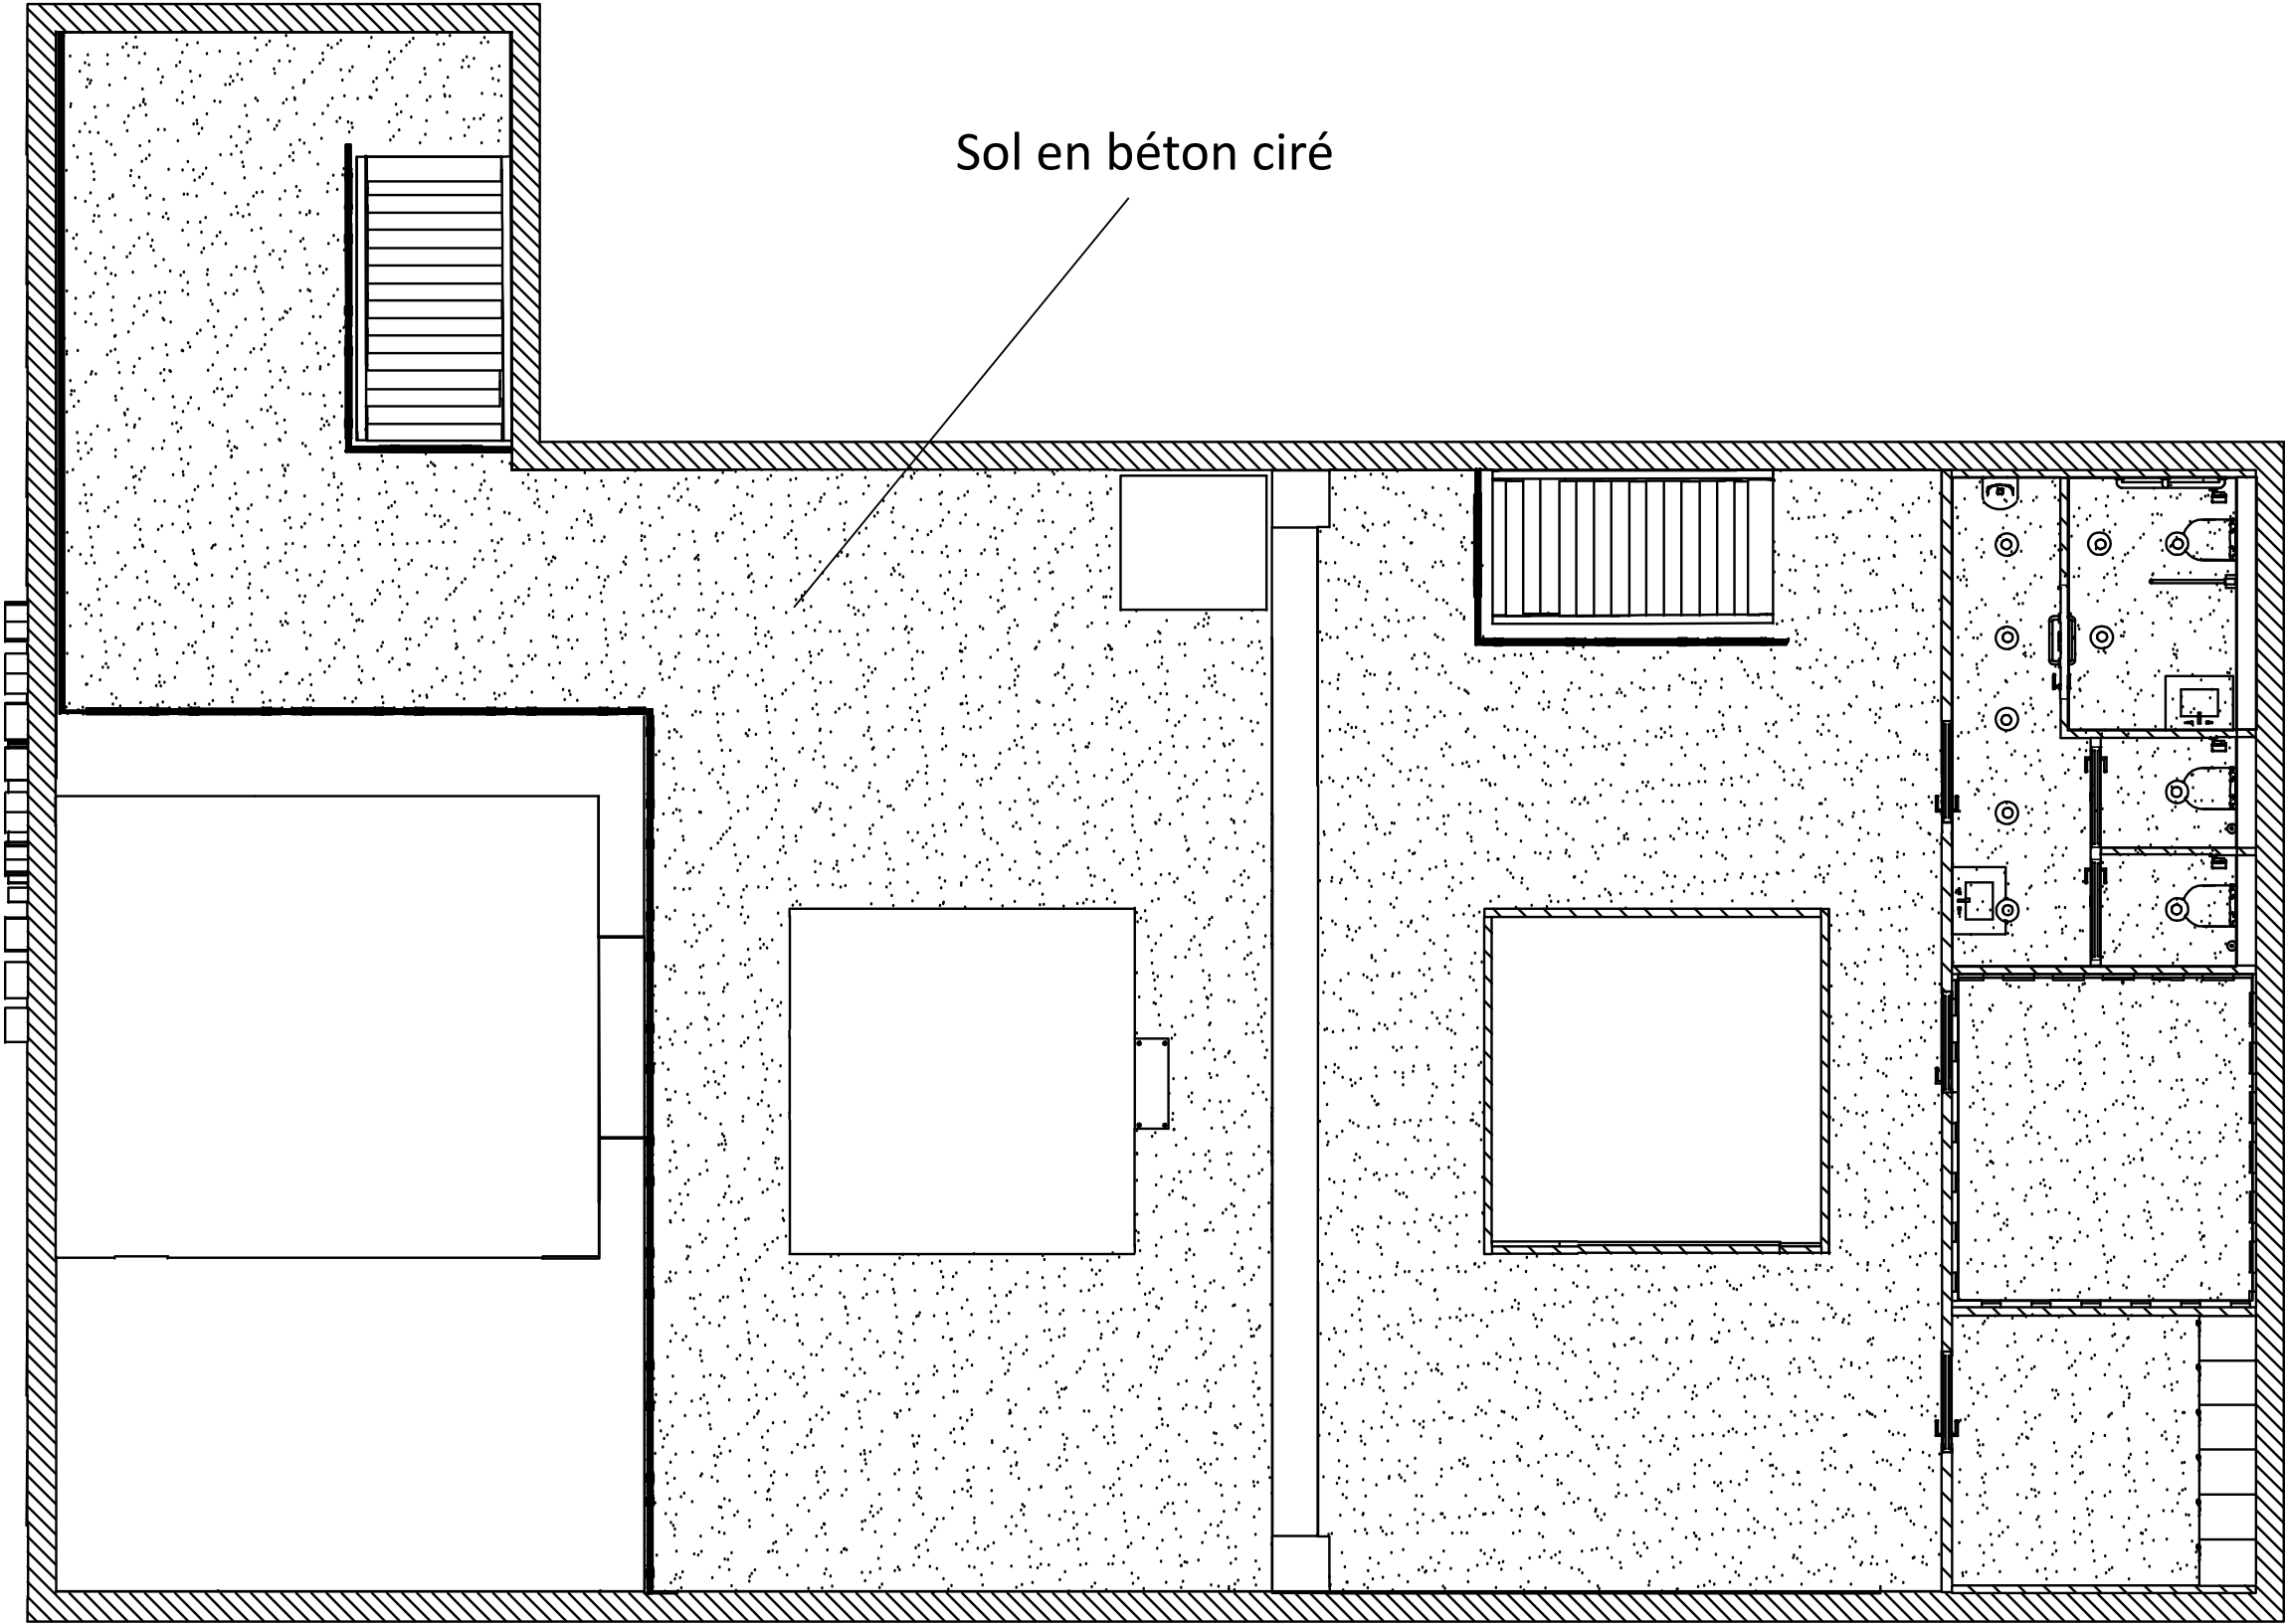

Ouvrage MATSAV ZOR 25 Terr de l'université,92000 Nanterre		Maitre d'oeuvre Léa Froger		Maitre D'ouvrage Marec Alon / Sahim Mohamed 12 rue Anatole France ,92000 Nanterre	
Titre Plan sol R+1		Echelle A3	Format 1/50	Date 30/04/2026	Etat du projet Projeté

Plan

BÉTON CIRÉ, POUR APPORTER DE LA CONTINUITÉ ET RENFORCER L'ASPECT BRUT ET MINÉRAL DE L'ESPACE.



MATÉRIAUX SOL ET MOBILIER RDC

BOIS NOYER, AU NIVEAU DE NOS CHAISES, POUR APPORTER DE LA CHALEUR ET CRÉER UN ÉQUILIBRE AVEC LES MATÉRIAUX PLUS FROIDS.




MARBRE BLANC VEINÉ GRIS, POUR APPORTER DE L'ÉLÉGANCE ET CRÉER UN CONTRASTE AVEC LA CHALEUR DU CONCEPT.



TEXTILE GRIS, AU NIVEAU DE NOS ASSISES, POUR APPORTER DU CONFORT ET ADOUCIR L'AMBIANCE GÉNÉRALE



VERRE ORANGE, POUR APPORTER DE LA TRANSPARENCE ET POUR FAVORISER L'IMMERSION

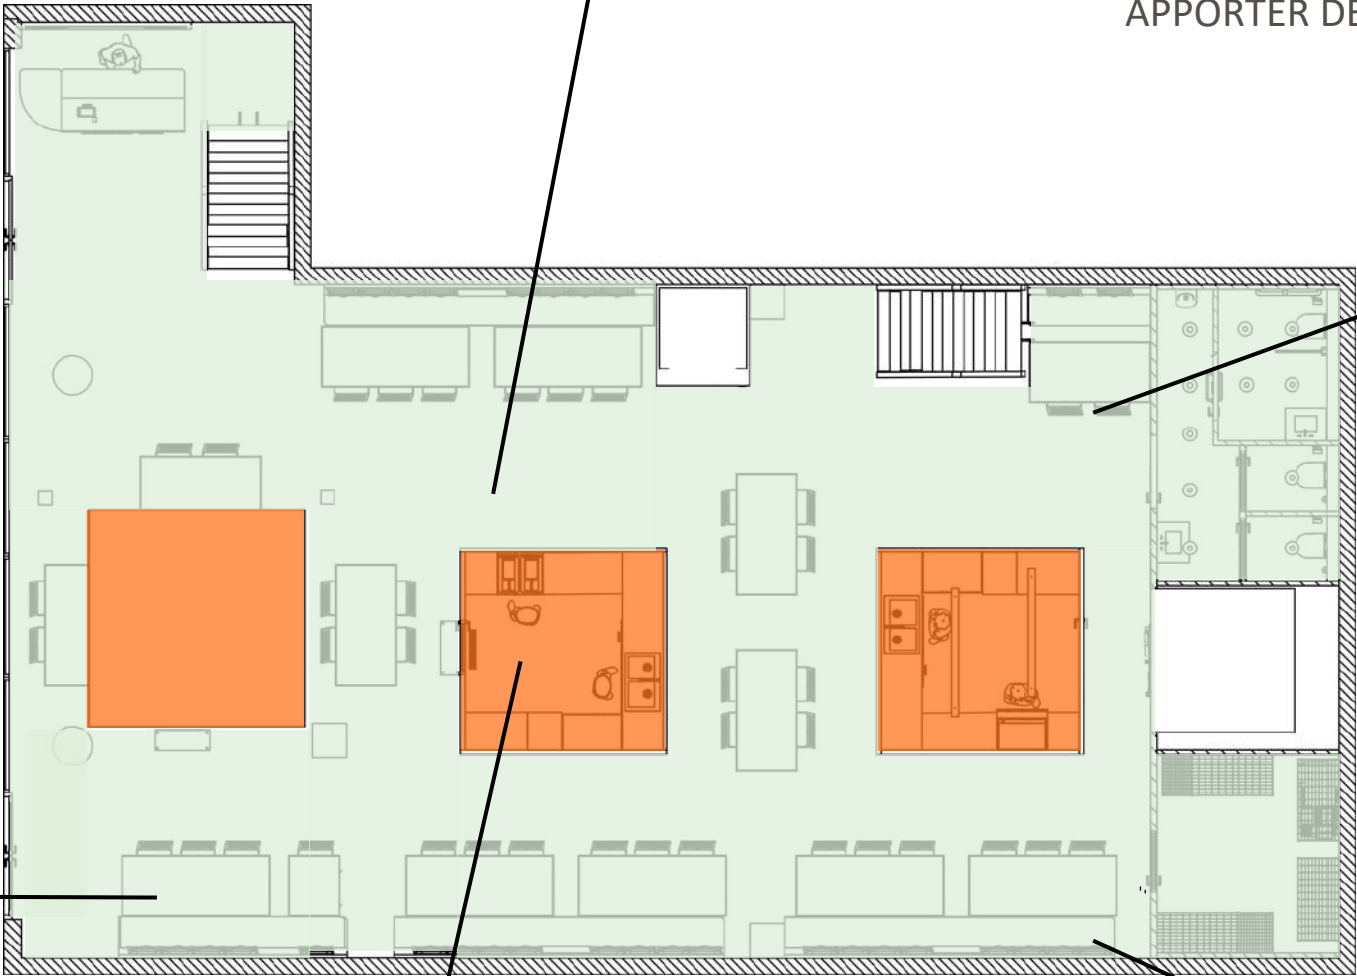

Ouvrage MATSAV ZOR 25 Terr de l'université,92000 Nanterre		Maitre d'oeuvre Léa Froger		Maitre D'ouvrage Marec Alon / Sahim Mohamed 12 rue Anatole France ,92000 Nanterre	
Titre Plan Matériaux sol et mobilier RDC	Echelle A3	Format 1/50	Date 30/04/2026	Etat du projet Projeté	

Plan

MATÉRIAUX SOL ET MOBILIER R+1

BÉTON CIRÉ, POUR APPORTER DE LA CONTINUITÉ ET RENFORCER L'ASPECT BRUT ET MINÉRAL DE L'ESPACE.



BOIS NOYER, AU NIVEAU DE NOS CHAISES, POUR APPORTER DE LA CHALEUR ET CRÉER UN ÉQUILIBRE AVEC LES MATÉRIAUX PLUS FROIDS.




MARBRE BLANC VEINÉ GRIS, POUR APPORTER DE L'ÉLÉGANCE ET CRÉER UN CONTRASTE AVEC LA CHALEUR DU CONCEPT.



TEXTILE GRIS, AU NIVEAU DE NOS ASSISES, POUR APPORTER DU CONFORT ET ADOUCIR L'AMBIANCE GÉNÉRALE



VERRE ORANGE, POUR APPORTER DE LA TRANSPARENCE ET POUR FAVORISER L'IMMERSION

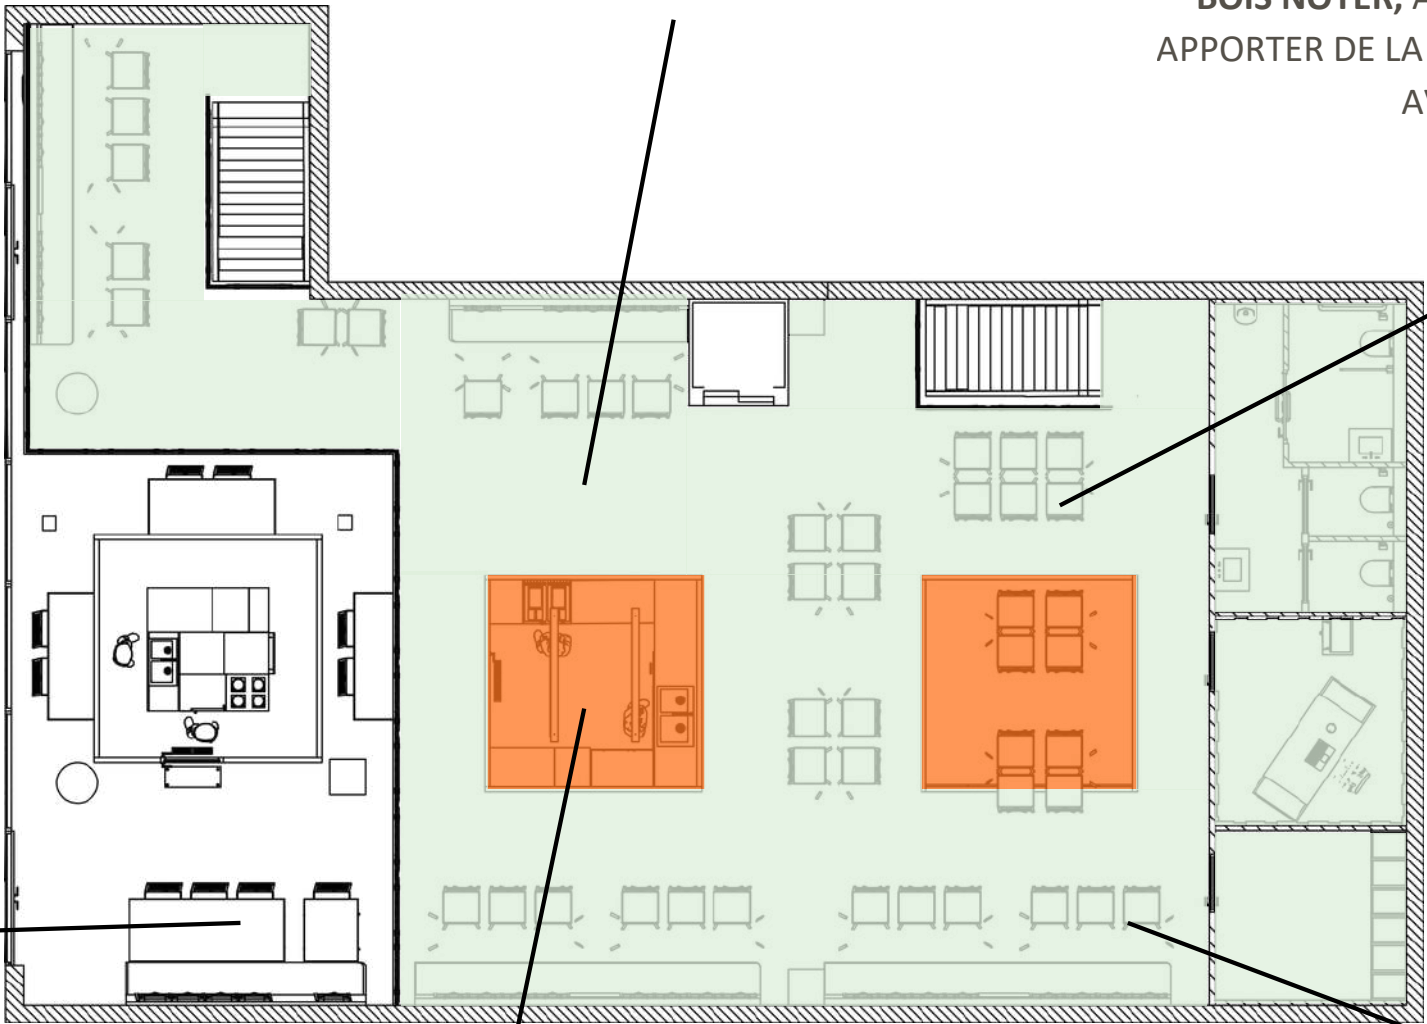

Ouvrage
MATSAV ZOR
25 Terr de l'université,92000 Nanterre

Maitre d'oeuvre
Léa Froger

Maitre D'ouvrage
Marec Alon / Sahim Mohamed
12 rue Anatole France ,92000 Nanterre

Titre
Plan Matériaux sol et mobilier R+1

Echelle
A3


Format
1/50

Date
30/04/2026

Etat du projet
Projeté

Plan

ELÉCTRIQUE RDC

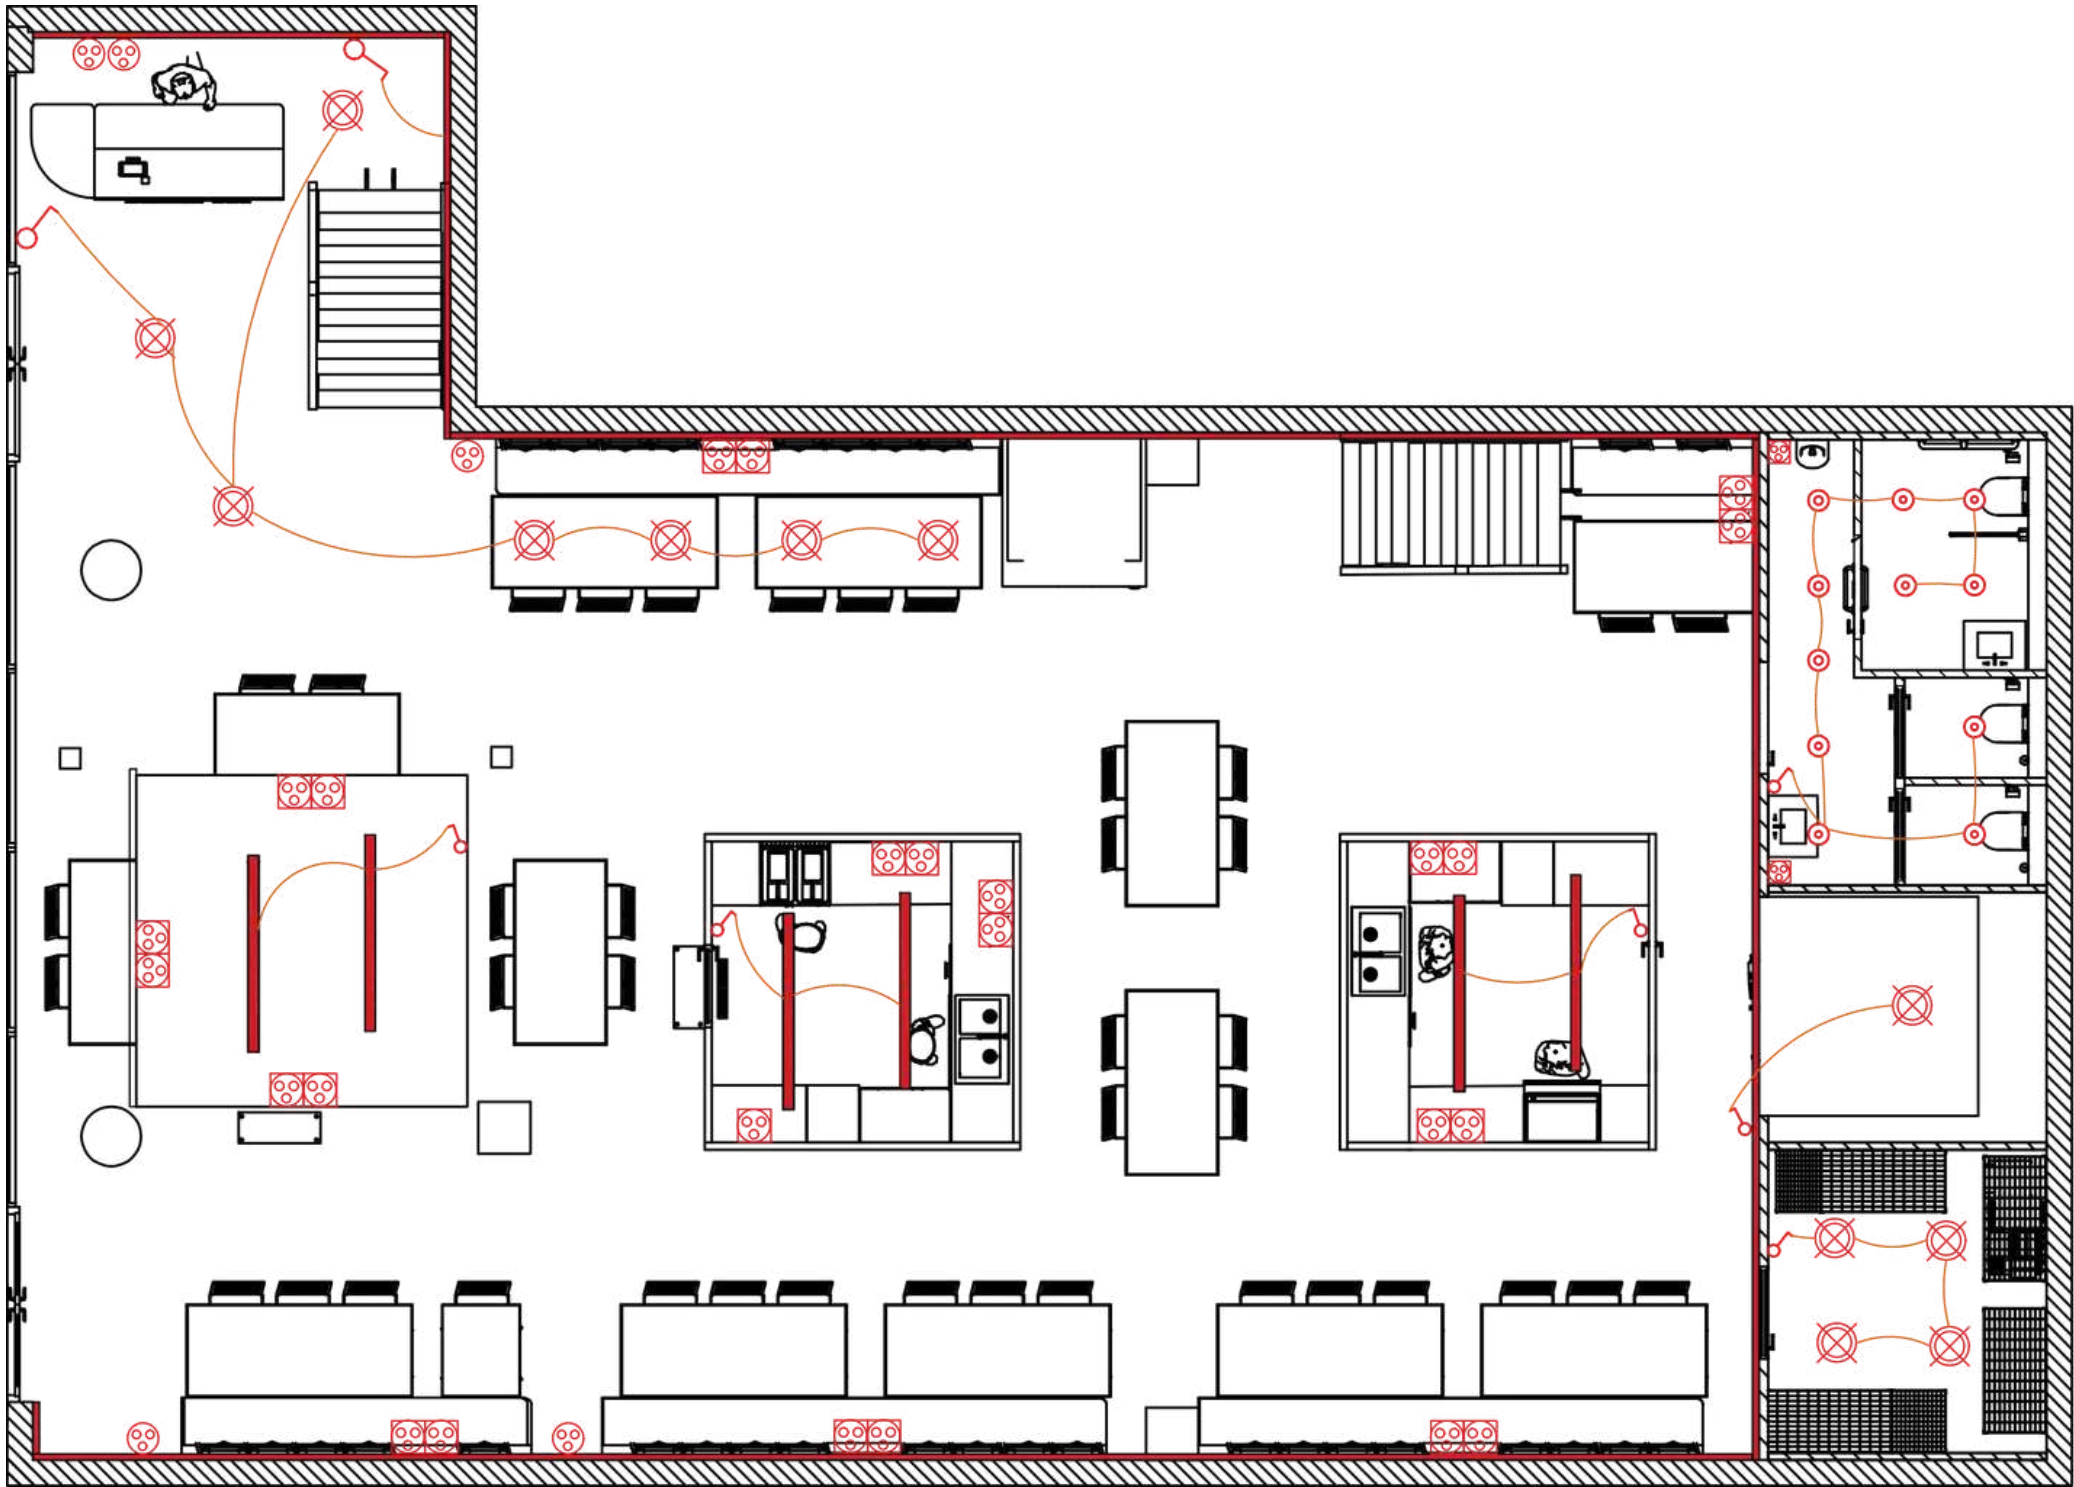


- TE Tableau électrique
- Bande LED
- Spot encastrée
- Interrupteur
- prise simple
- Prise haute
- Spot

Ouvrage MATSAV ZOR 25 Terr de l'université,92000 Nanterre	Maitre d'oeuvre Léa Froger		Maitre D'ouvrage Marec Alon / Sahim Mohamed 12 rue Anatole France ,92000 Nanterre	
Titre Plan electrique RDC	Echelle A3	Format 1/50	Date 30/04/2026	Etat du projet Projeté

Plan

ELÉCTRIQUE R+1

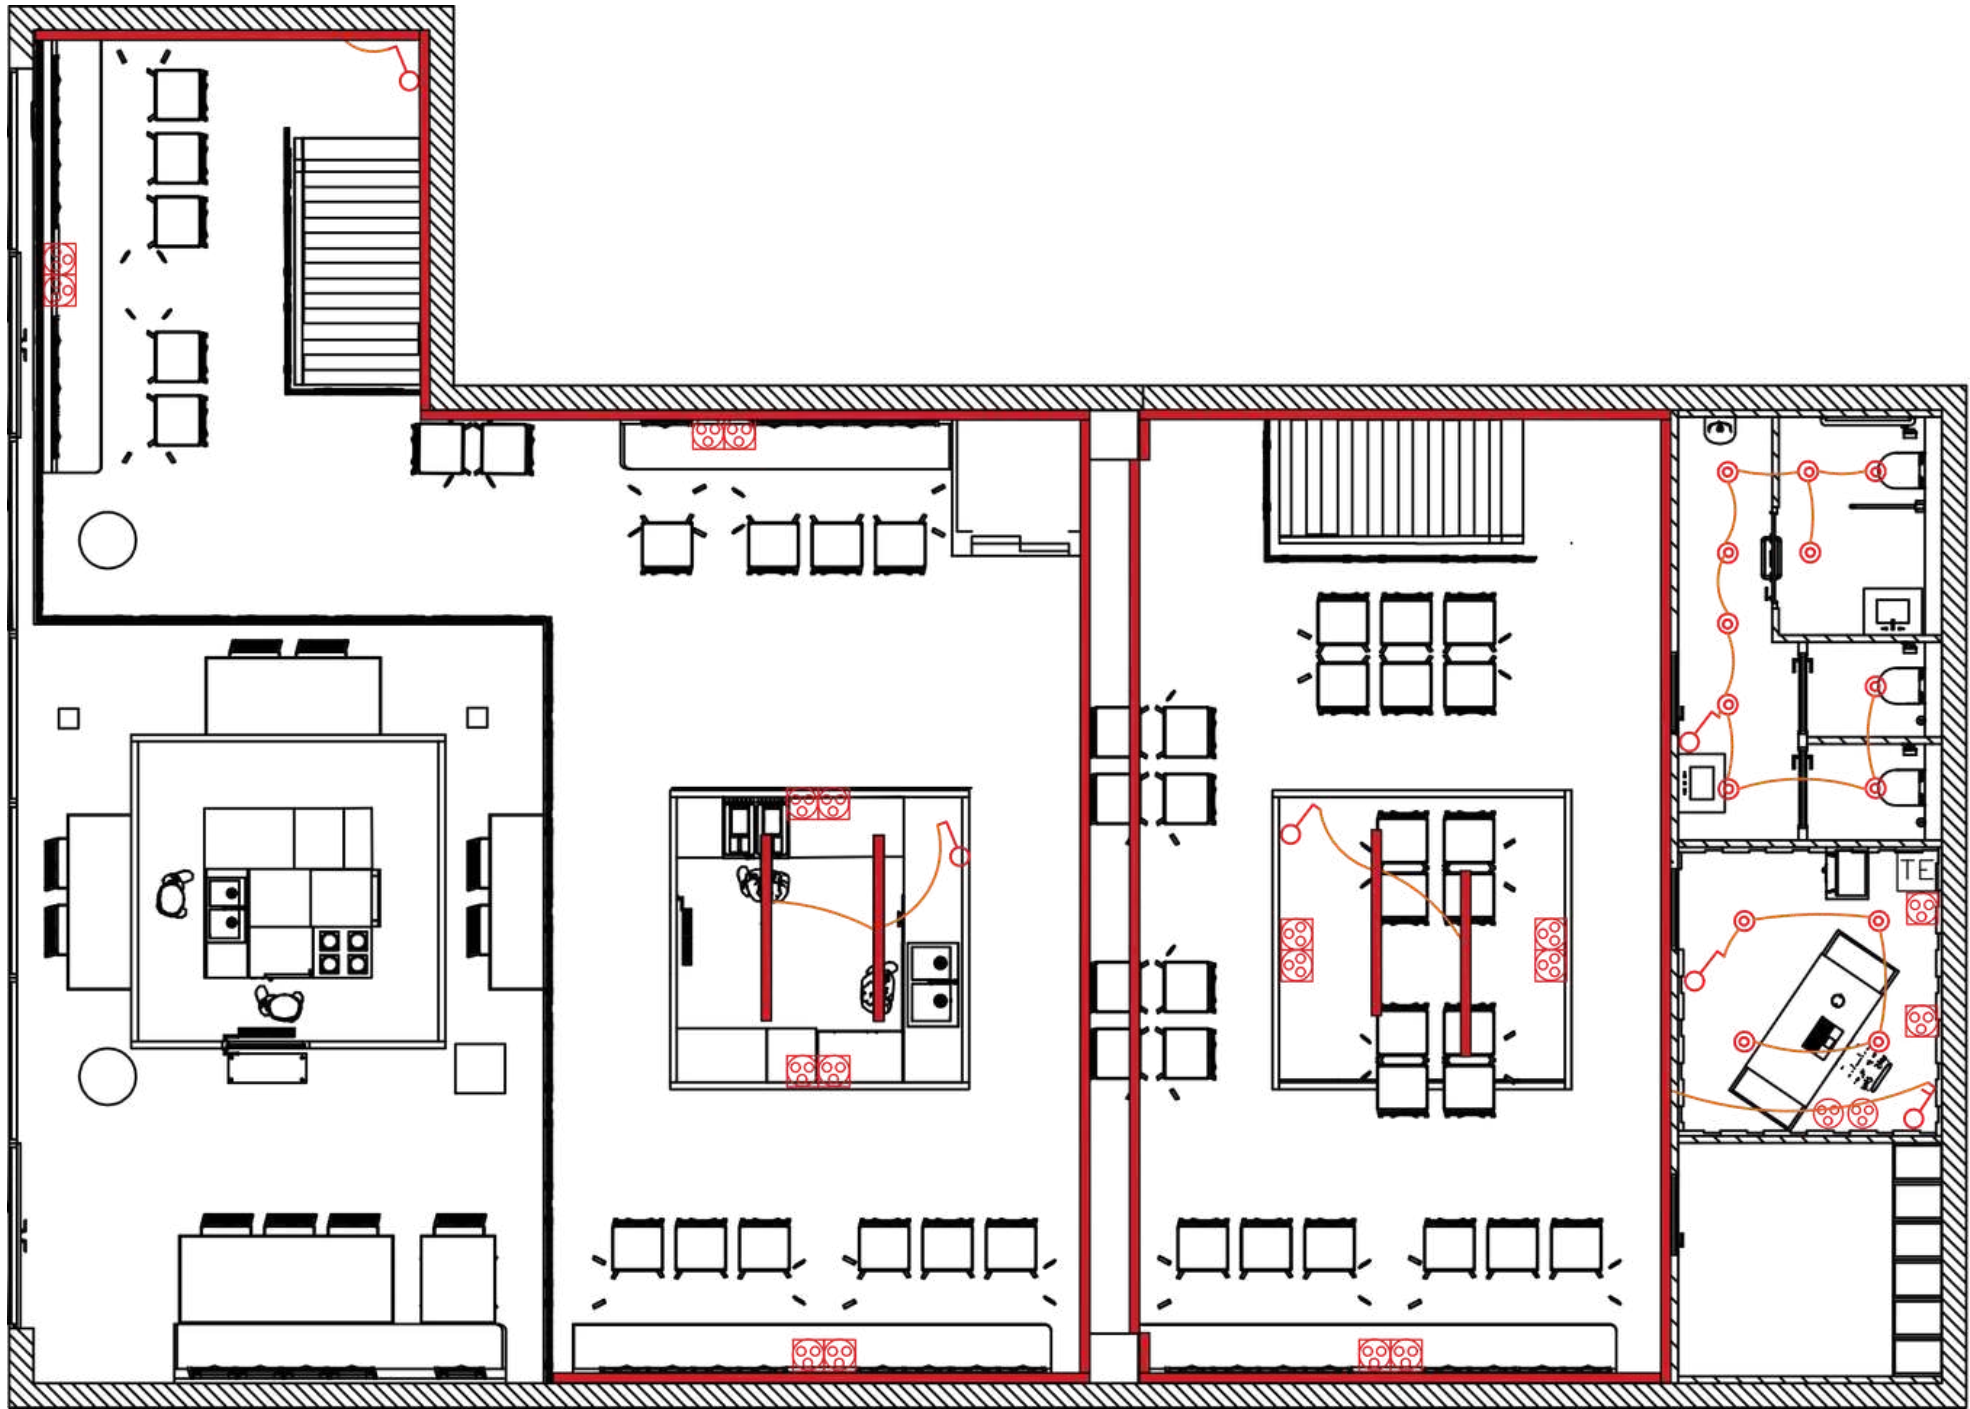


- TE Tableau électrique
- Bande LED
- Spot encastrée
- Interrupteur
- prise simple
- Prise haute
- Spot

Ouvrage MATSAV ZOR 25 Terr de l'université,92000 Nanterre		Maitre d'oeuvre Léa Froger		Maitre D'ouvrage Marec Alon / Sahim Mohamed 12 rue Anatole France ,92000 Nanterre	
Titre Plan électrique R+1		Echelle A3	Format 1/50	Date 30/04/2026	Etat du projet Projeté

Plan


PLAFOND RDC

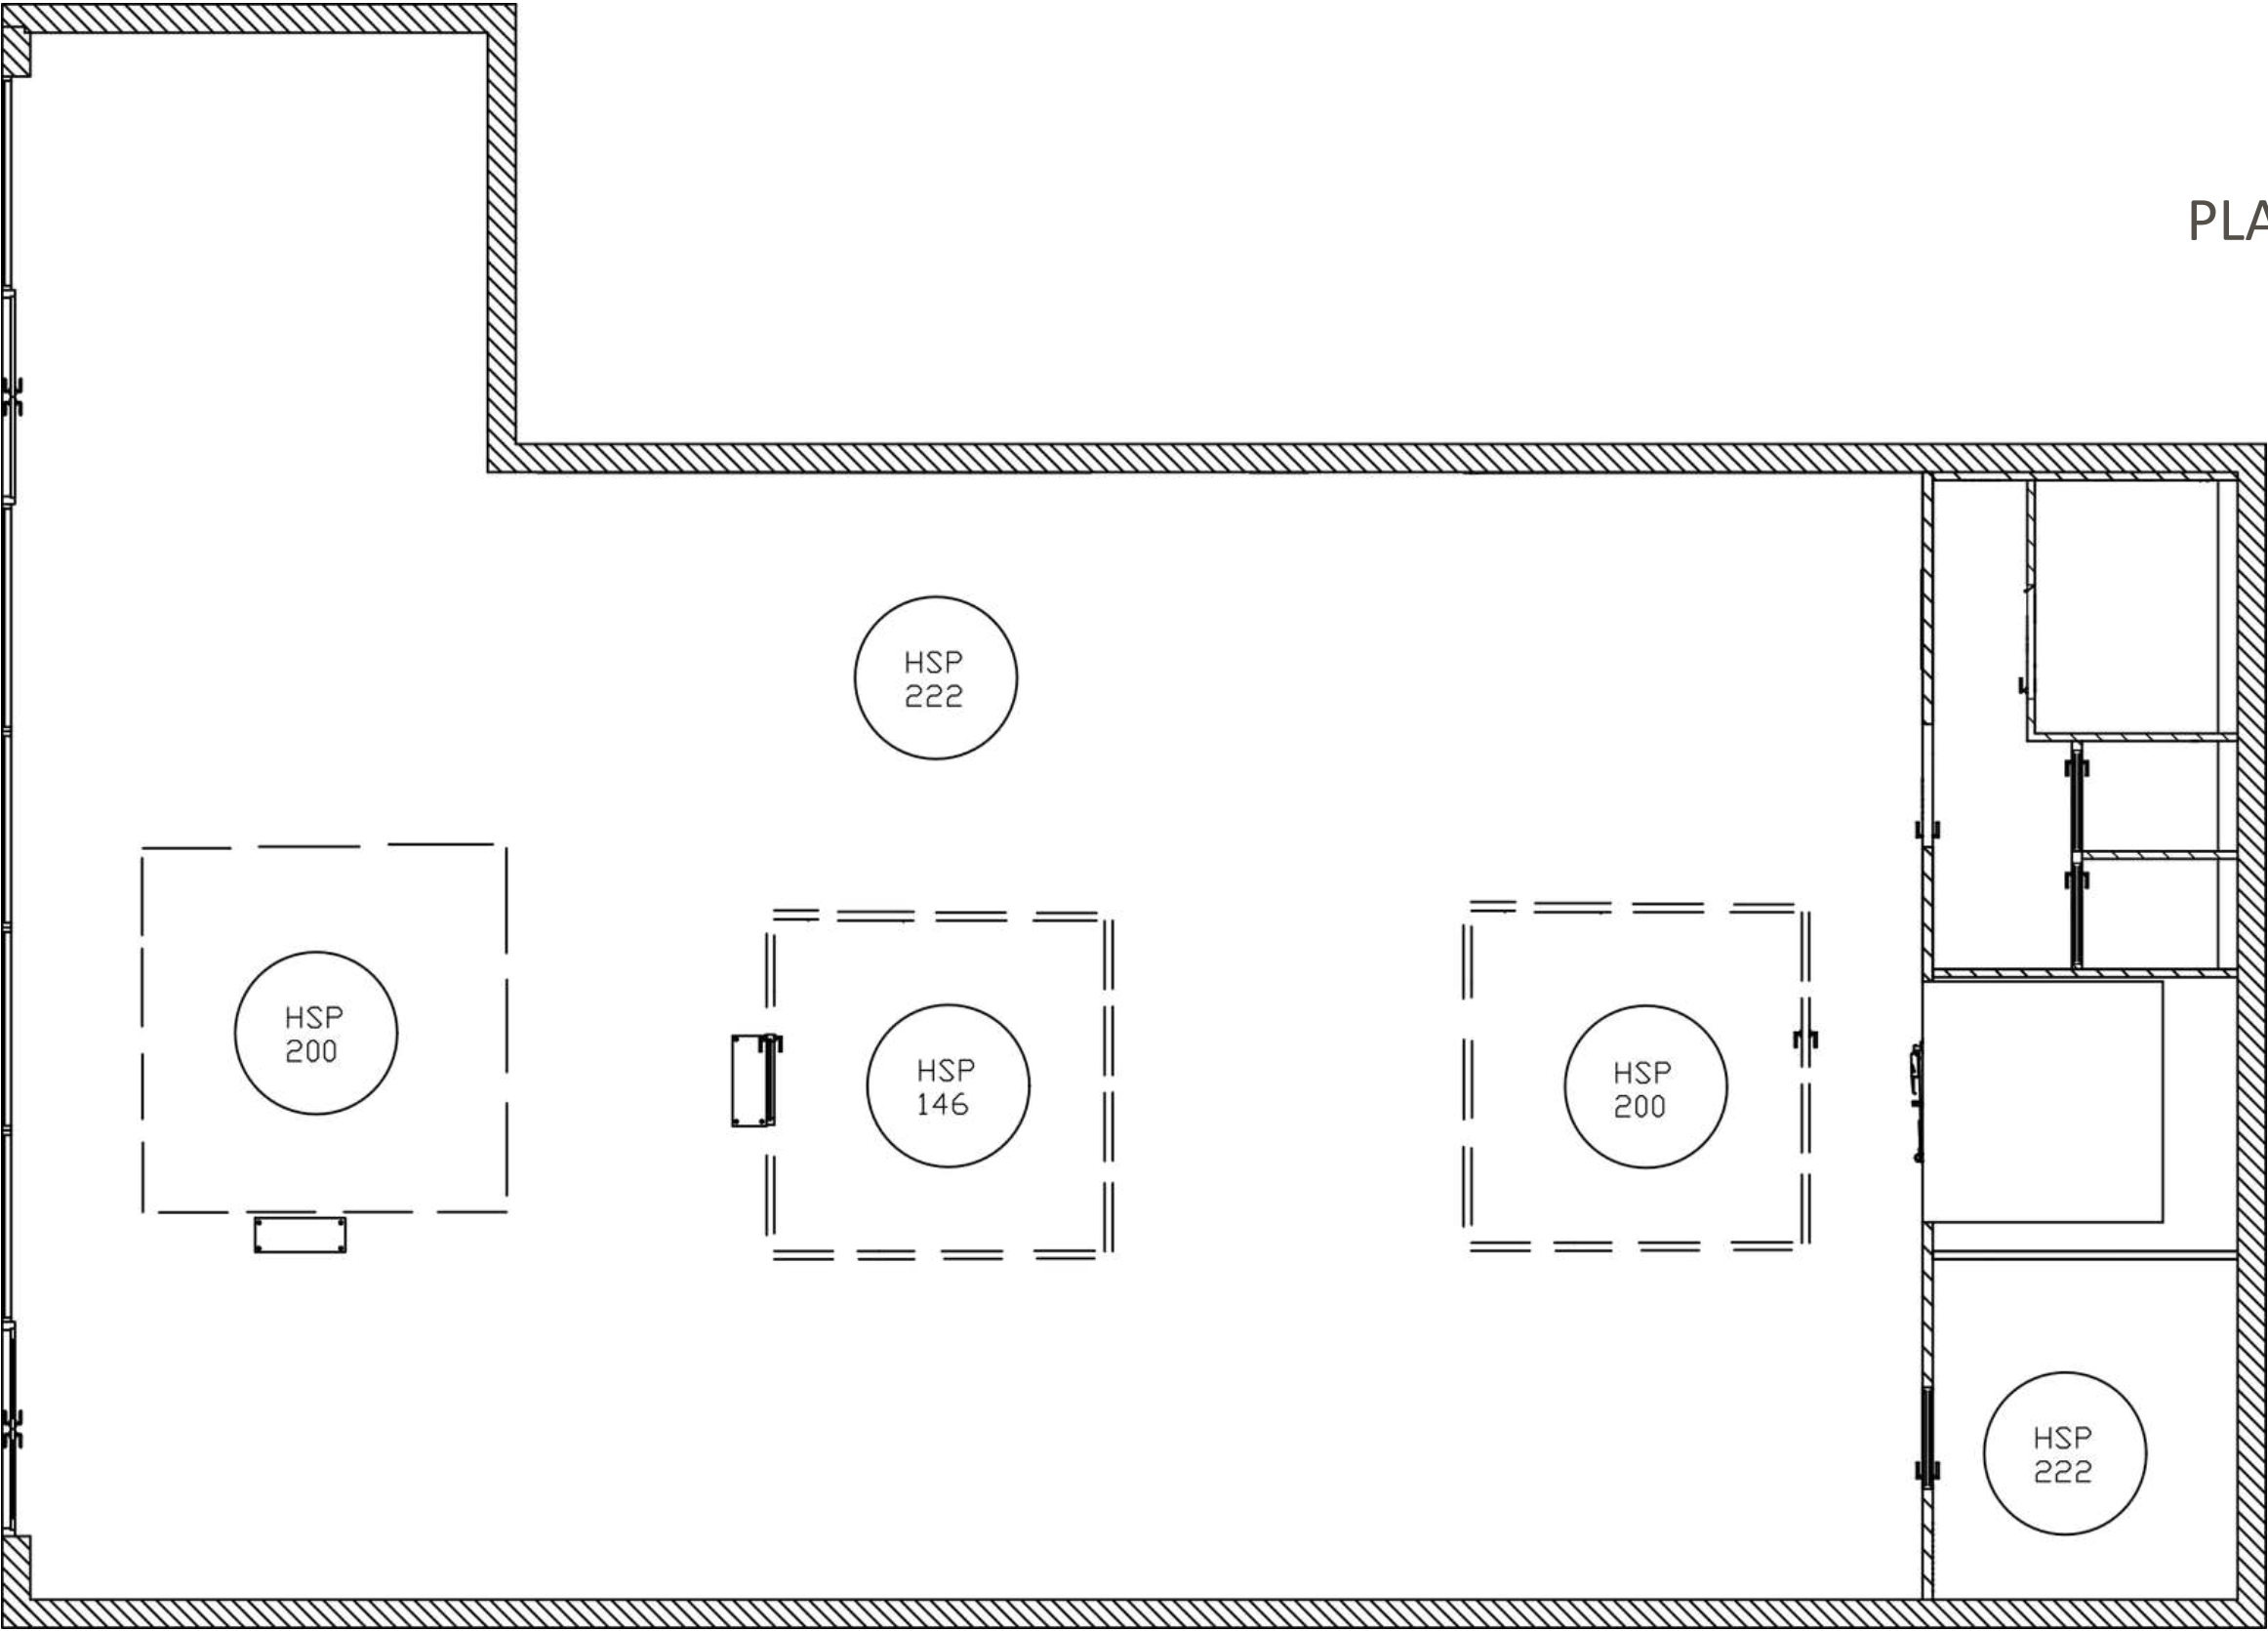

Ouvrage MATSAV ZOR 25 Terr de l'université,92000 Nanterre		Maitre d'oeuvre Léa Froger		Maitre D'ouvrage Marec Alon / Sahim Mohamed 12 rue Anatole France ,92000 Nanterre	
Titre Plan plafond Rdc		Echelle A3	Format 1/50	Date 30/04/2026	Etat du projet Projeté

Plan


PLAFOND R+1

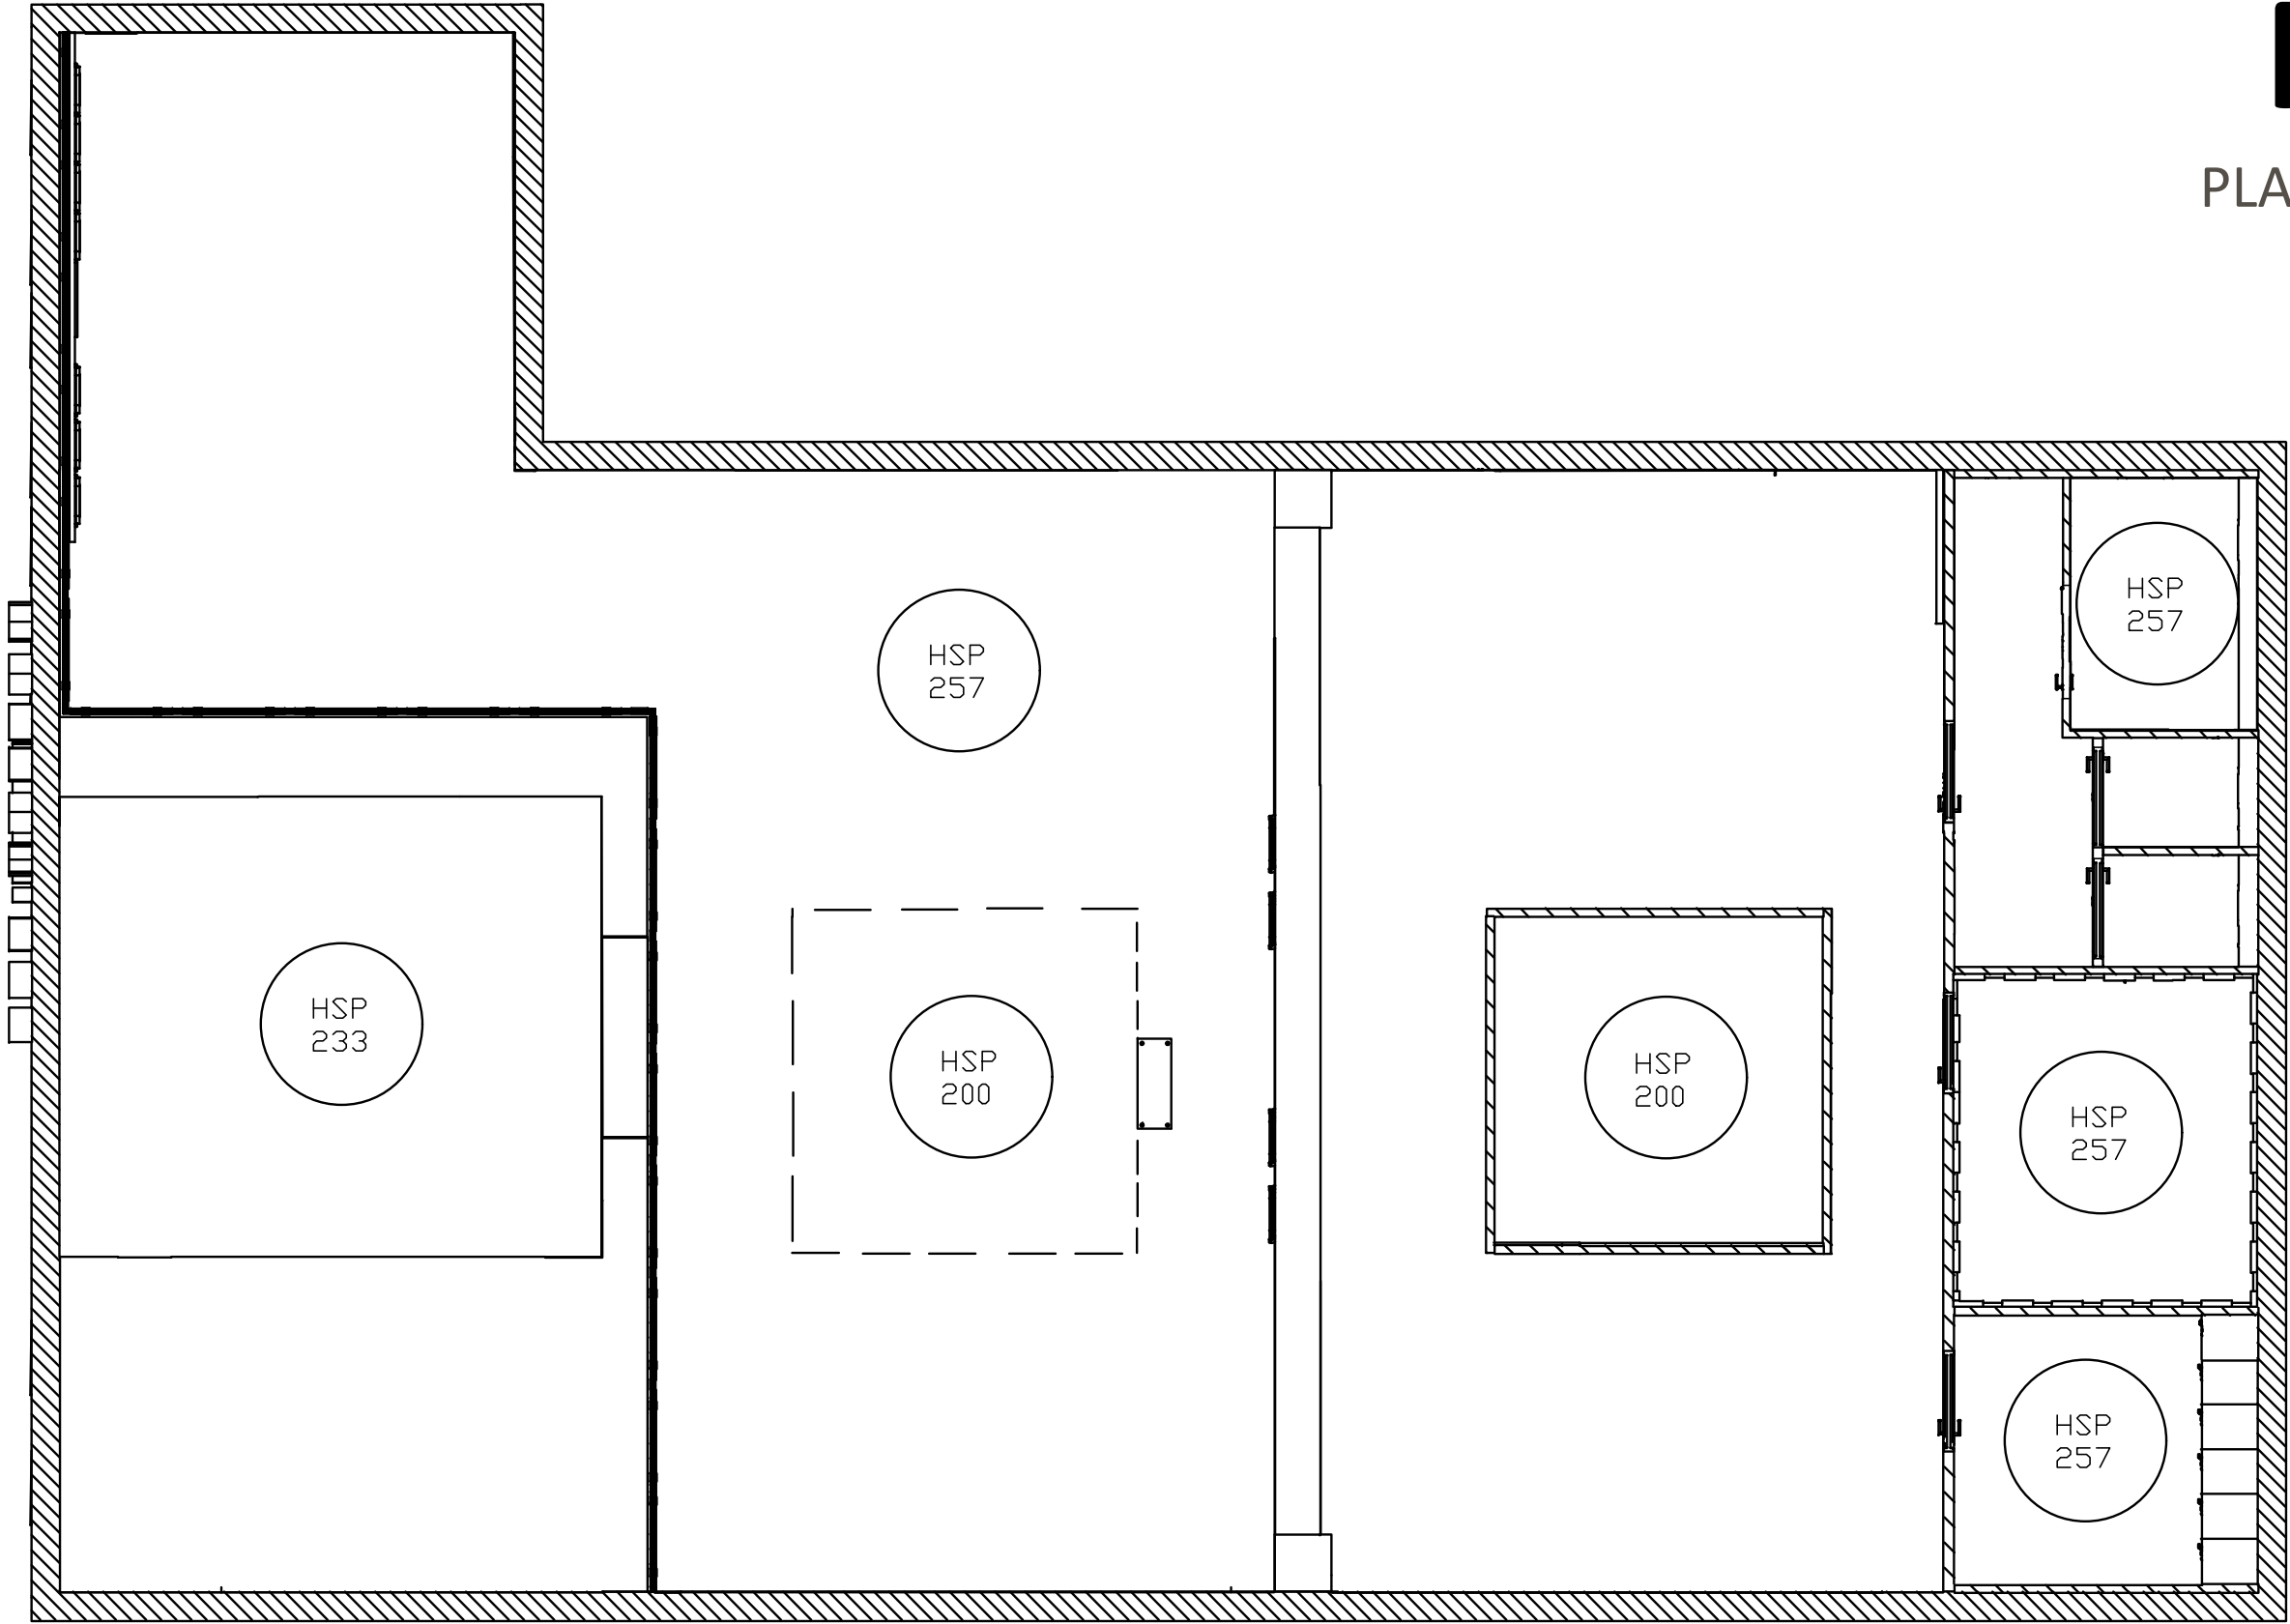

Ouvrage MATSAV ZOR 25 Terr de l'université,92000 Nanterre		Maitre d'oeuvre Léa Froger		Maitre D'ouvrage Marec Alon / Sahim Mohamed 12 rue Anatole France ,92000 Nanterre	
Titre Plan plafond R+1		Echelle A3	Format 1/50	Date 30/04/2026	Etat du projet Projeté

Plan


PMR RDC

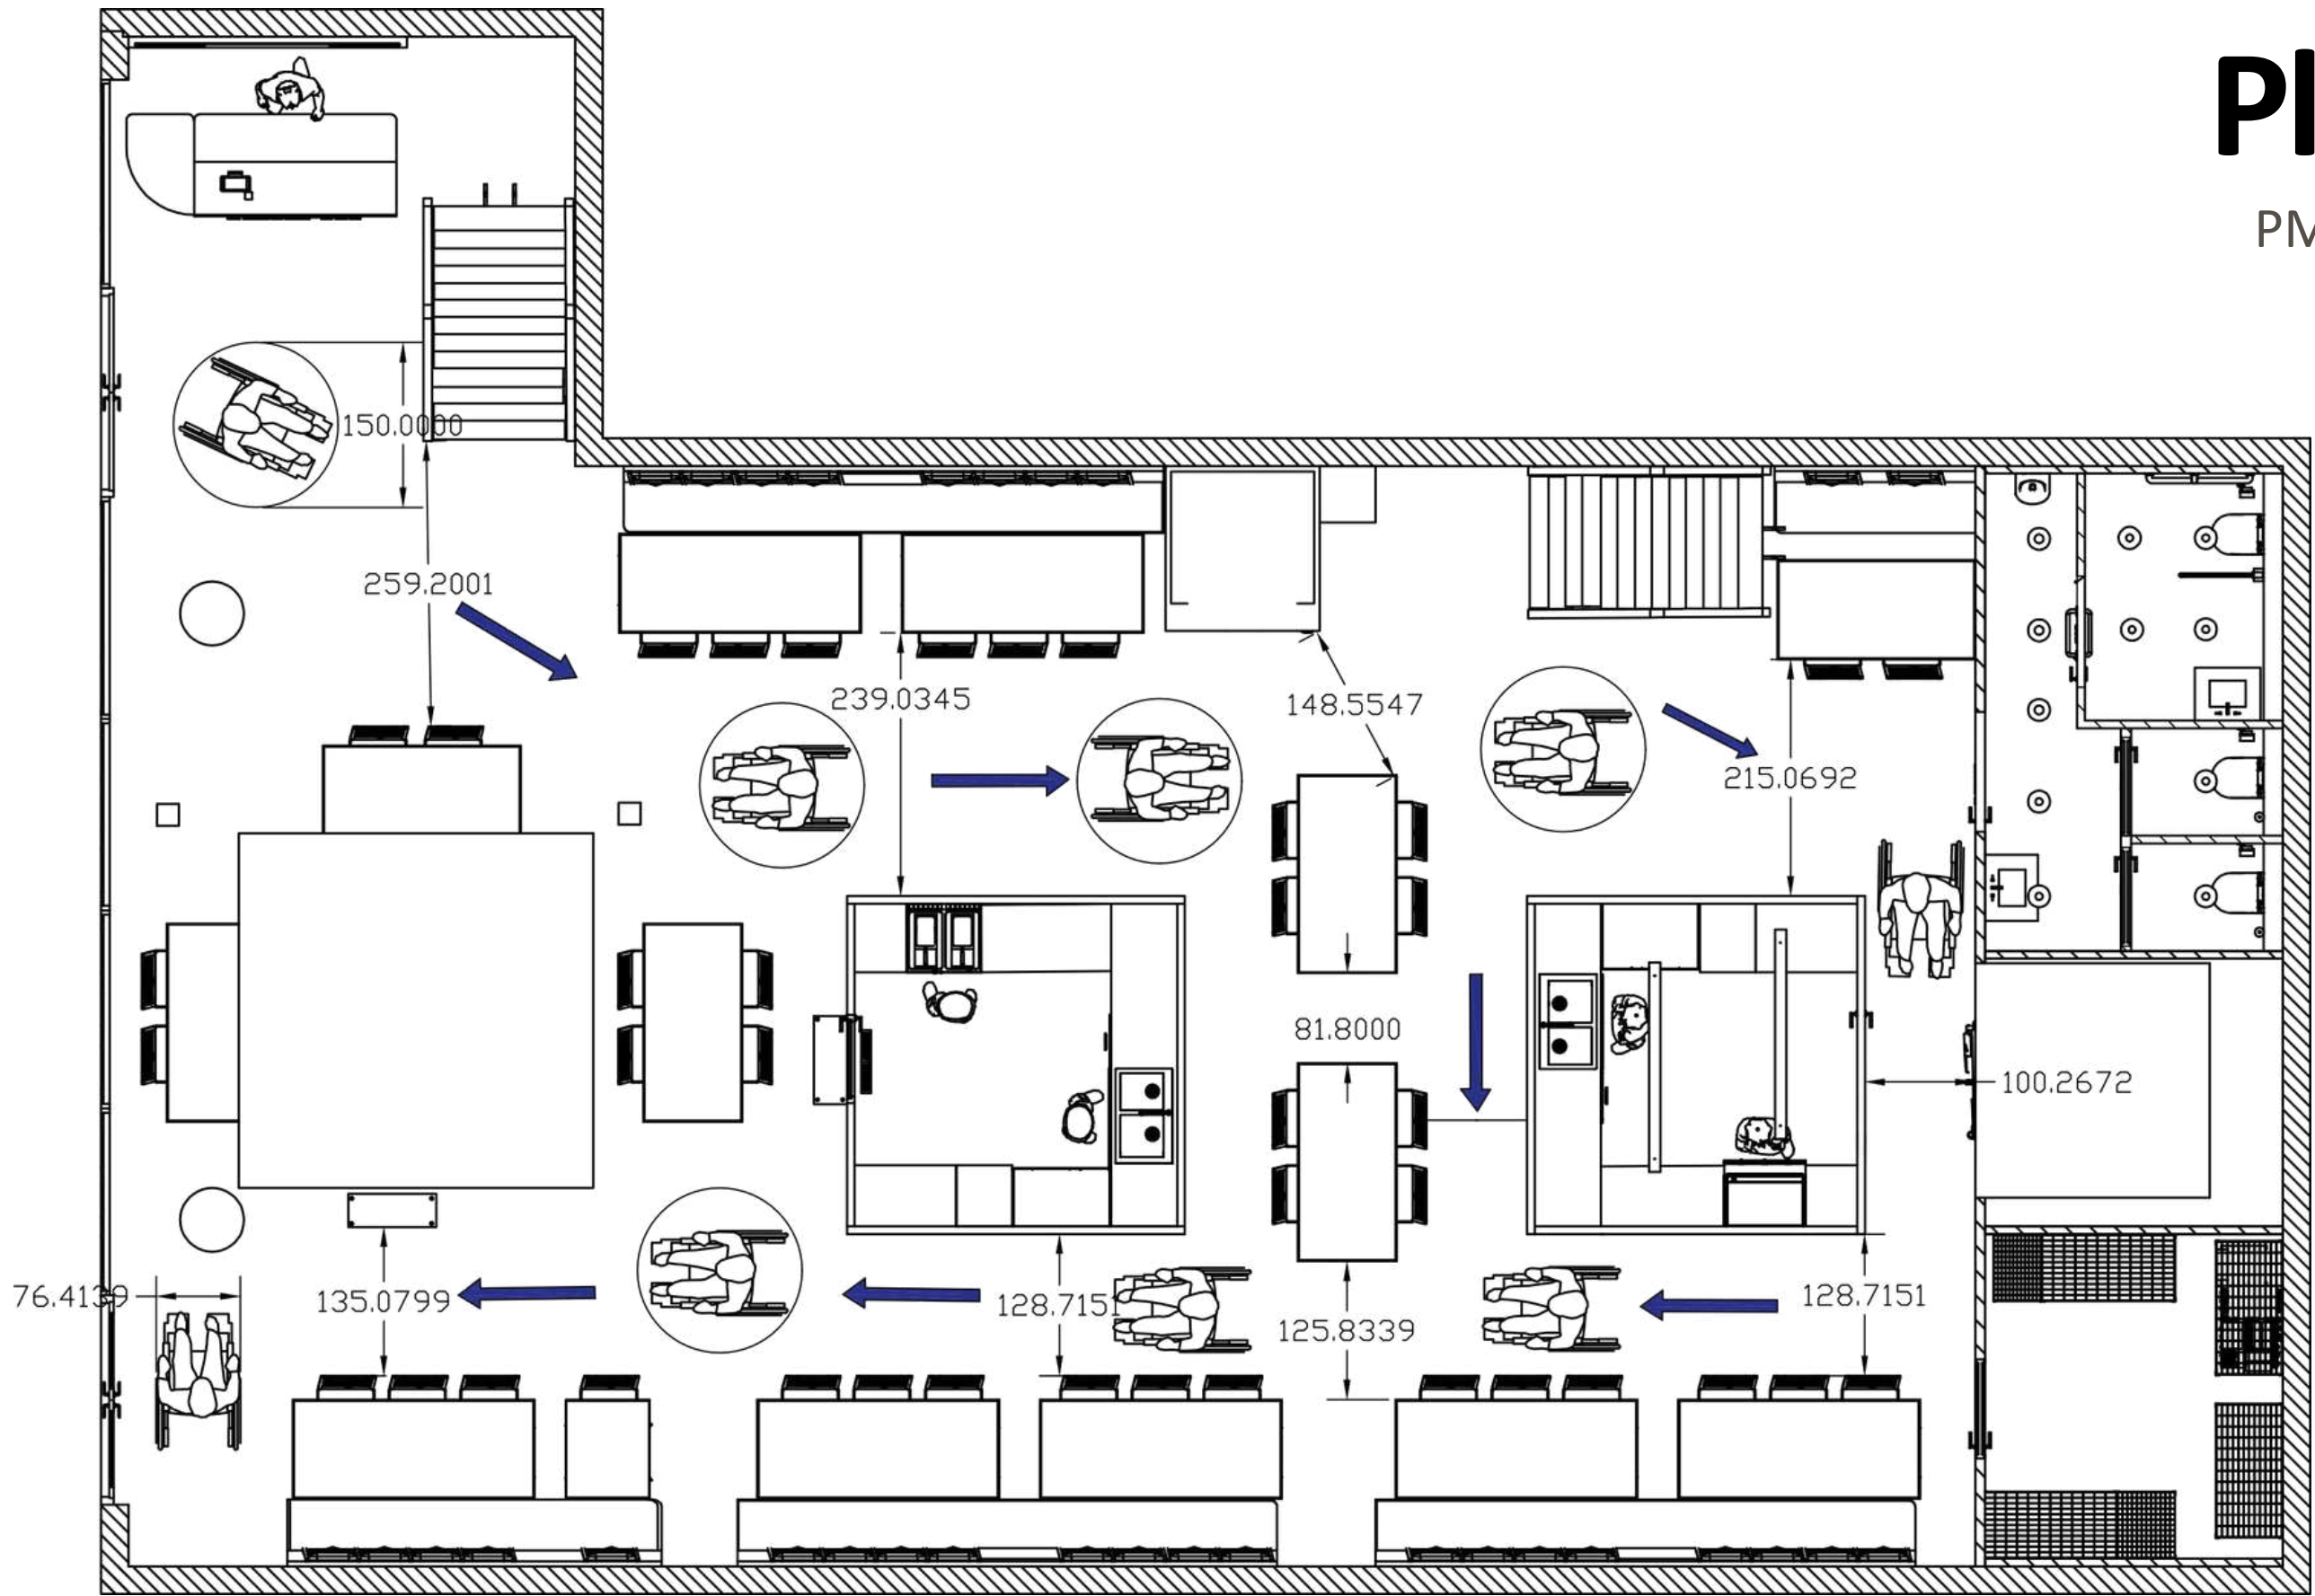

Ouvrage MATSAV ZOR 25 Terr de l'université,92000 Nanterre		Maitre d'oeuvre Léa Froger		Maitre D'ouvrage Marec Alon / Sahim Mohamed 12 rue Anatole France ,92000 Nanterre	
Titre Plan PMR Rdc		Echelle A3	Format 1/50	Date 30/04/2026	Etat du projet Projeté

Plan

PMR R+1

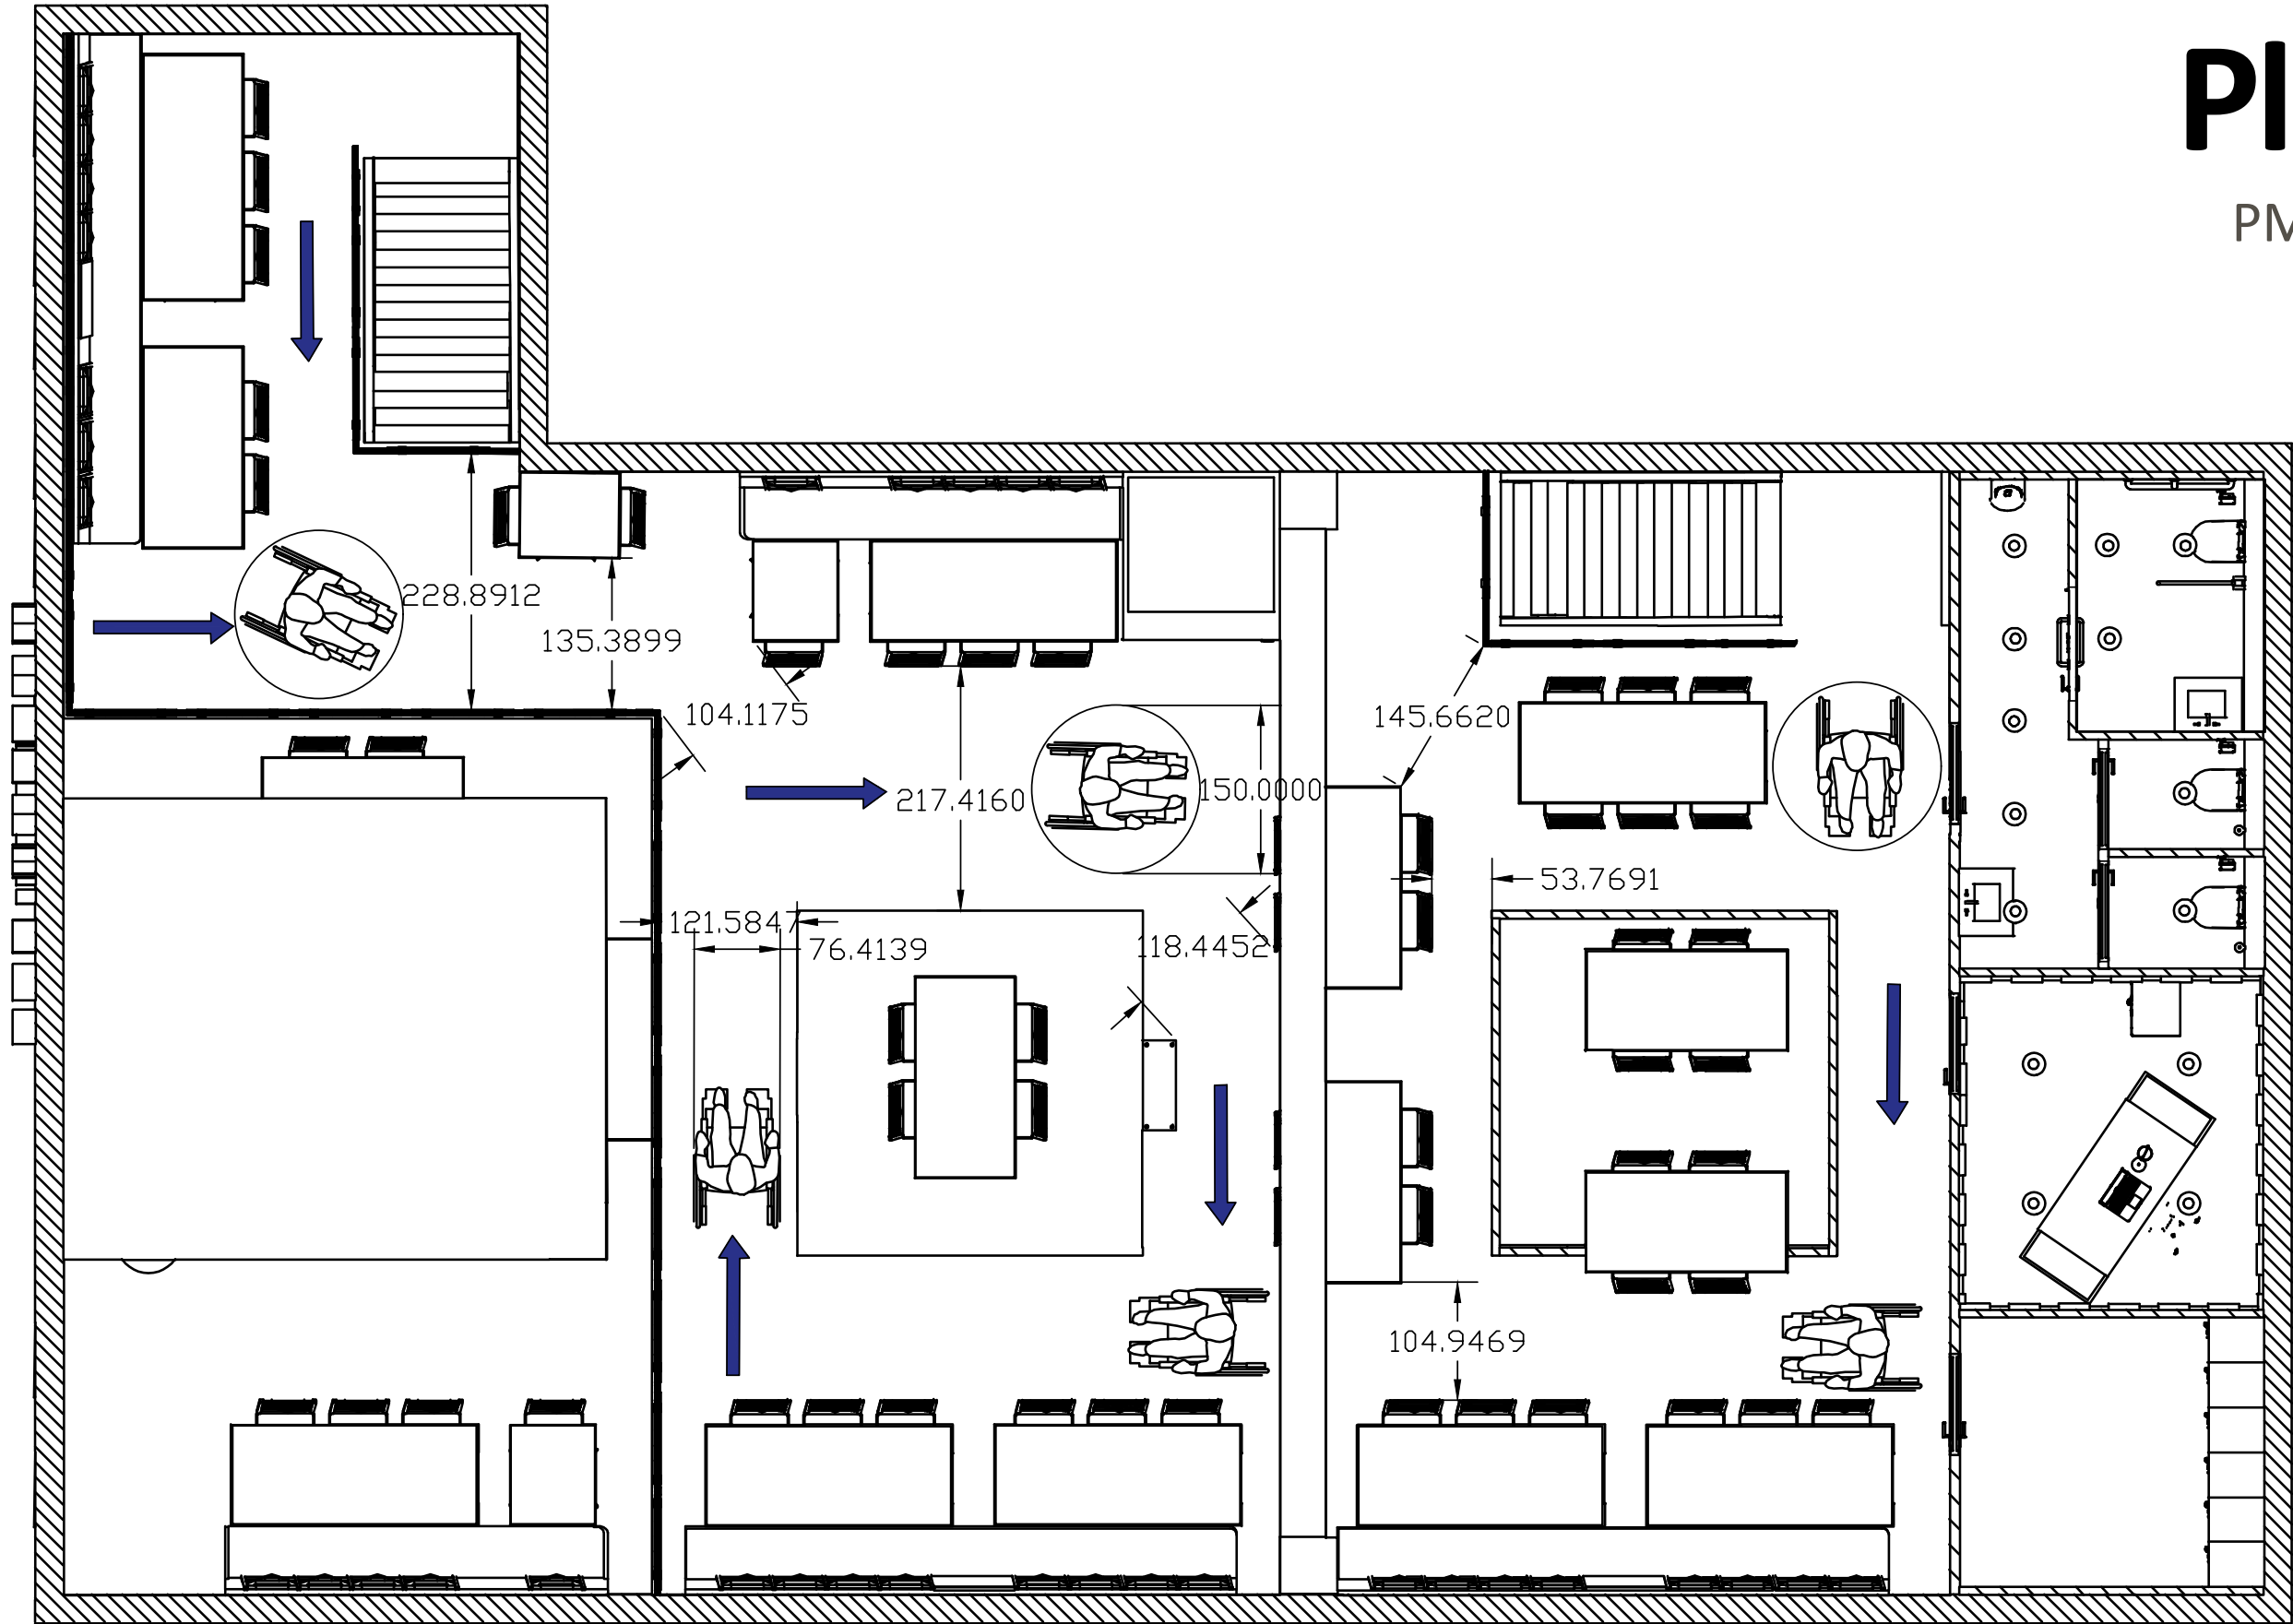

Ouvrage MATSAV ZOR 25 Terr de l'université,92000 Nanterre		Maitre d'oeuvre Léa Froger		Maitre D'ouvrage Marec Alon / Sahim Mohamed 12 rue Anatole France ,92000 Nanterre	
Titre Plan PMR R+1		Echelle A3	Format 1/50	Date 30/04/2026	Etat du projet Projeté

Plan

DE SECURITÉ RDC



- ZONE DE CIRCULATION
- PARTIES COMMUNES
- PARTIES PRIVÉE
- EXTINCTEUR A EAU
- EXTINCTEUR A CO2
- CIRCULATION
- BAES
- FLASH LUMINEUX
- COUPURE D'URGENCE
- PLAN D'INTERVENTION
- TGBT TABLEAU ÉLECTRIQUE
- CE COUPE ELÉCTRICITÉ
- CG COUPE GAZ

Ouvrage MATSAV ZOR 25 Terr de l'université,92000 Nanterre	Maitre d'oeuvre Léa Froger		Maitre D'ouvrage Marec Alon / Sahim Mohamed 12 rue Anatole France ,92000 Nanterre	
Titre Plan de sécurité RDC	Echelle A3	Format 1/50	Date 30/04/2026	Etat du projet Projeté

Plan

DE SECURITÉ R+1




- ZONE DE CIRCULATION
- PARTIES COMMUNES
- PARTIES PRIVÉE
- EXTINCTEUR A EAU
- EXTINCTEUR A CO2
- CIRCULATION
- BAES
- FLASH LUMINEUX
- COUPURE D'URGENCE
- PLAN D'INTERVENTION
- TGBT
- COUPE ELÉCTRICITÉ
- COUPE GAZ

Ouvrage MATSAV ZOR 25 Terr de l'université,92000 Nanterre		Maitre d'oeuvre Léa Froger		Maitre D'ouvrage Marec Alon / Sahim Mohamed 12 rue Anatole France ,92000 Nanterre	
Titre Plan securié R+1		Echelle A3	Format 1/50	Date 30/04/2026	Etat du projet Projeté

Facade

MATZAV ZOR

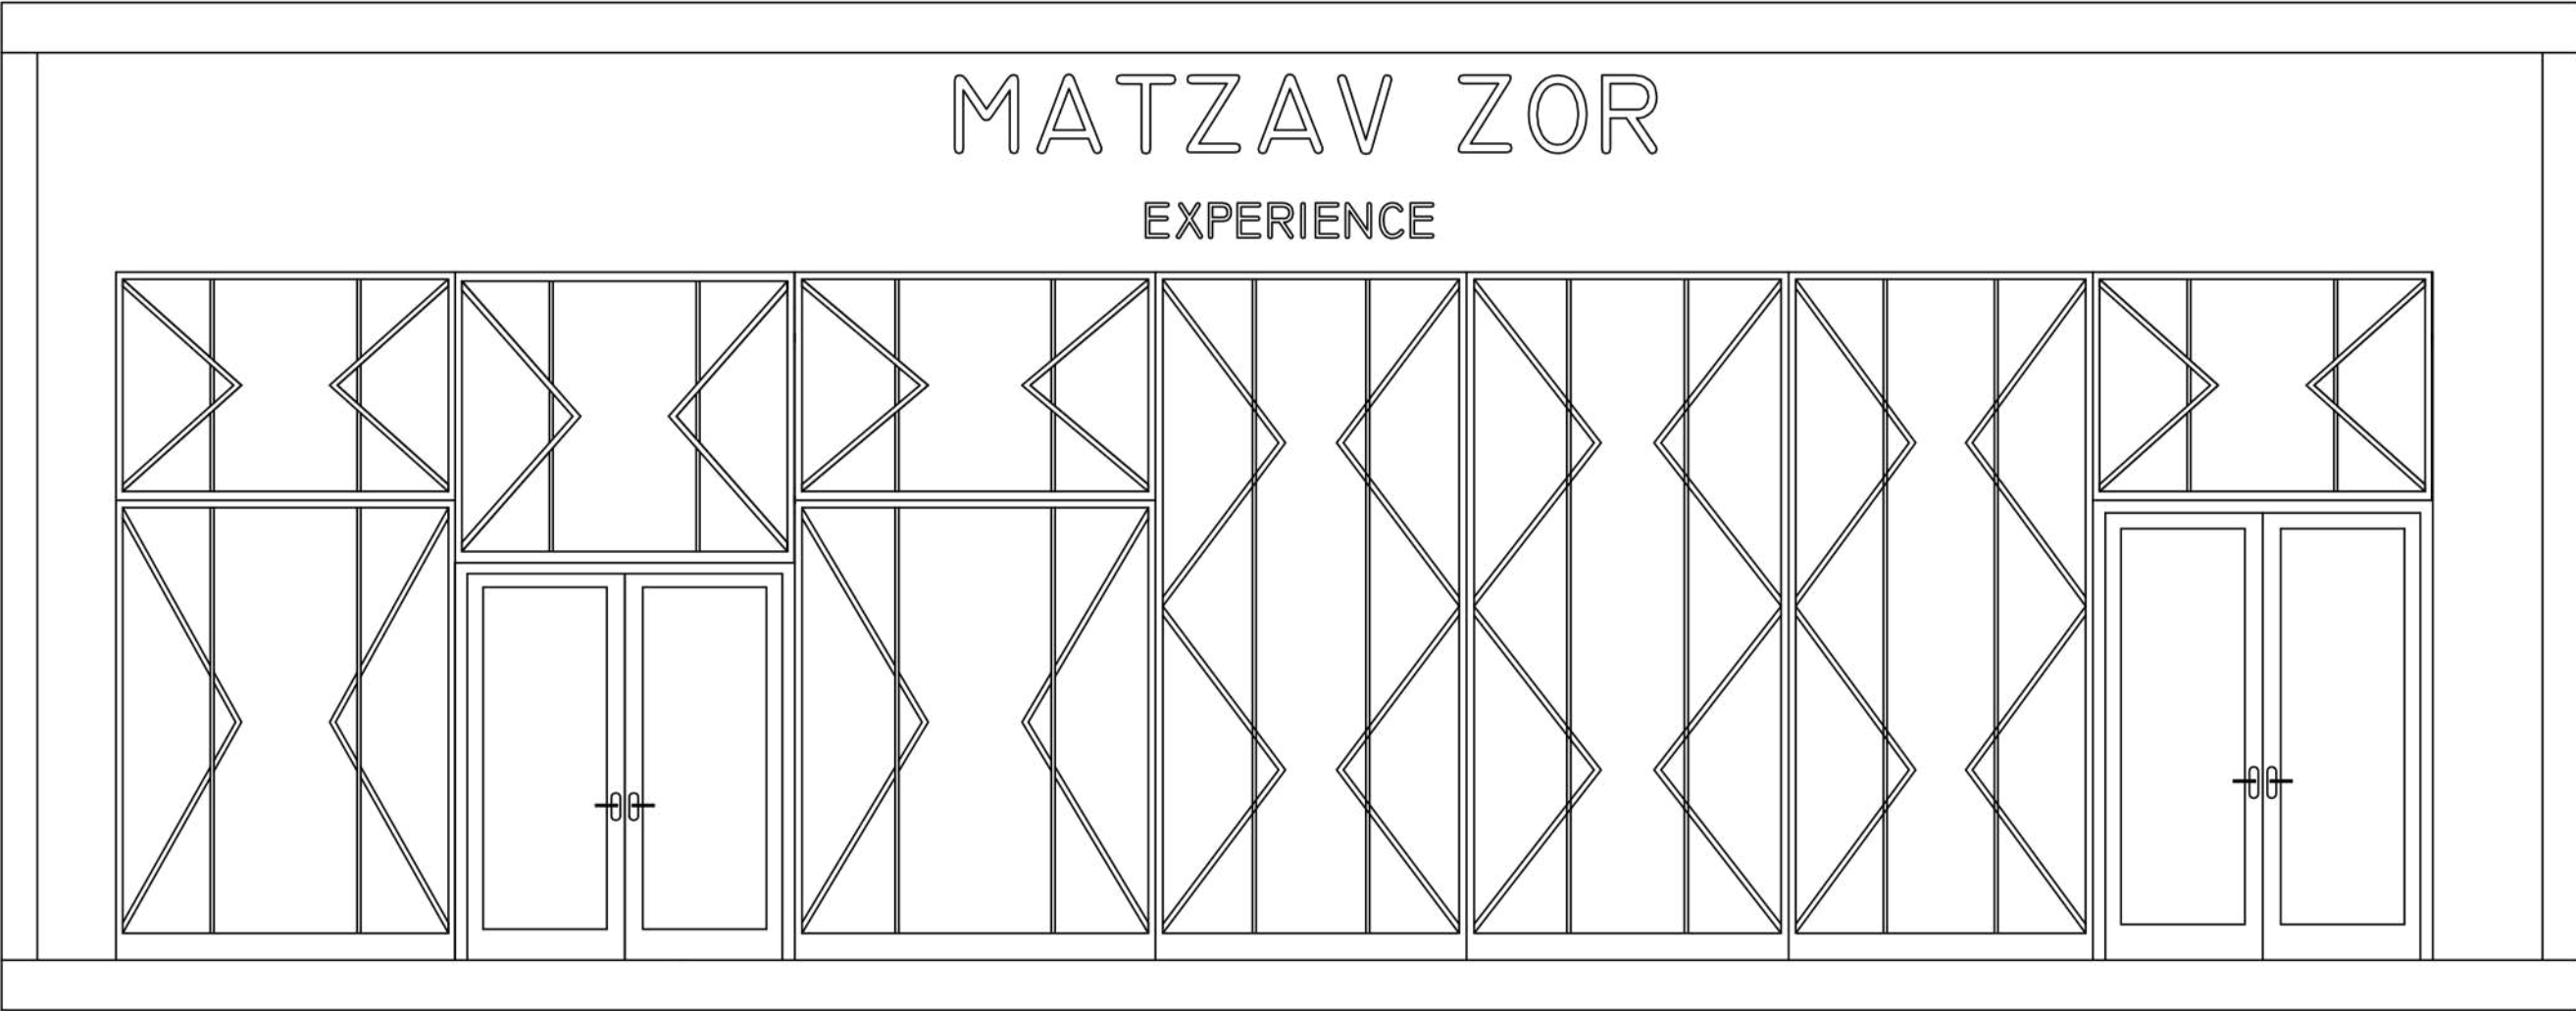

Ouvrage MATSAV ZOR 25 Terr de l'université,92000 Nanterre		Maitre d'oeuvre Léa Froger		Maitre D'ouvrage Marec Alon / Sahim Mohamed 12 rue Anatole France ,92000 Nanterre	
Titre Facade		Echelle A3	Format 1/50	Date 30/04/2026	Etat du projet Projeté

Facade texturée

MATZAV ZOR




Ouvrage MATSAV ZOR 25 Terr de l'université,92000 Nanterre	Maitre d'oeuvre Léa Froger		Maitre D'ouvrage Marec Alon / Sahim Mohamed 12 rue Anatole France ,92000 Nanterre	
Titre Facade texturée	Echelle A3	Format 1/50	Date 30/04/2026	Etat du projet Projeté



Coupe

AA

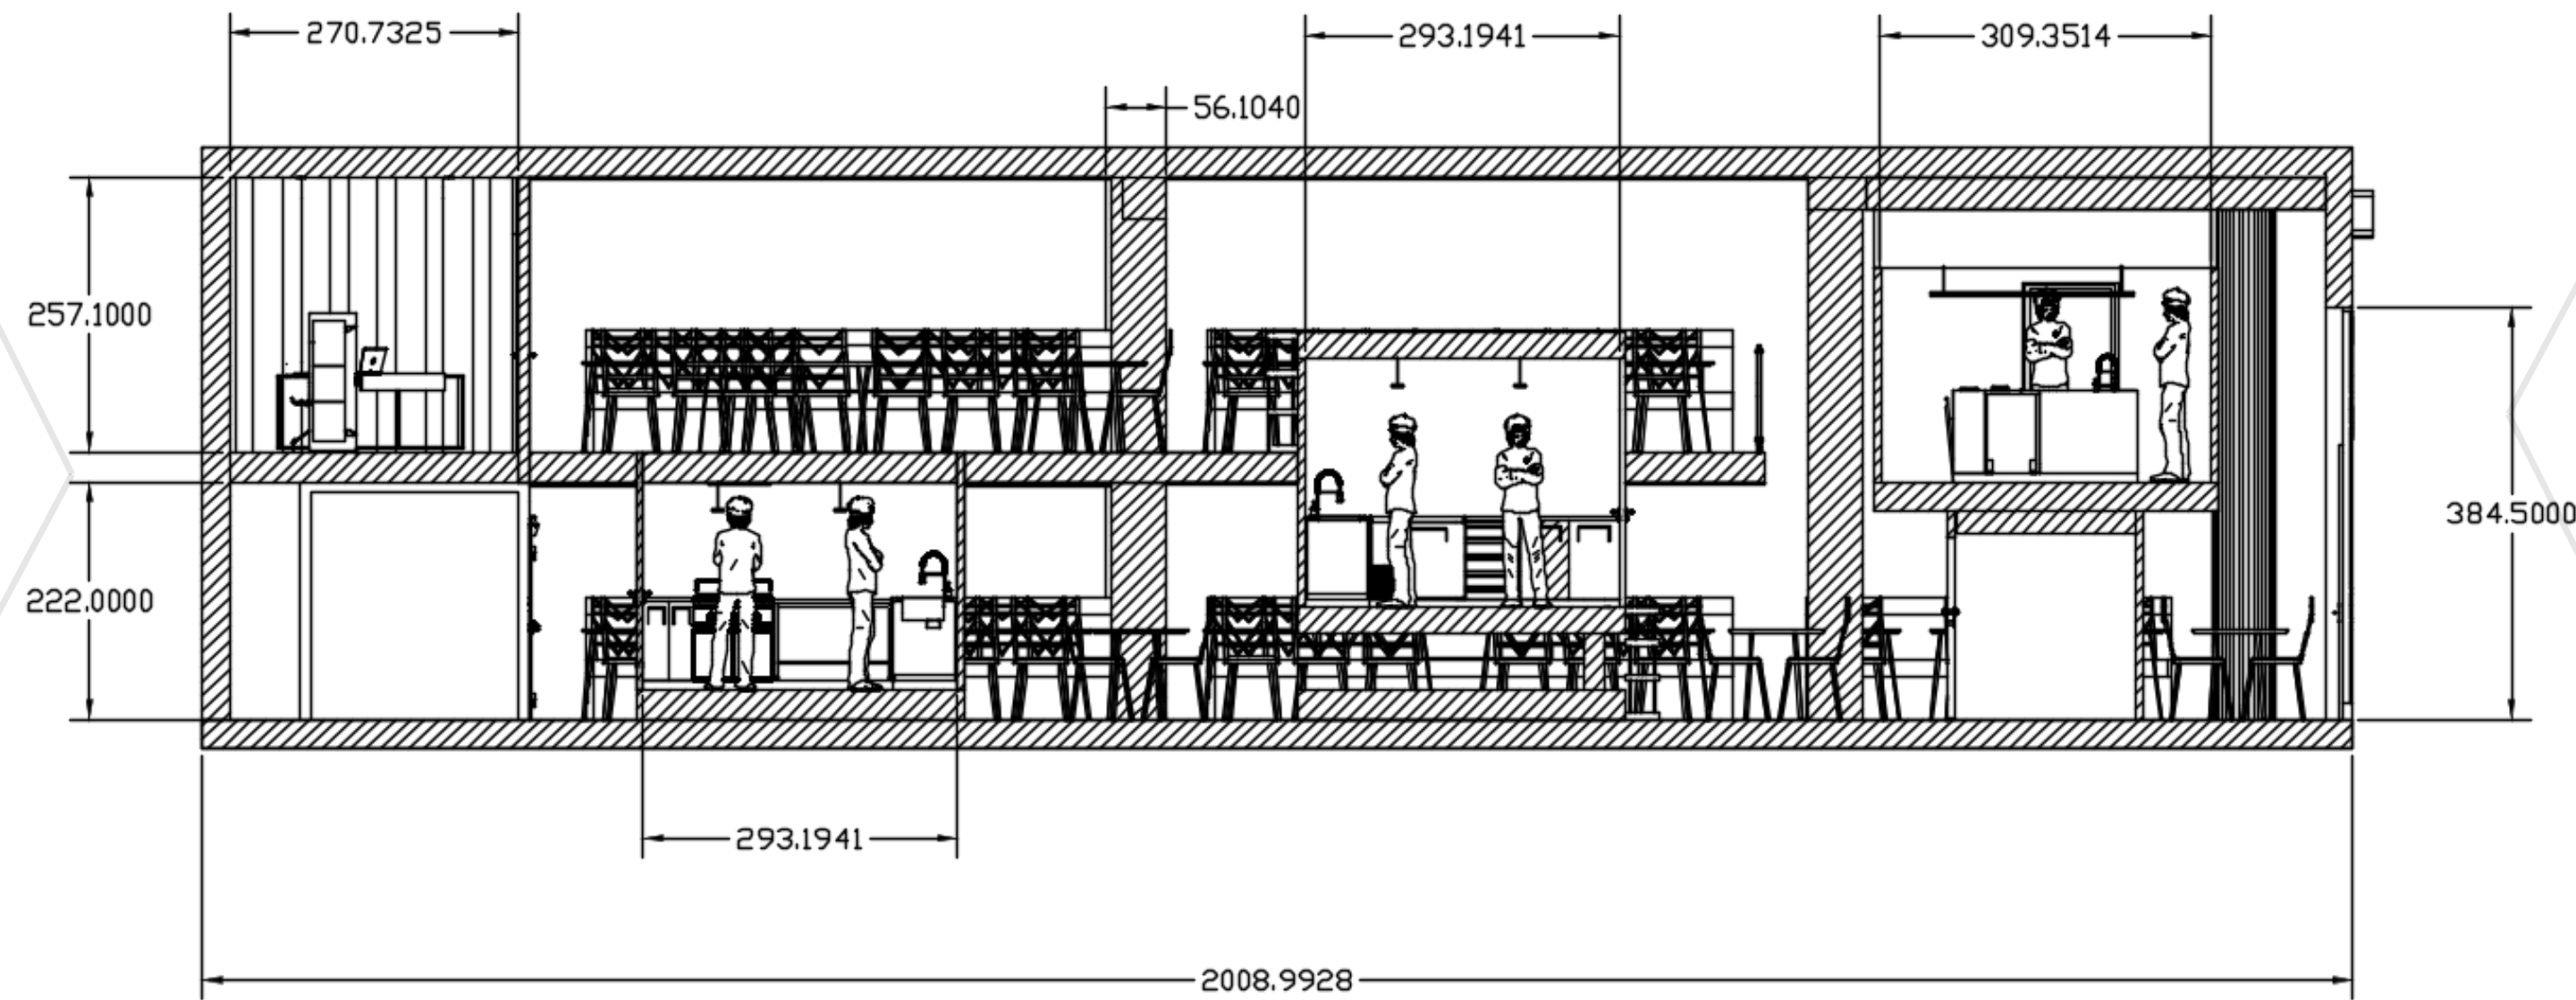


Ouvrage MATSAV ZOR 25 Terr de l'université,92000 Nanterre	Maitre d'oeuvre Léa Froger		Maitre D'ouvrage Marec Alon / Sahim Mohamed 12 rue Anatole France ,92000 Nanterre	
Titre Coupe AA	Echelle A3	Format 1/50	Date 30/04/2026	Etat du projet Projeté



Coupe

BB

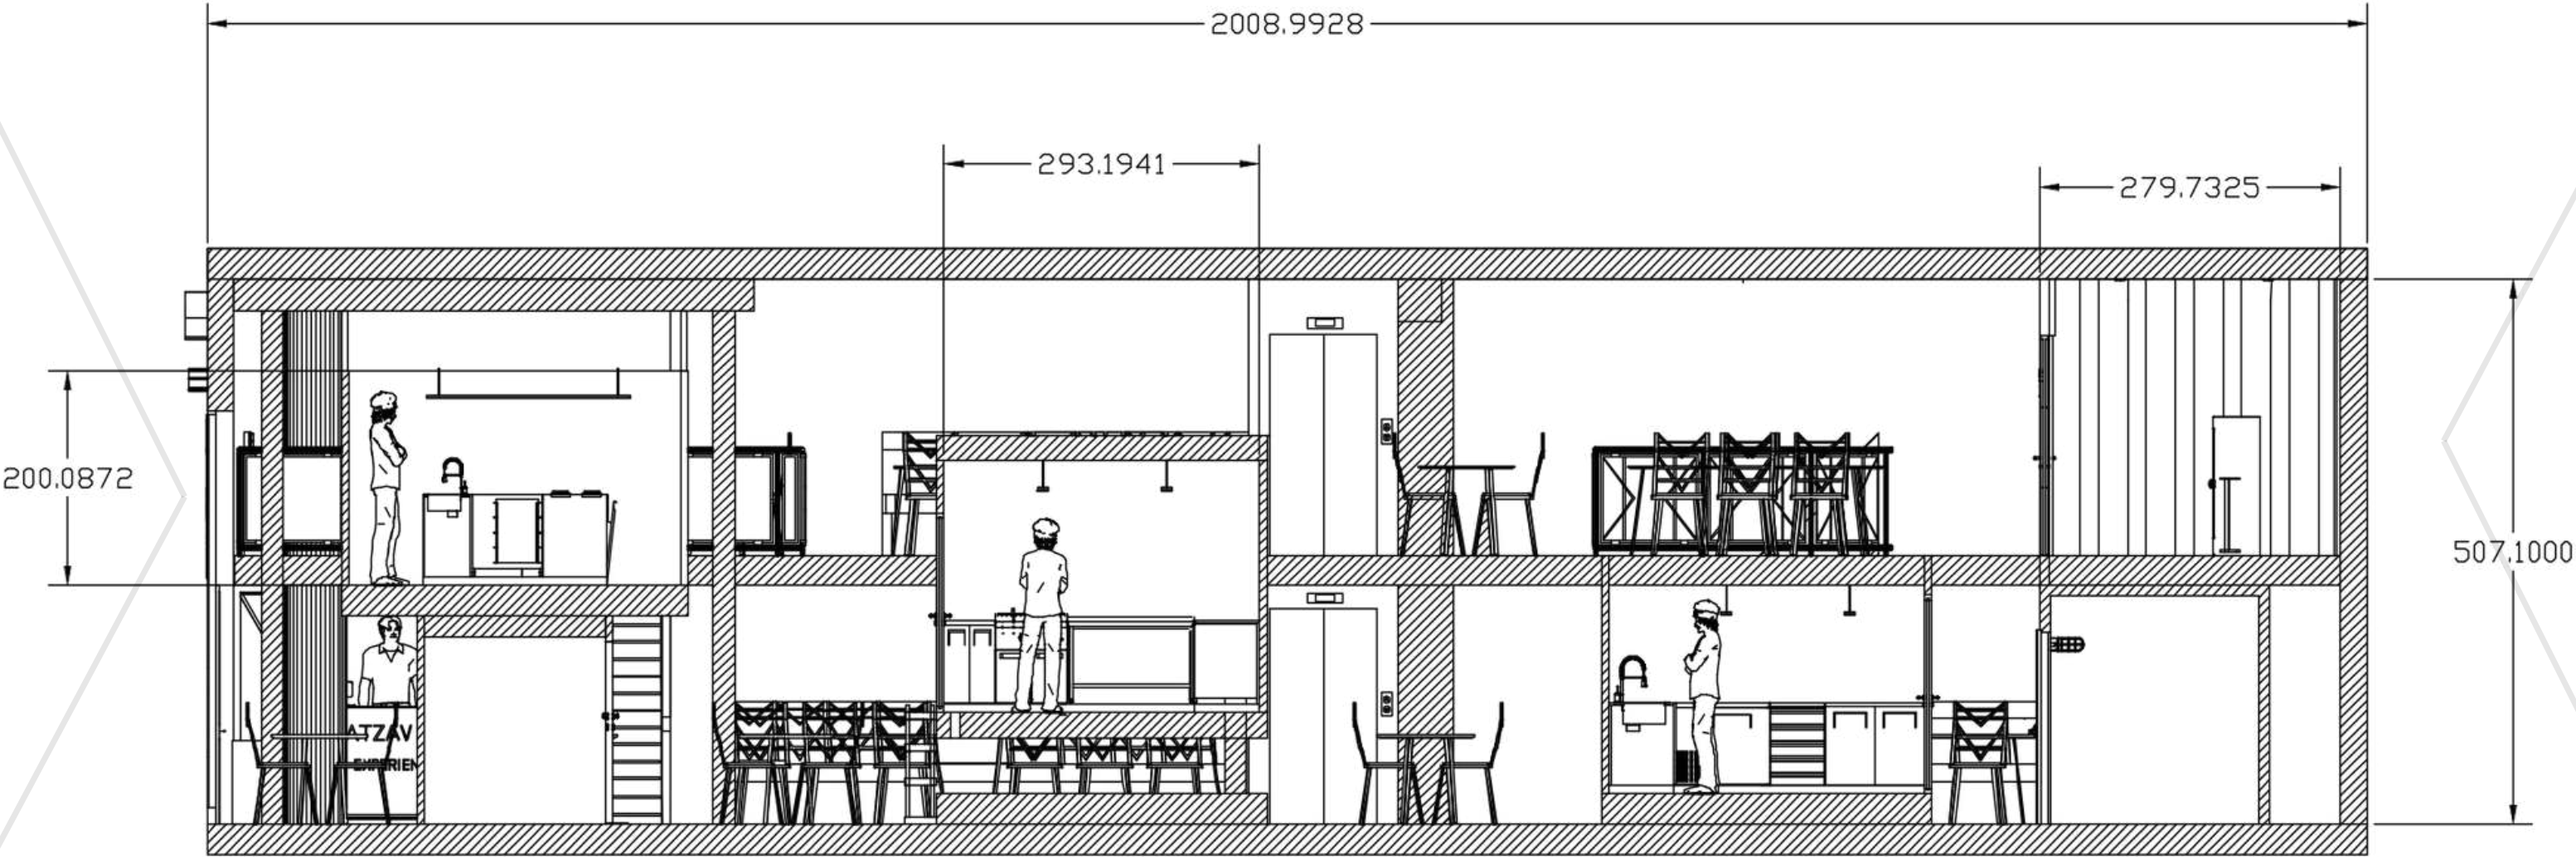


Ouvrage MATSAV ZOR 25 Terr de l'université,92000 Nanterre		Maitre d'oeuvre Léa Froger		Maitre D'ouvrage Marec Alon / Sahim Mohamed 12 rue Anatole France ,92000 Nanterre	
Titre Coupe BB		Echelle A3	Format 1/50	Date 30/04/2026	Etat du projet Projeté



Coupe

CC

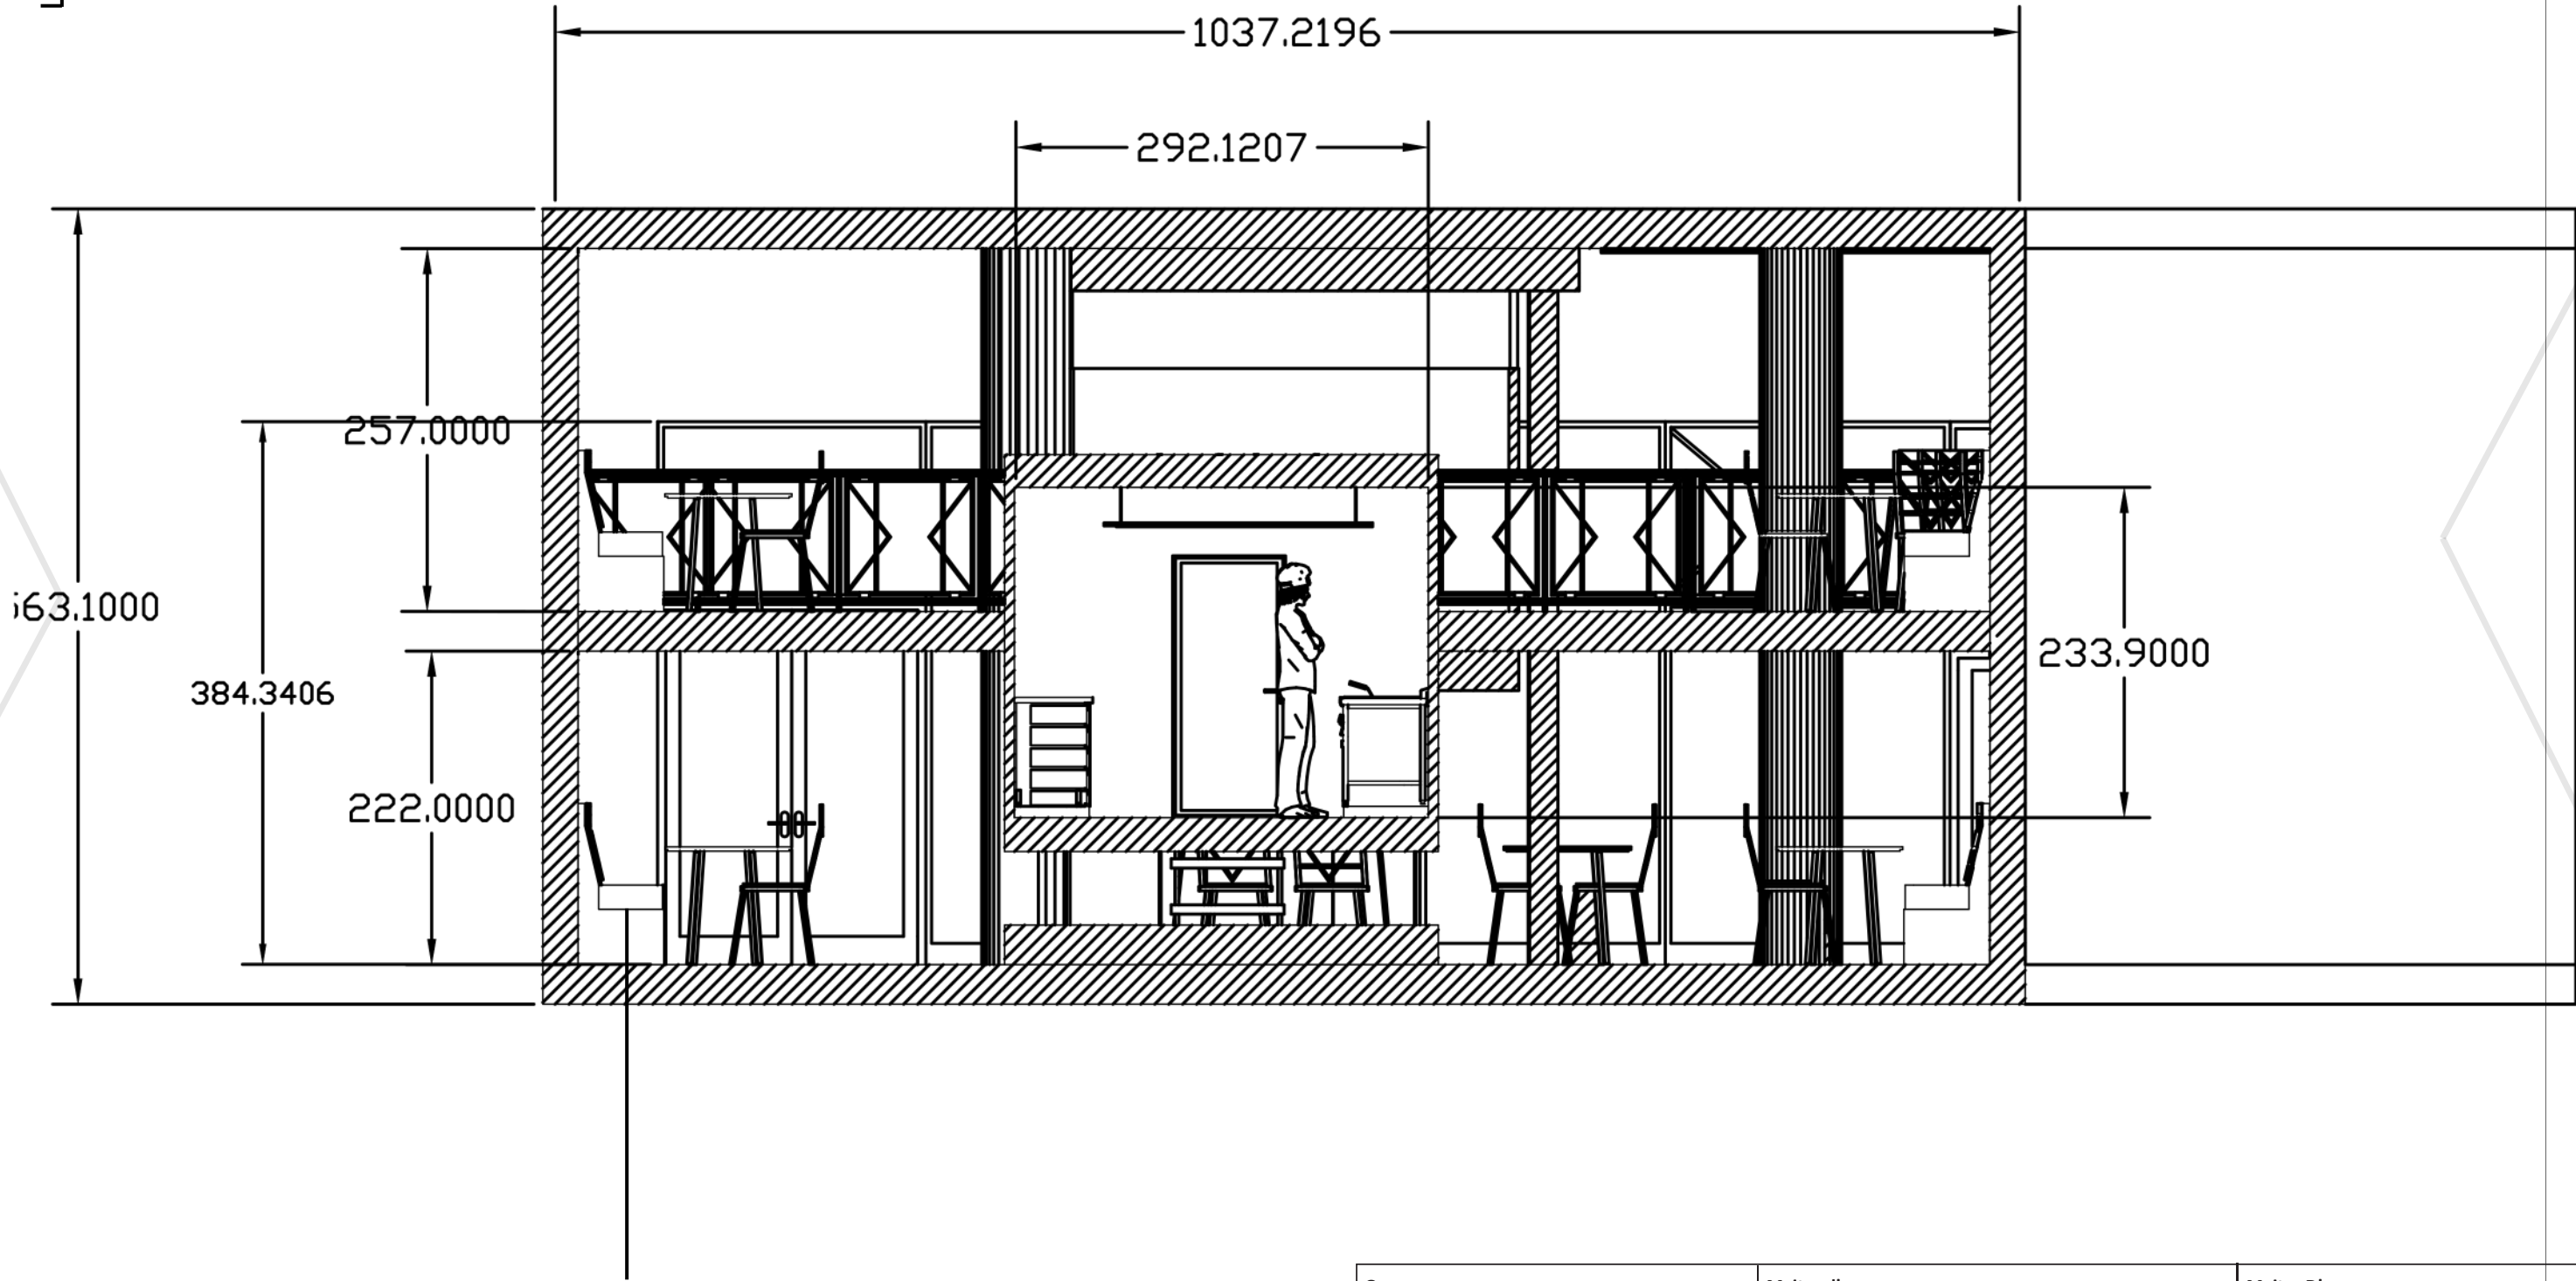


Ouvrage MATSAV ZOR 25 Terr de l'université,92000 Nanterre		Maitre d'oeuvre Léa Froger		Maitre D'ouvrage Marec Alon / Sahim Mohamed 12 rue Anatole France ,92000 Nanterre	
Titre Coupe CC		Echelle A3	Format 1/50	Date 30/04/2026	Etat du projet Projeté



Coupe

DD

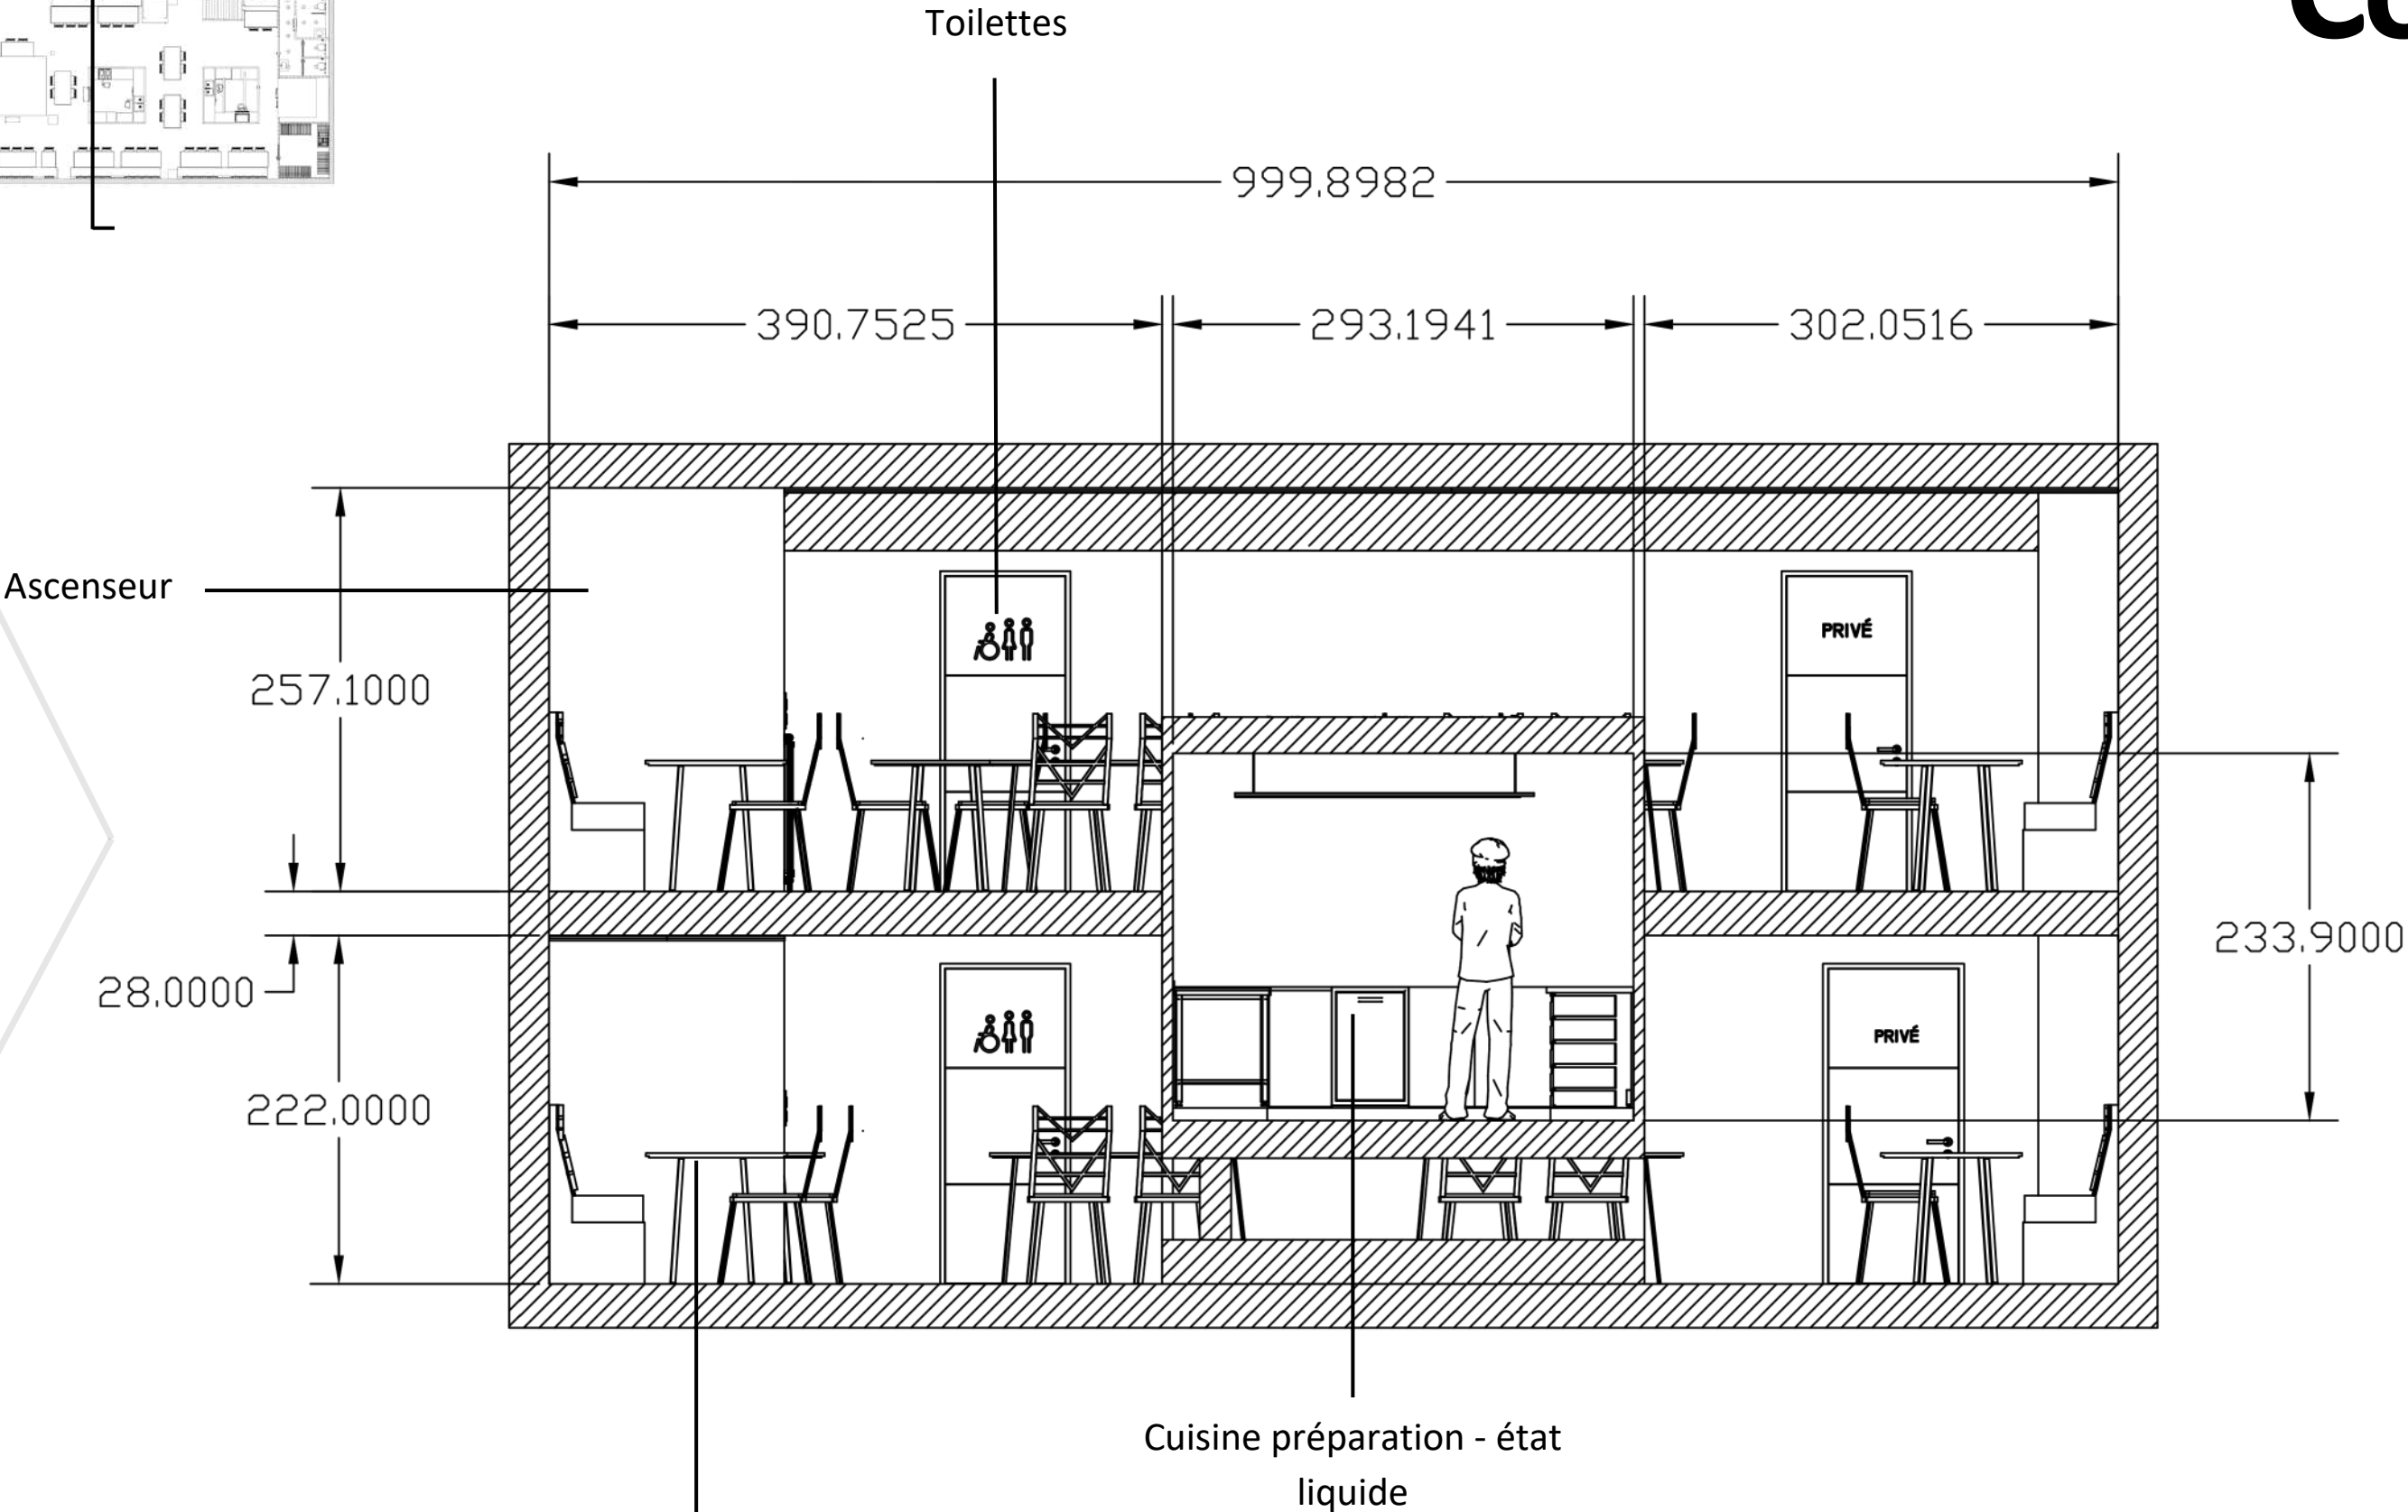

Espace de
dégustation

Cuisine préparation - état
liquide

Ouvrage MATSAV ZOR 25 Terr de l'université,92000 Nanterre		Maitre d'oeuvre Léa Froger		Maitre D'ouvrage Marec Alon / Sahim Mohamed 12 rue Anatole France ,92000 Nanterre	
Titre Coupe DD		Echelle A3	Format 1/50	Date 30/04/2026	Etat du projet Projeté

Coupe

AA TEXTURÉE



CUISINE

ESPACE RESTAURATION

LOCAL TECHNIQUE

Ouvrage MATSAV ZOR 25 Terr de l'université,92000 Nanterre	Maitre d'oeuvre Léa Froger		Maitre D'ouvrage Marec Alon / Sahim Mohamed 12 rue Anatole France ,92000 Nanterre	
Titre Coupe AA Texturée	Echelle A3	Format 1/50	Date 30/04/2026	Etat du projet Projeté

Coupe

BB TEXTURÉE

CUISINE - ETAT GAZEUX

BUREAU



Ouvrage MATSAV ZOR 25 Terr de l'université,92000 Nanterre	Maitre d'oeuvre Léa Froger		Maitre D'ouvrage Marec Alon / Sahim Mohamed 12 rue Anatole France ,92000 Nanterre	
Titre Coupe BB Texturée	Echelle A3	Format 1/50	Date 30/04/2026	Etat du projet Projeté

Coupe

CC TEXTURÉE




CUISINE - ETAT LIQUIDE

Ouvrage MATSAV ZOR 25 Terr de l'université,92000 Nanterre	Maitre d'oeuvre Léa Froger		Maitre D'ouvrage Marec Alon / Sahim Mohamed 12 rue Anatole France ,92000 Nanterre	
Titre Coupe CC texturée	Echelle A3	Format 1/50	Date 30/04/2026	Etat du projet Projeté

Coupe

DD TEXTURÉE

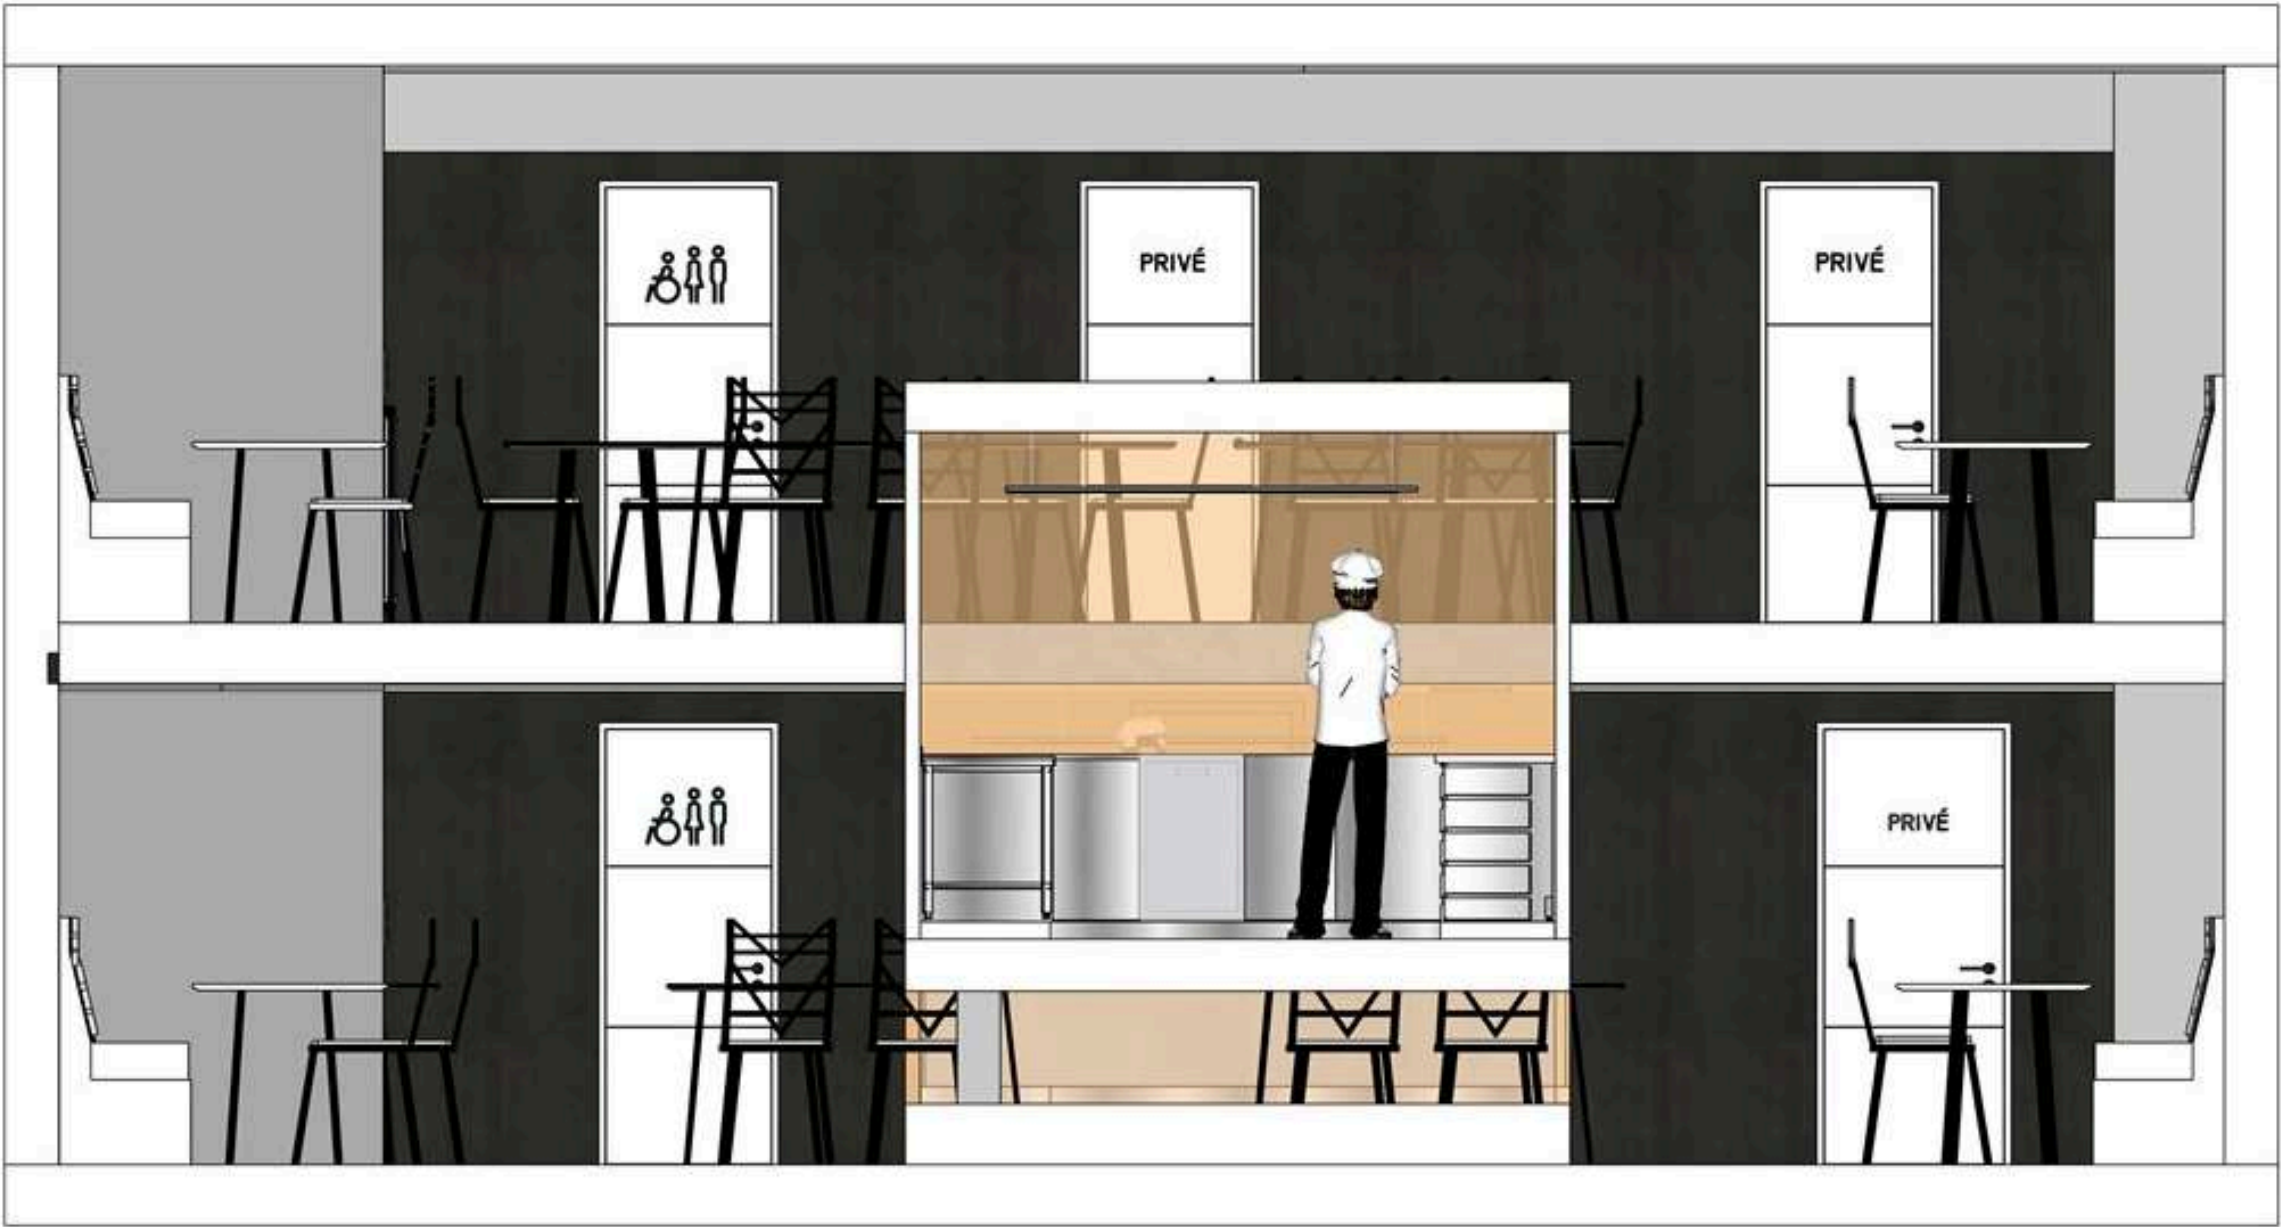

Ouvrage MATSAV ZOR 25 Terr de l'université,92000 Nanterre		Maitre d'oeuvre Léa Froger		Maitre D'ouvrage Marec Alon / Sahim Mohamed 12 rue Anatole France ,92000 Nanterre	
Titre Coupe DD texturée		Echelle A3	Format 1/50	Date 30/04/2026	Etat du projet Projeté


Planche ERP

Données	Informations
Type d'ERP	Type N – Restaurant
Catégorie ERP	5 (moins de 200 personnes)
Superficie totale	385 m ²
Surface accessible au public	324 m ²
Effectif public estimé	138 (2.35 m ² / pers)
Effectif personnel	13 personnes
Nombre de niveaux	2 niveaux
Nombre d'issues de secours	2
Largeur de circulation principale	1.40 m
Accessibilité PMR	Oui rdc et R+1 (ascenseur)
Moyen de secours	4 extincteurs, éclairage sécurité signalétique
Désenfumage/ ventilation	Hotte dans la cuisine, ventilation naturelle et/ou extraction d'air dans les cuisines
Hauteur sous plafond	Rdc : 2.20 m / R+1 : 2.55 m

Visuel 3D



Visuel 3D

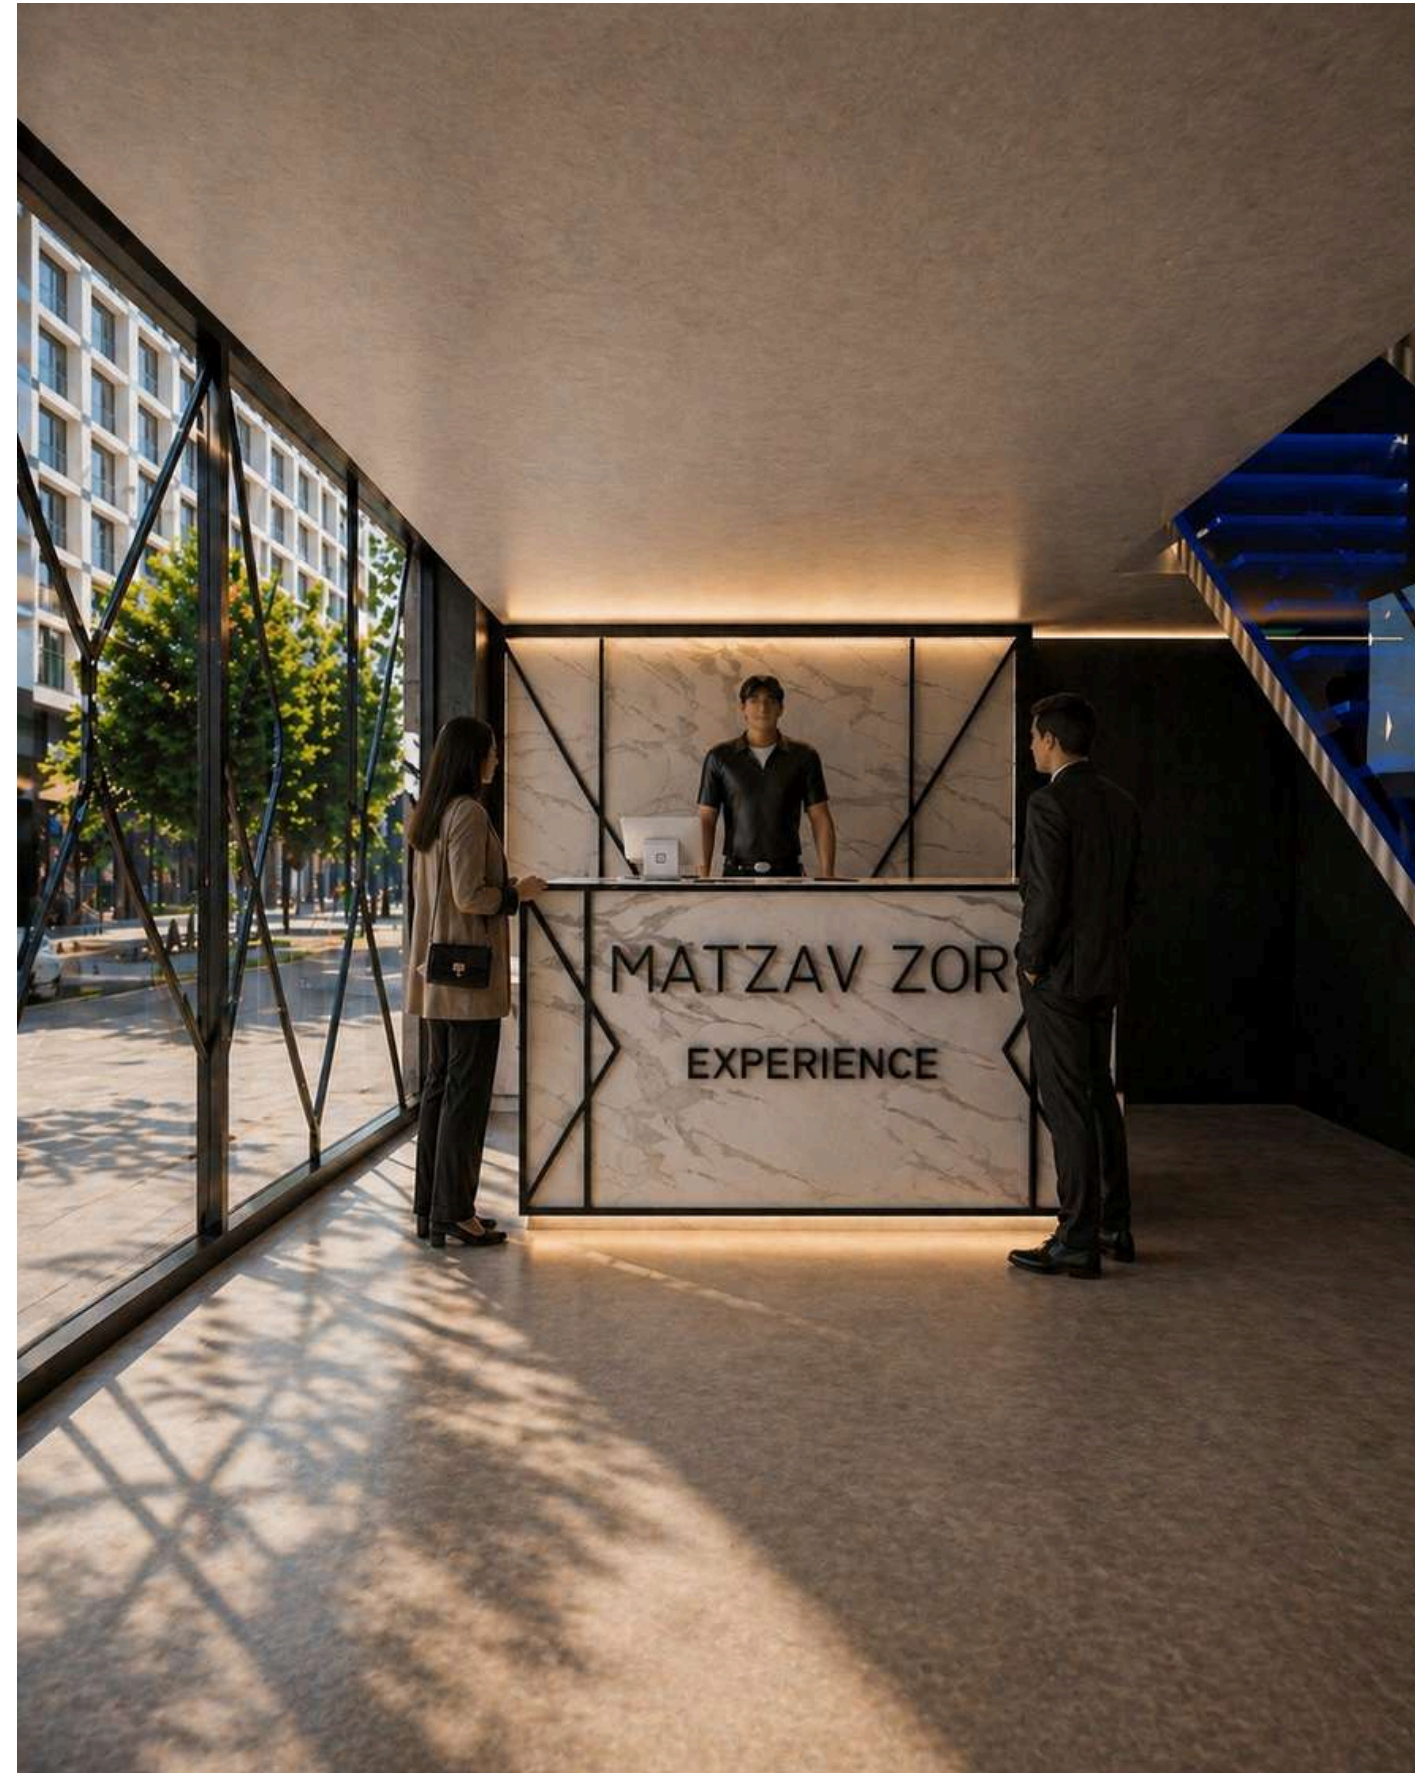

Visuel 3D




Visuel 3D




Mobilier concept





CROQUIS

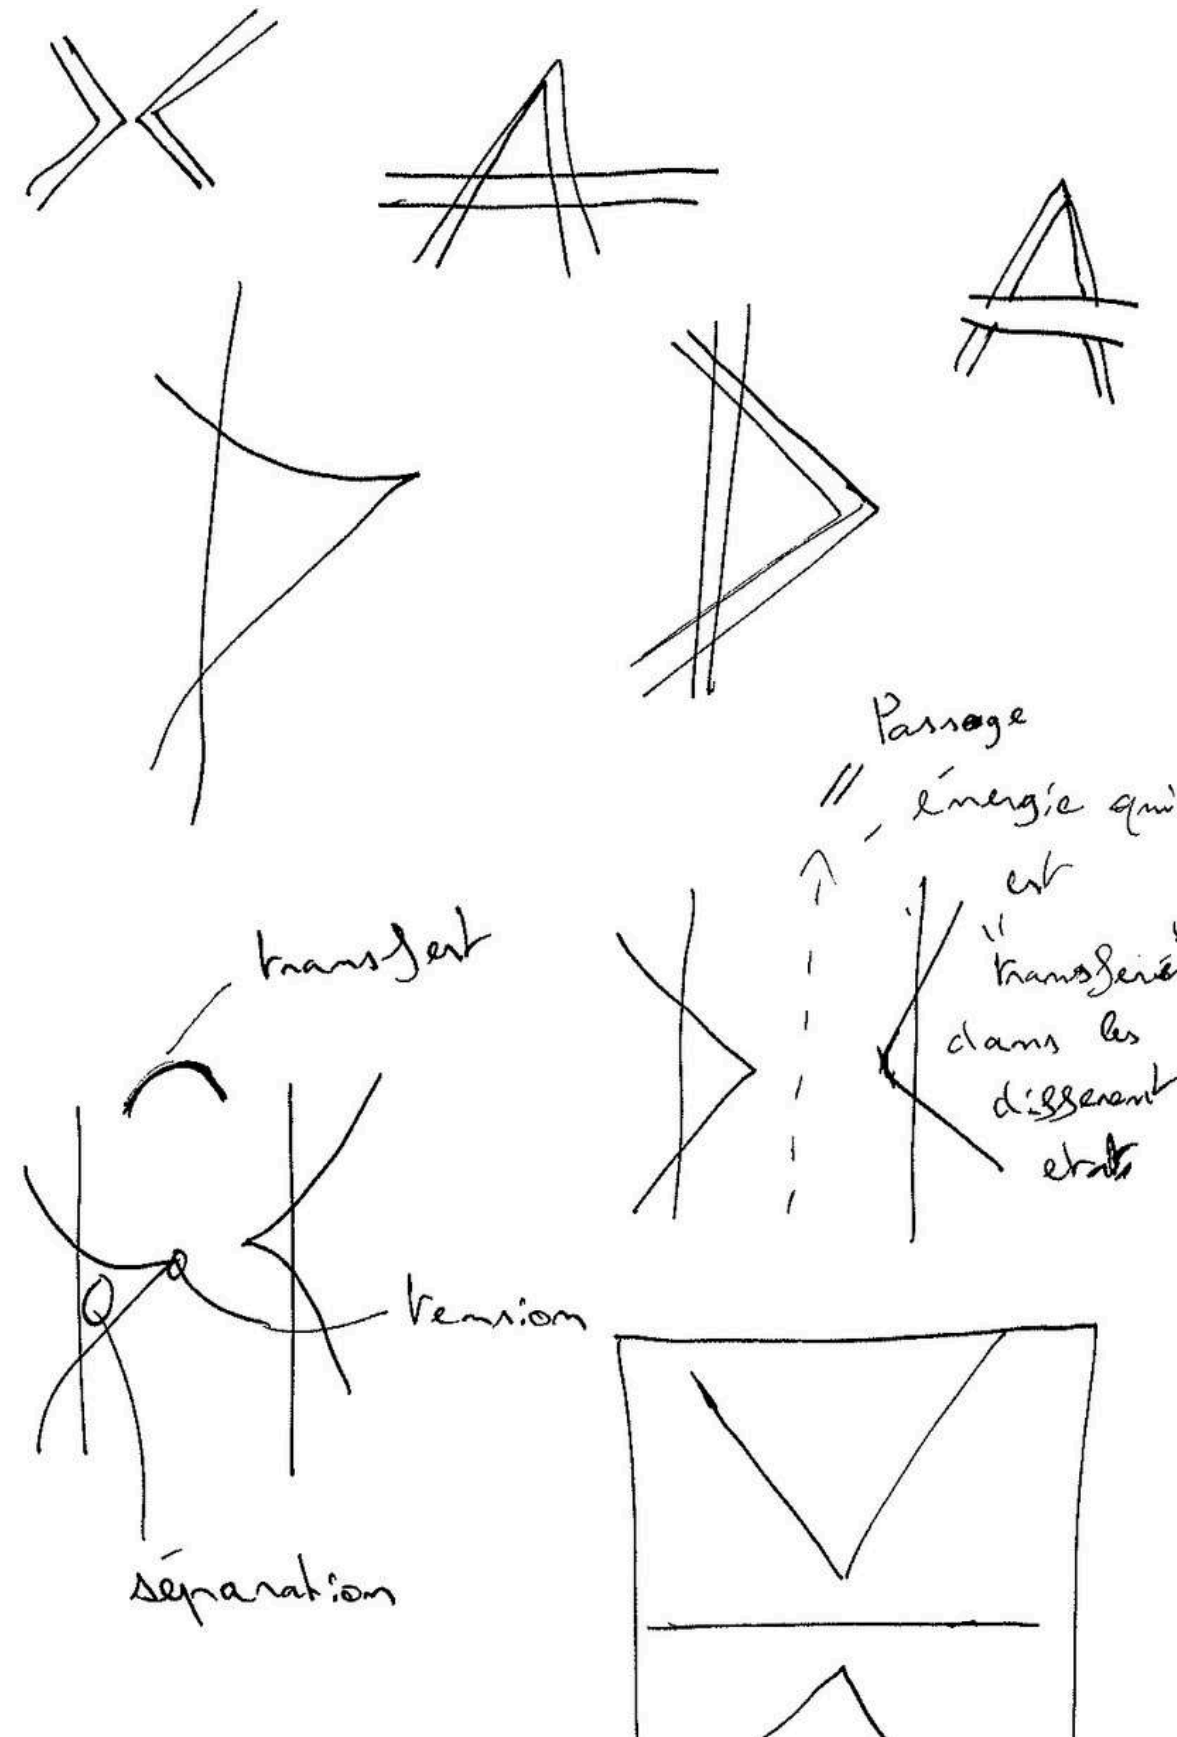


Détail cuisine

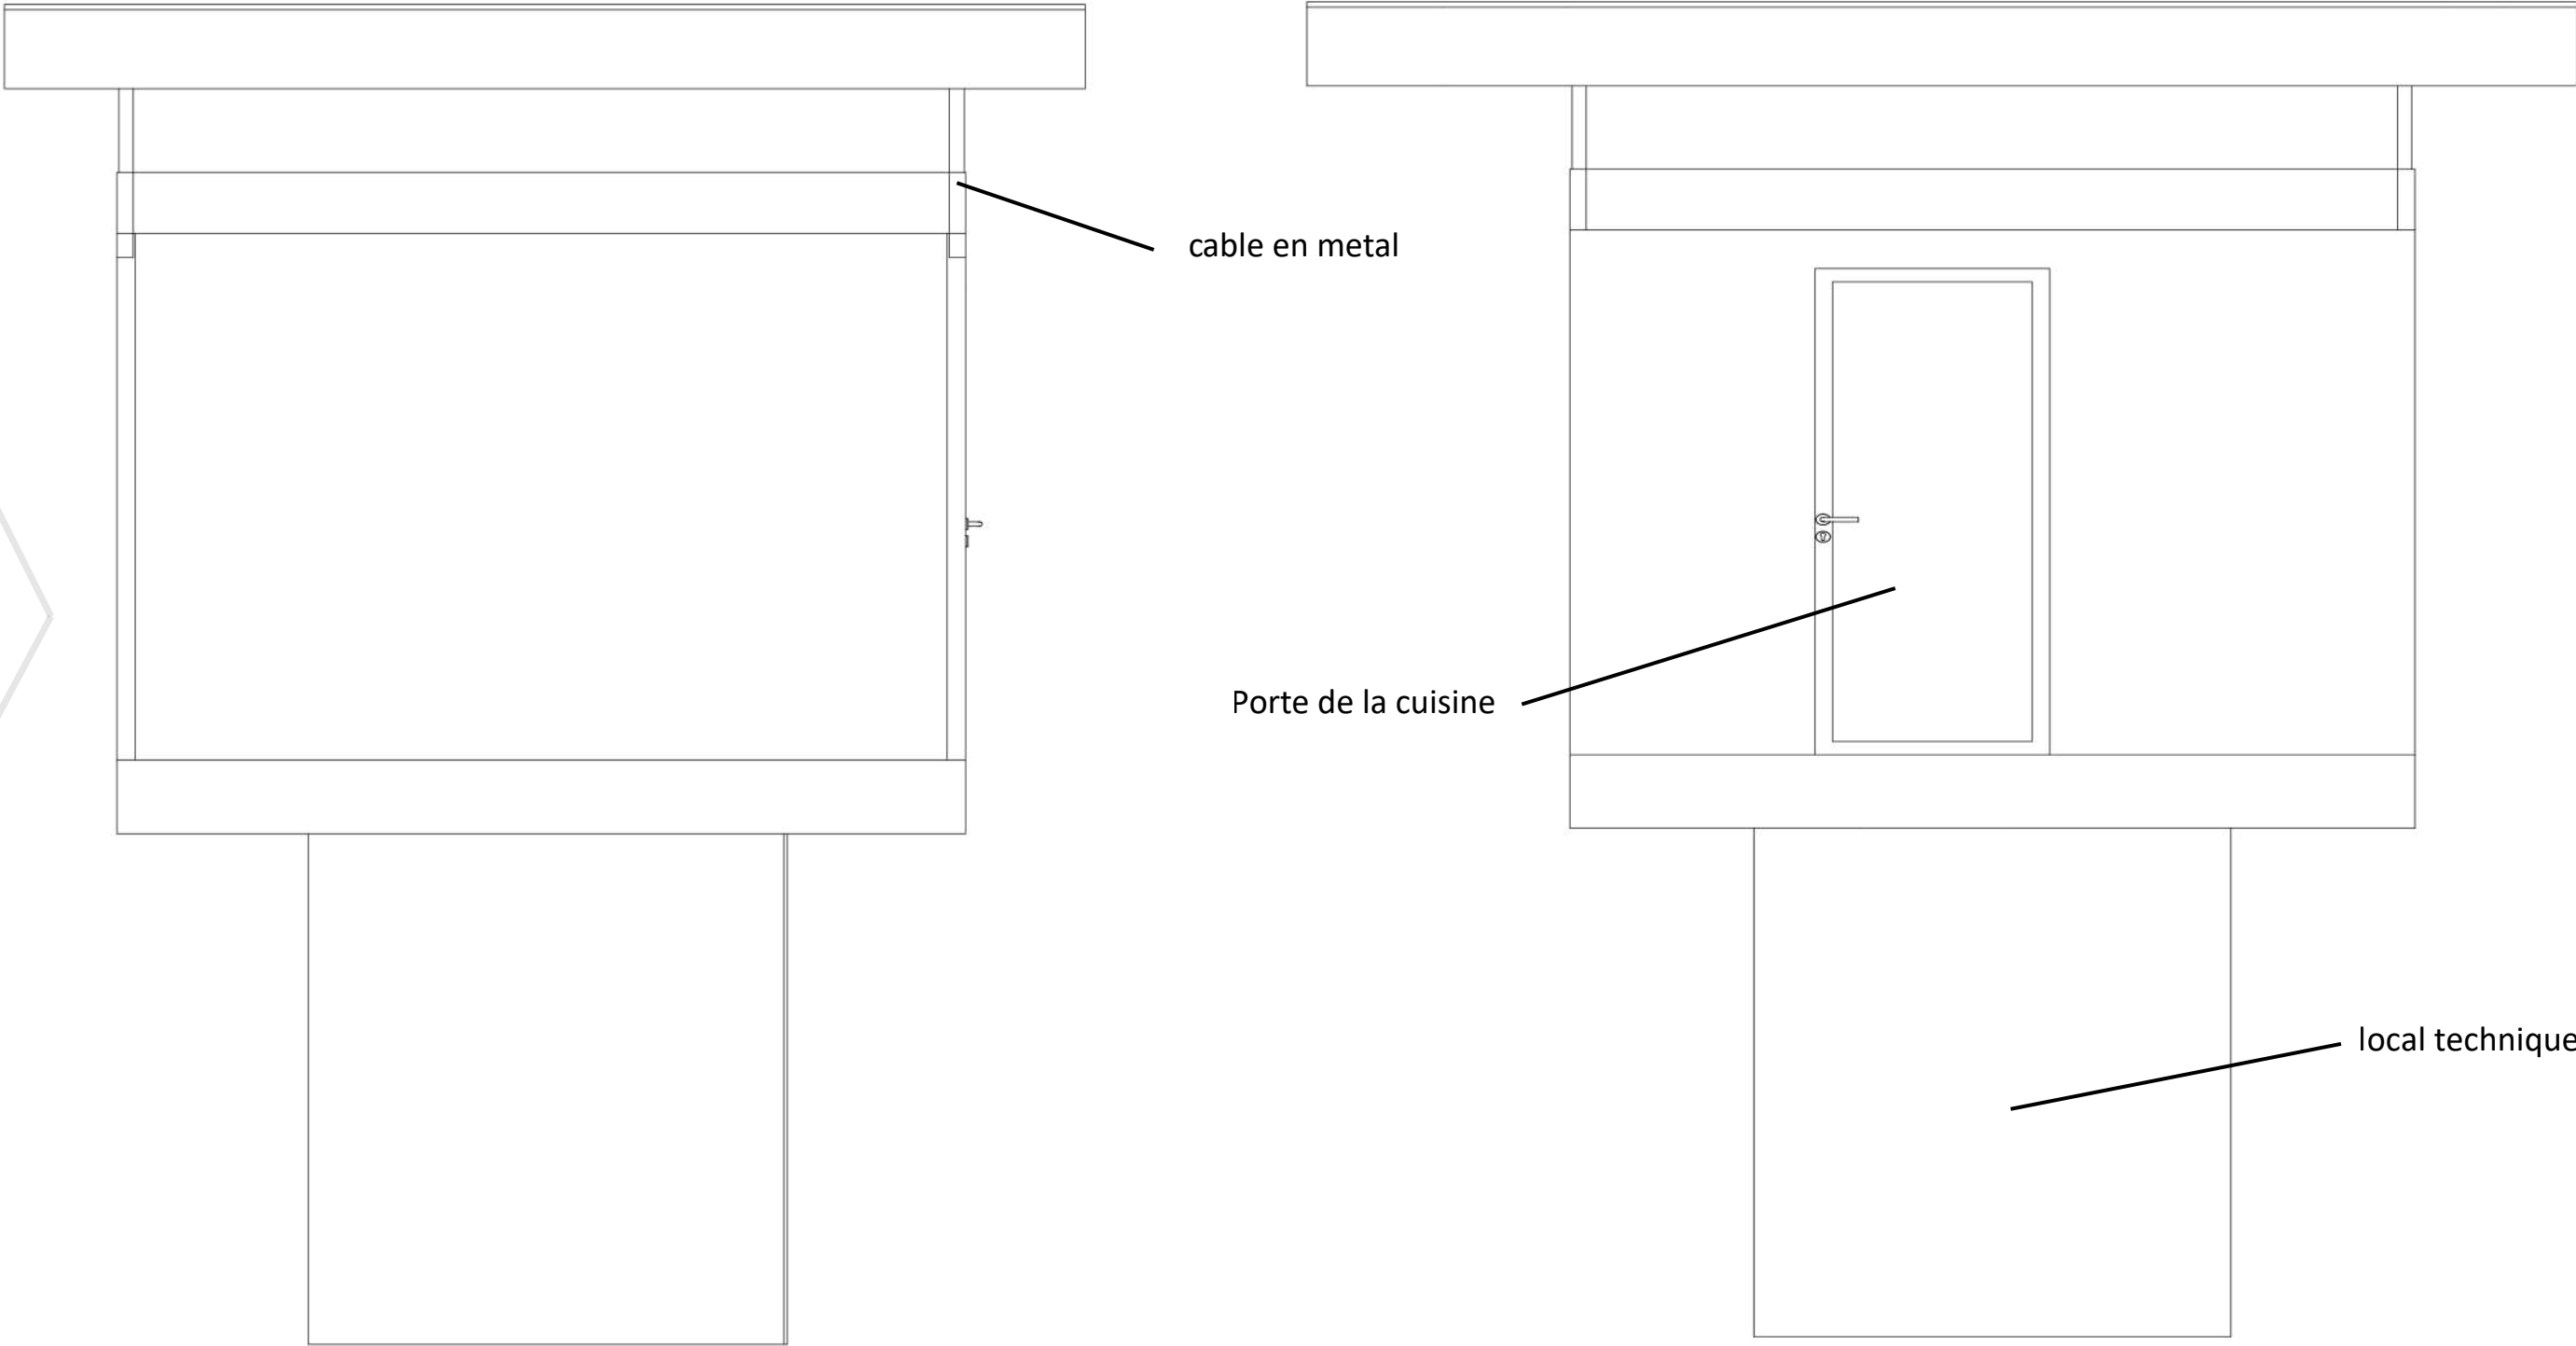

Détail chaise

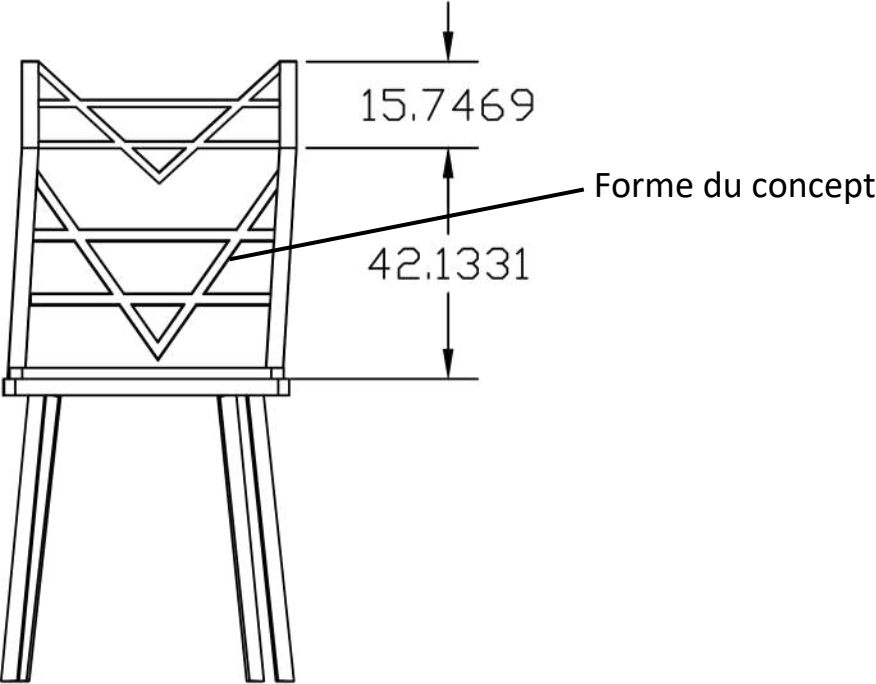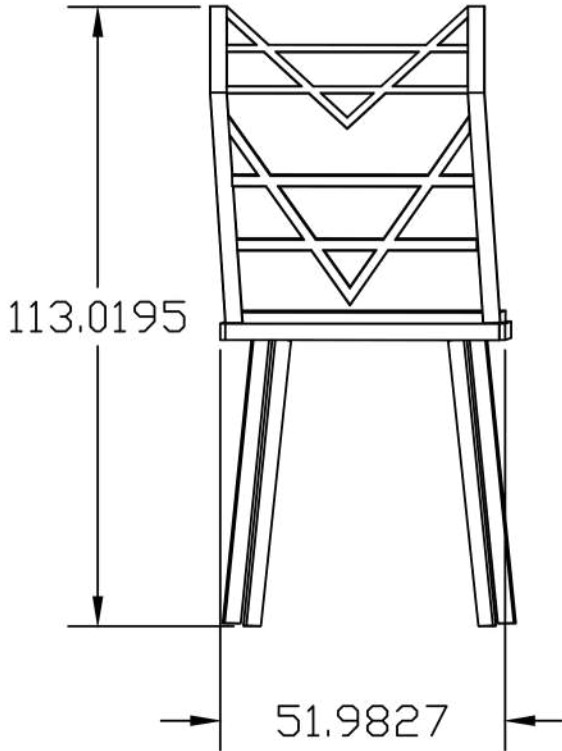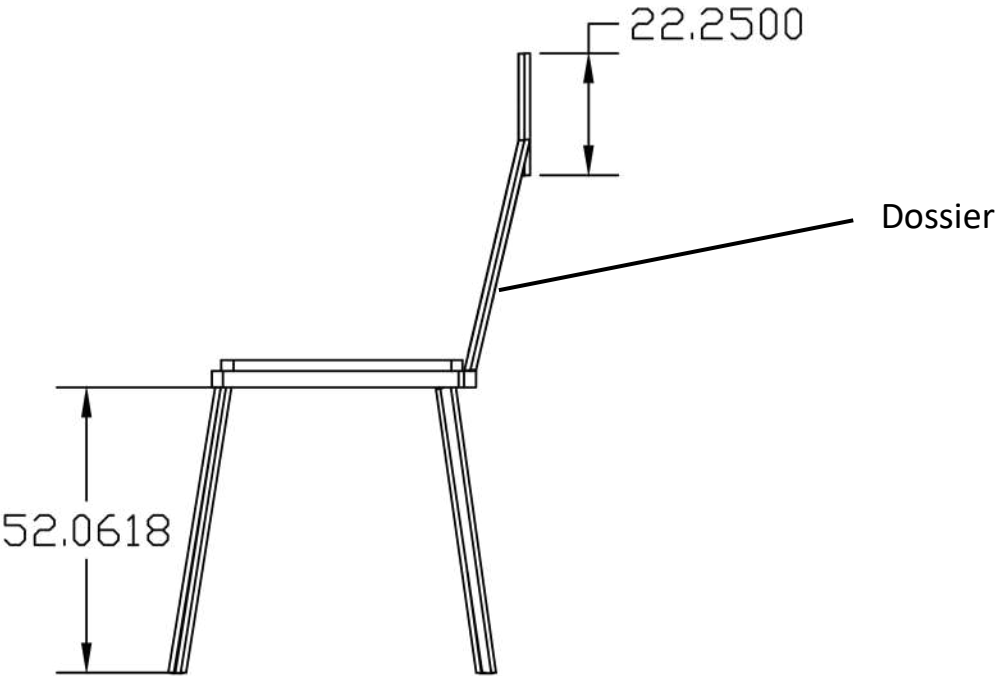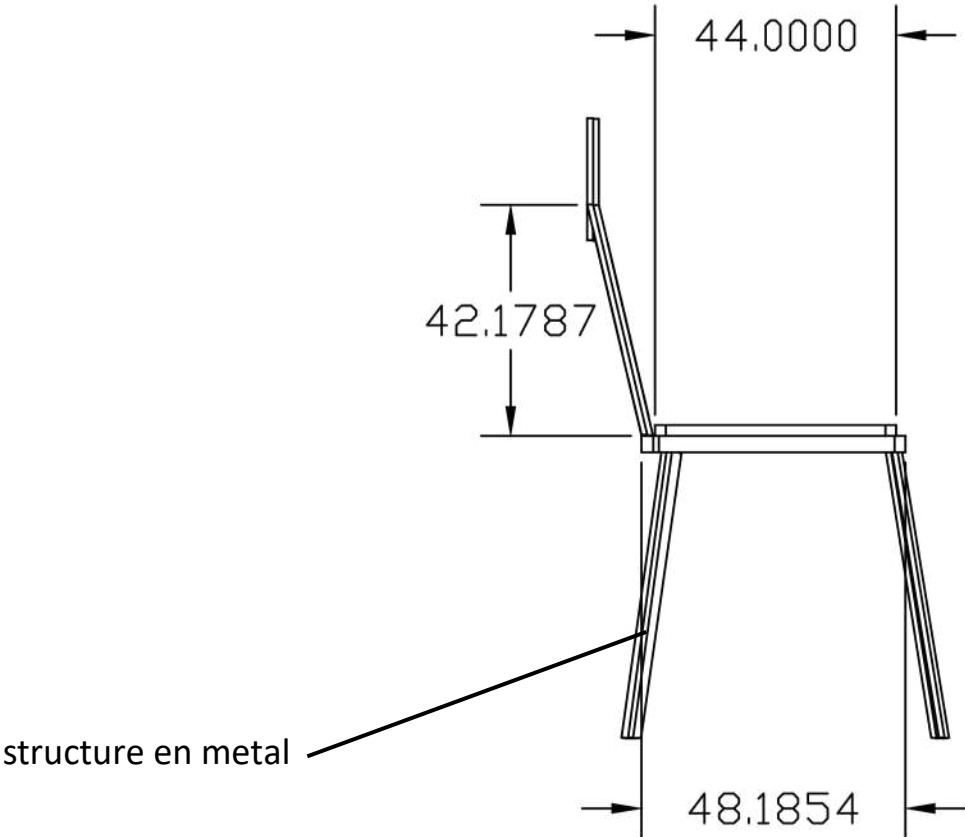

Détail banquette

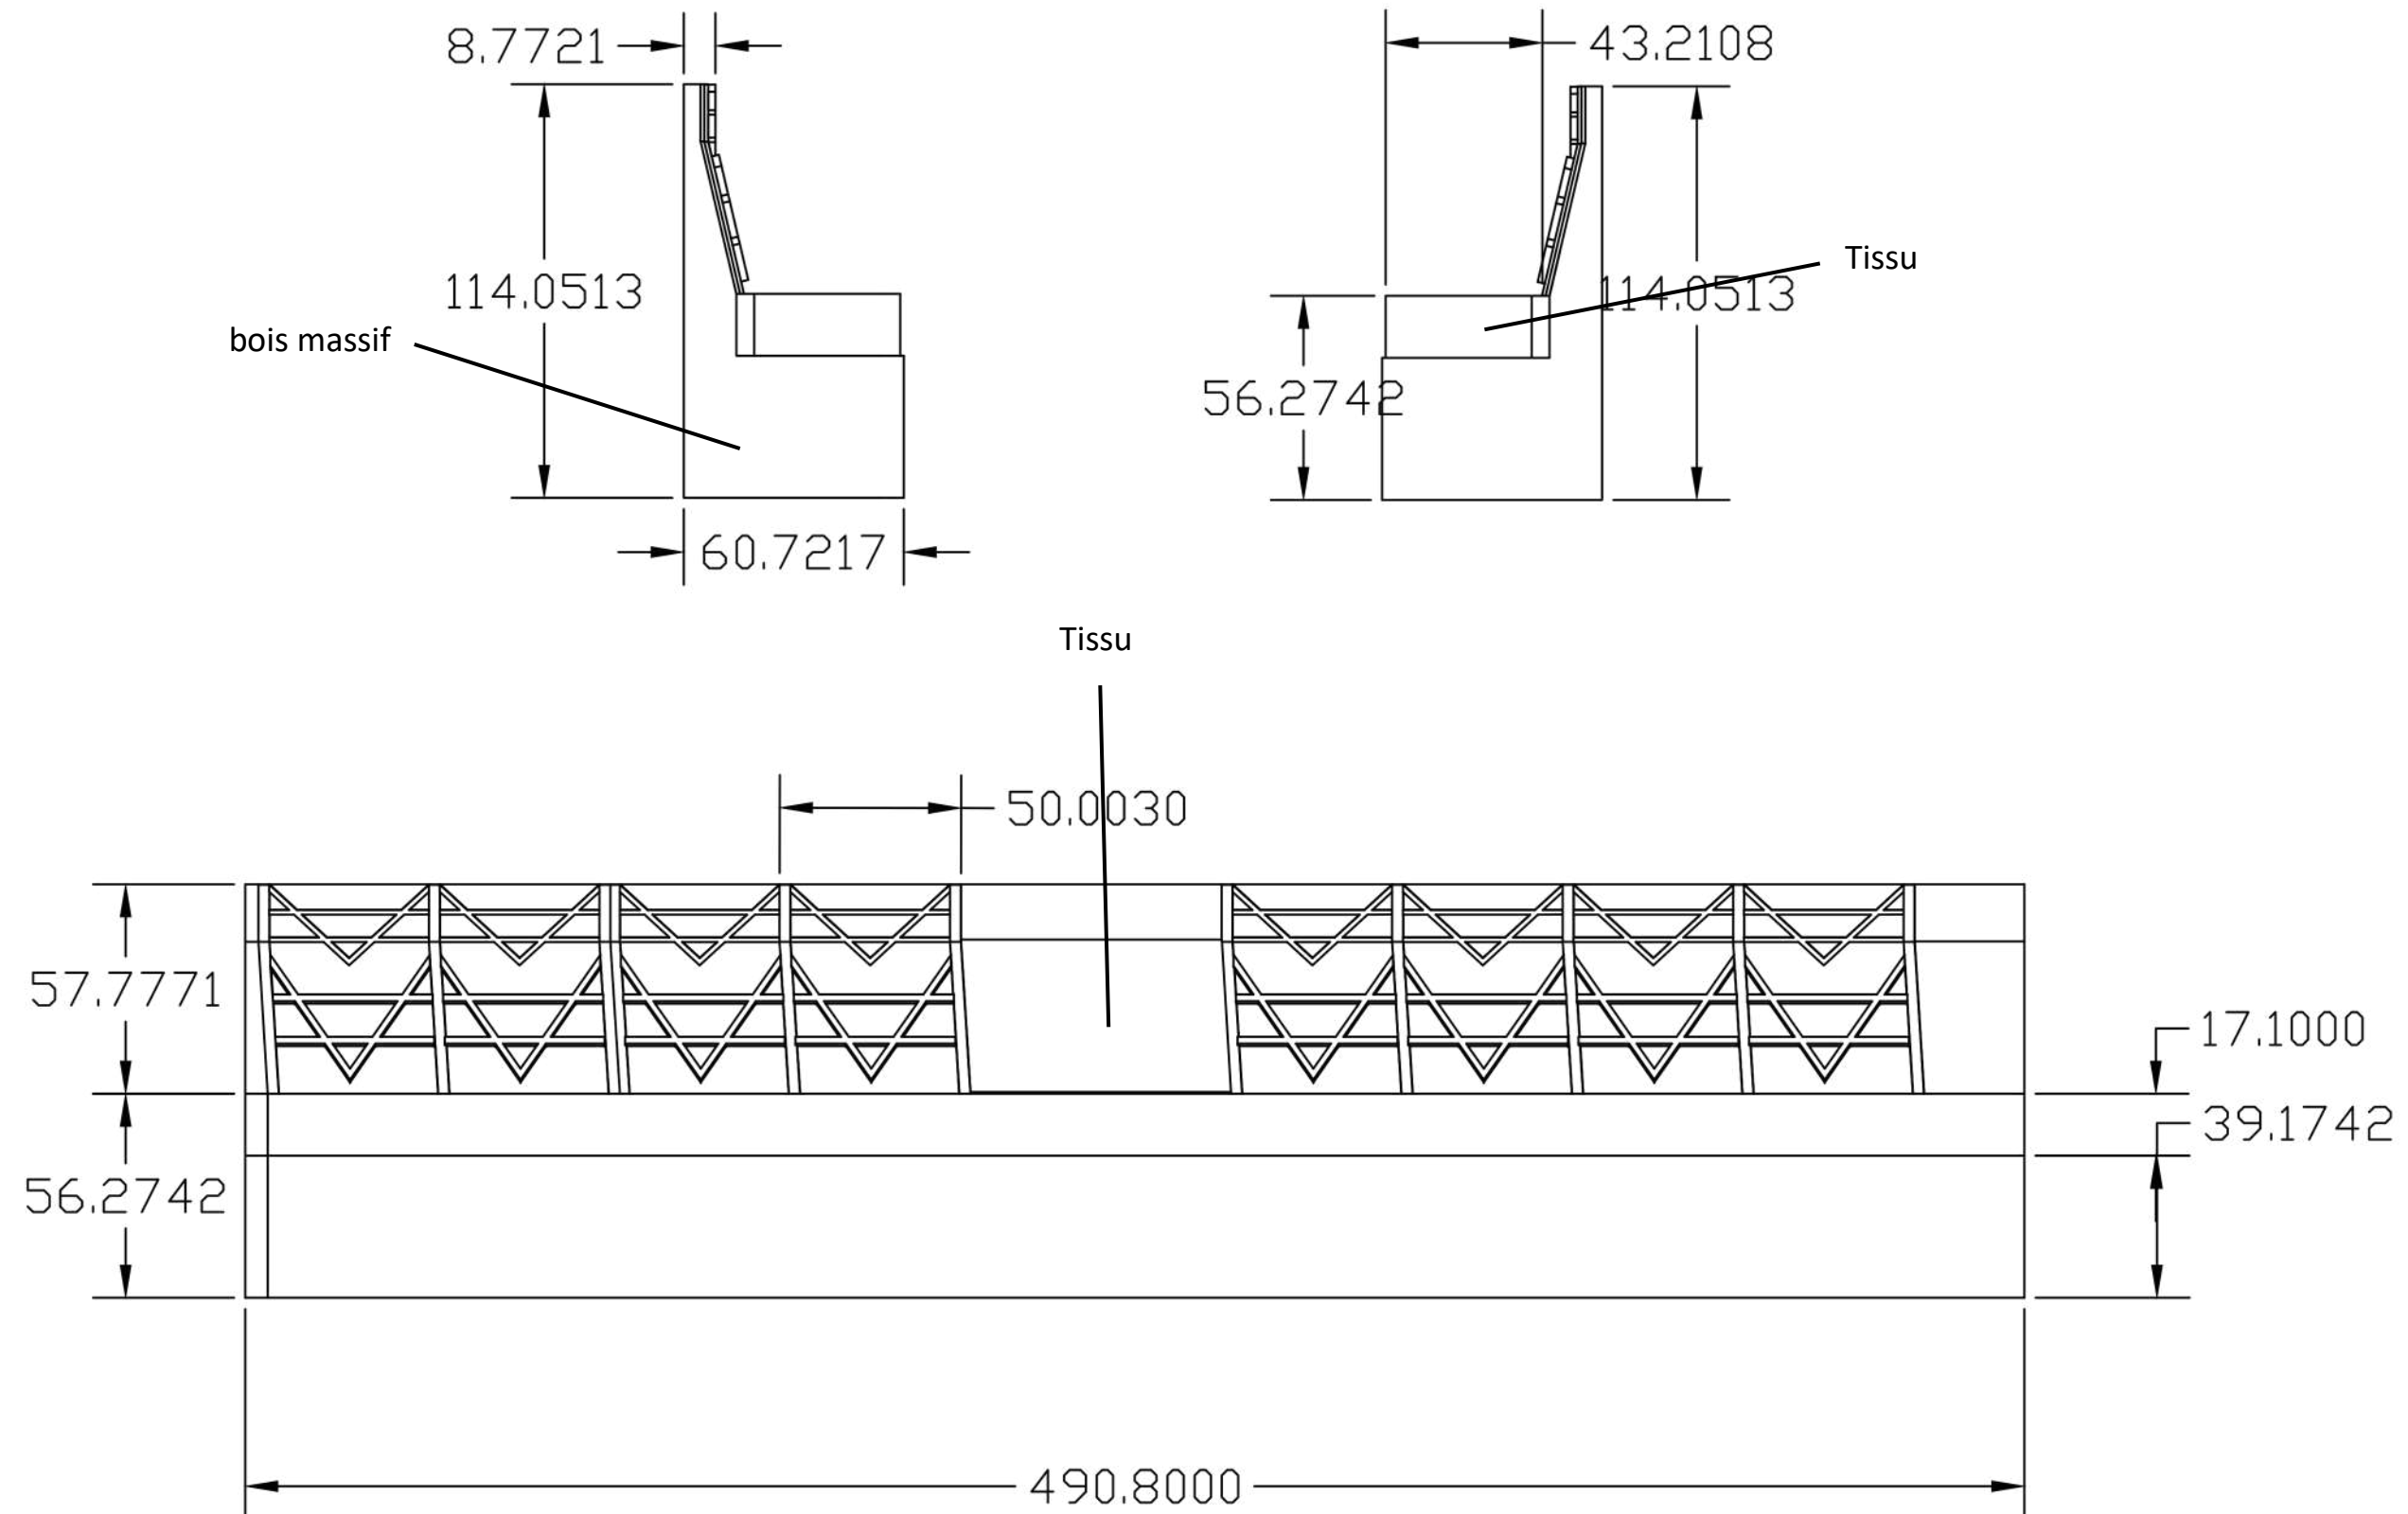

The background is a dark gray gradient. On the left and right sides, there are white geometric lines. On the left, a vertical line and a diagonal line intersect to form a right-angled triangle pointing towards the center. On the right, a vertical line and a diagonal line intersect to form a right-angled triangle pointing towards the center.

Merci

Alon Marec, Sahim Mohamed