

**B2 - Projet 3**

## **Extension et transformation d'un garage en Tiny house Airbnb**

6 avenue Eugène Godin, Melun (77000)

Alon Marec  
Alan distrophe

15/06/2026

# Sommaire

**01. Présentation du projet**

**02. Analyse et principes conceptuels**

**03. Dossier graphique extérieur**

**04. Dossier graphique intérieur**

**05. Dossier technique**

**06. DQE**

**07. Visualisations 3D**

# Présentation du projet

## 01. Note d'intention

### Relation intérieur / extérieur

- Grandes baies vitrées disposées sur les 2 faces donnant sur le jardin.

### Mobilier et espaces multifonctions intégrés

- Le **claustra** à panneaux rabattables structure les espaces en distinguant la zone nuit de l'espace d'appoint.
- Meuble sur toute la hauteur disponible.
- Optimisation des petits espaces grâce à l'organisation verticale.
- Le **lit escamotable** permet de gagner davantage d'espace
- Création d'une table à manger qui se rabat en un meuble existant.

## 02. Brief client

- Expérience Airbnb atypique pour les couples
- Continuité garage / jardin / tiny house
- Optimisation des petits espaces
- Maximisation de la lumière naturelle
- Matériaux respectueux de l'environnement
- Valoriser un garage inutilisé

## 03. Contrainte du projet

- PLU (zone U)
- Accès étroit / enclavé au site
- Vis-à-vis
- Emprise au sol limitée
- Budget : 50 - 70 k

# Références

A45 . BIG / Klein



Grande baie vitrée

Relation intérieur / extérieur

Garden Studio. Studio abacaxi




Rangement intégré

Lit escamotable





# SWOT

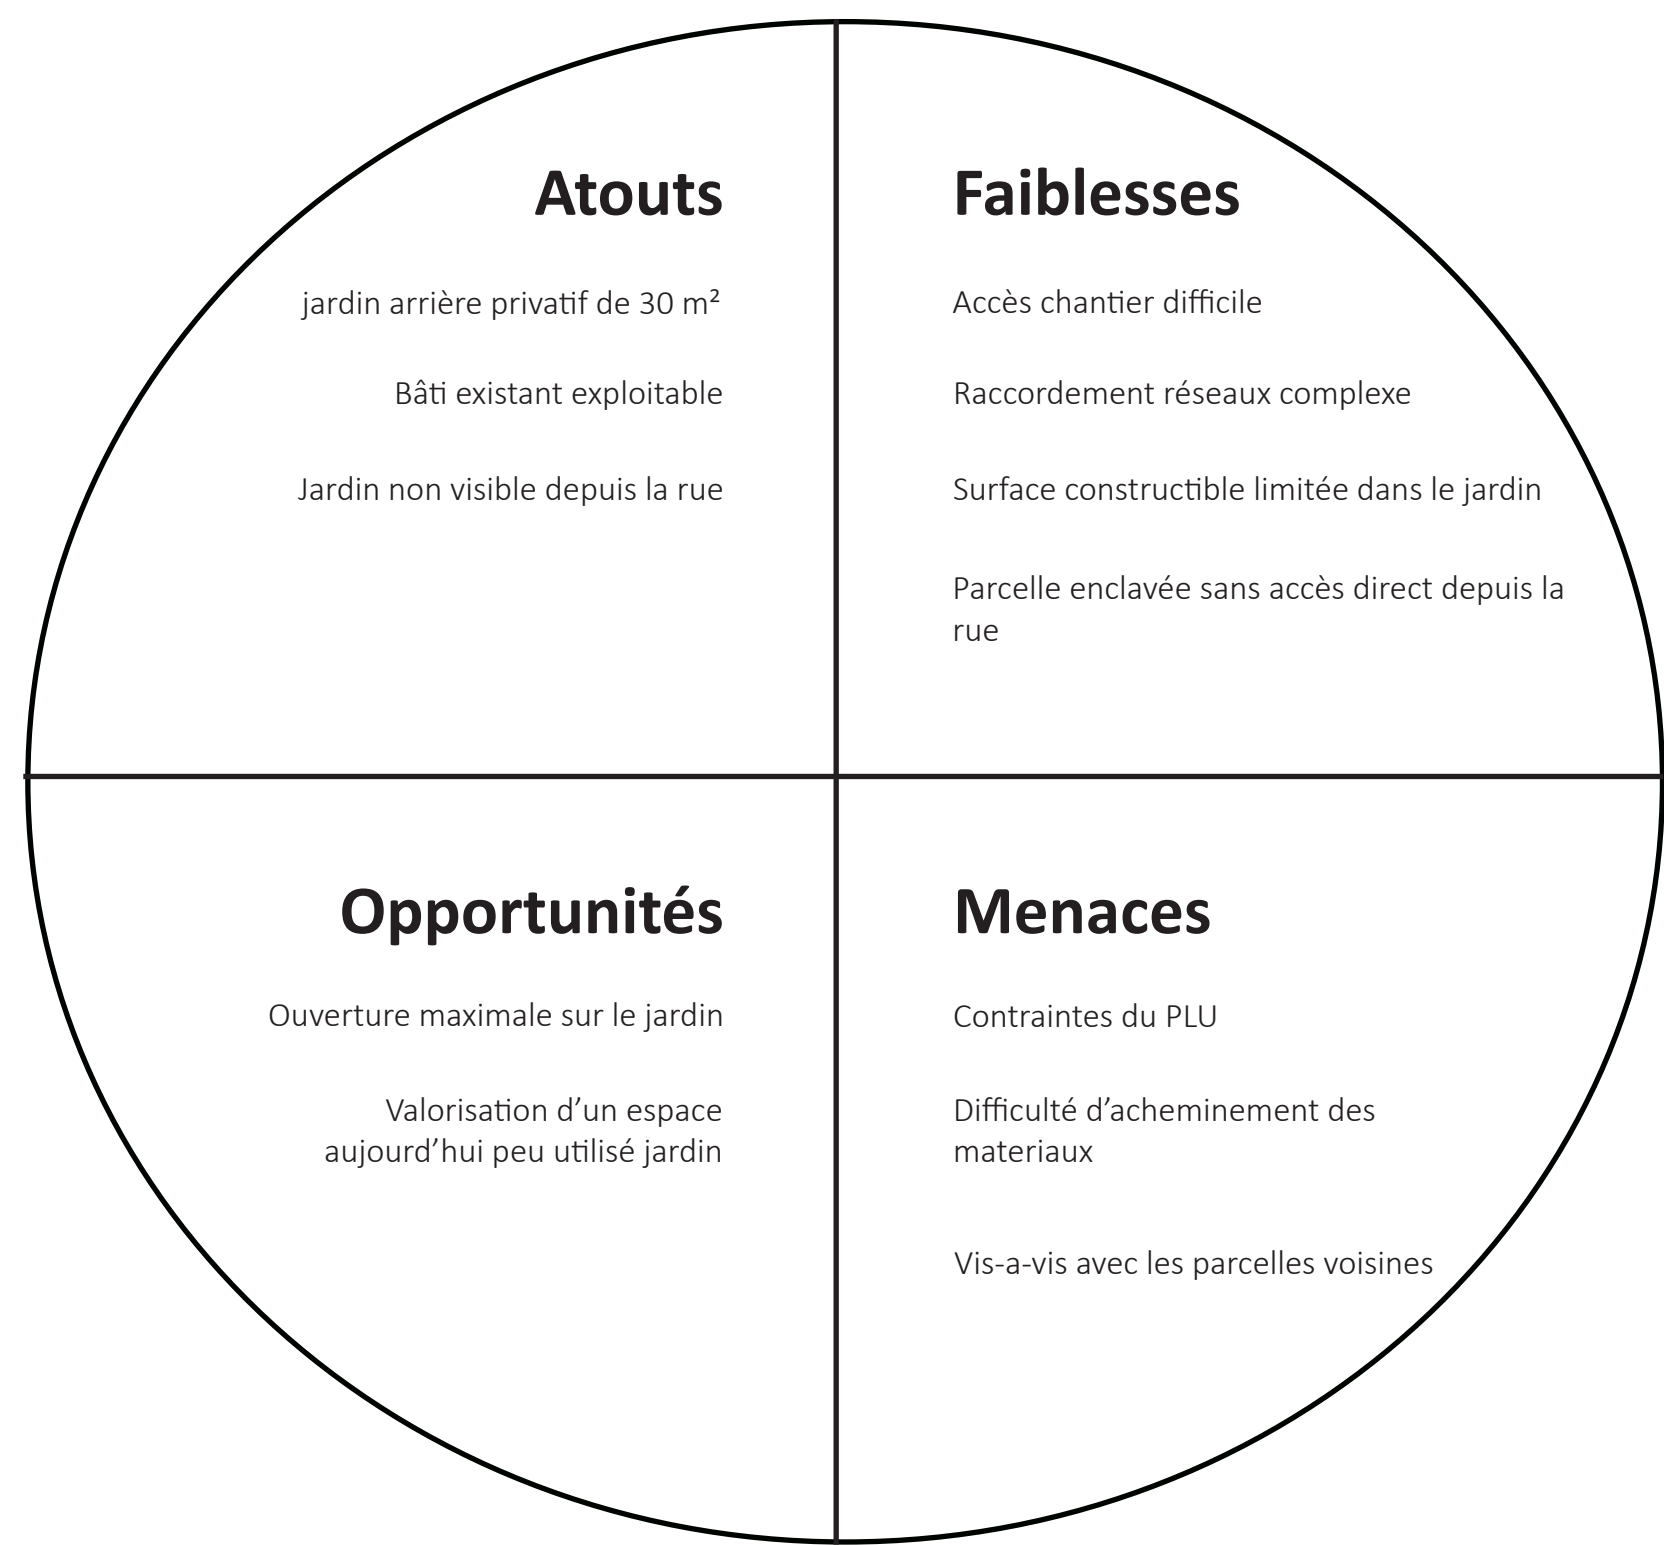

Le diagnostic met en évidence un site calme mais enclavé.  
Le projet s'oriente donc vers une micro-architecture légère, réversible et ouverte sur le jardin.

Plan de Masse

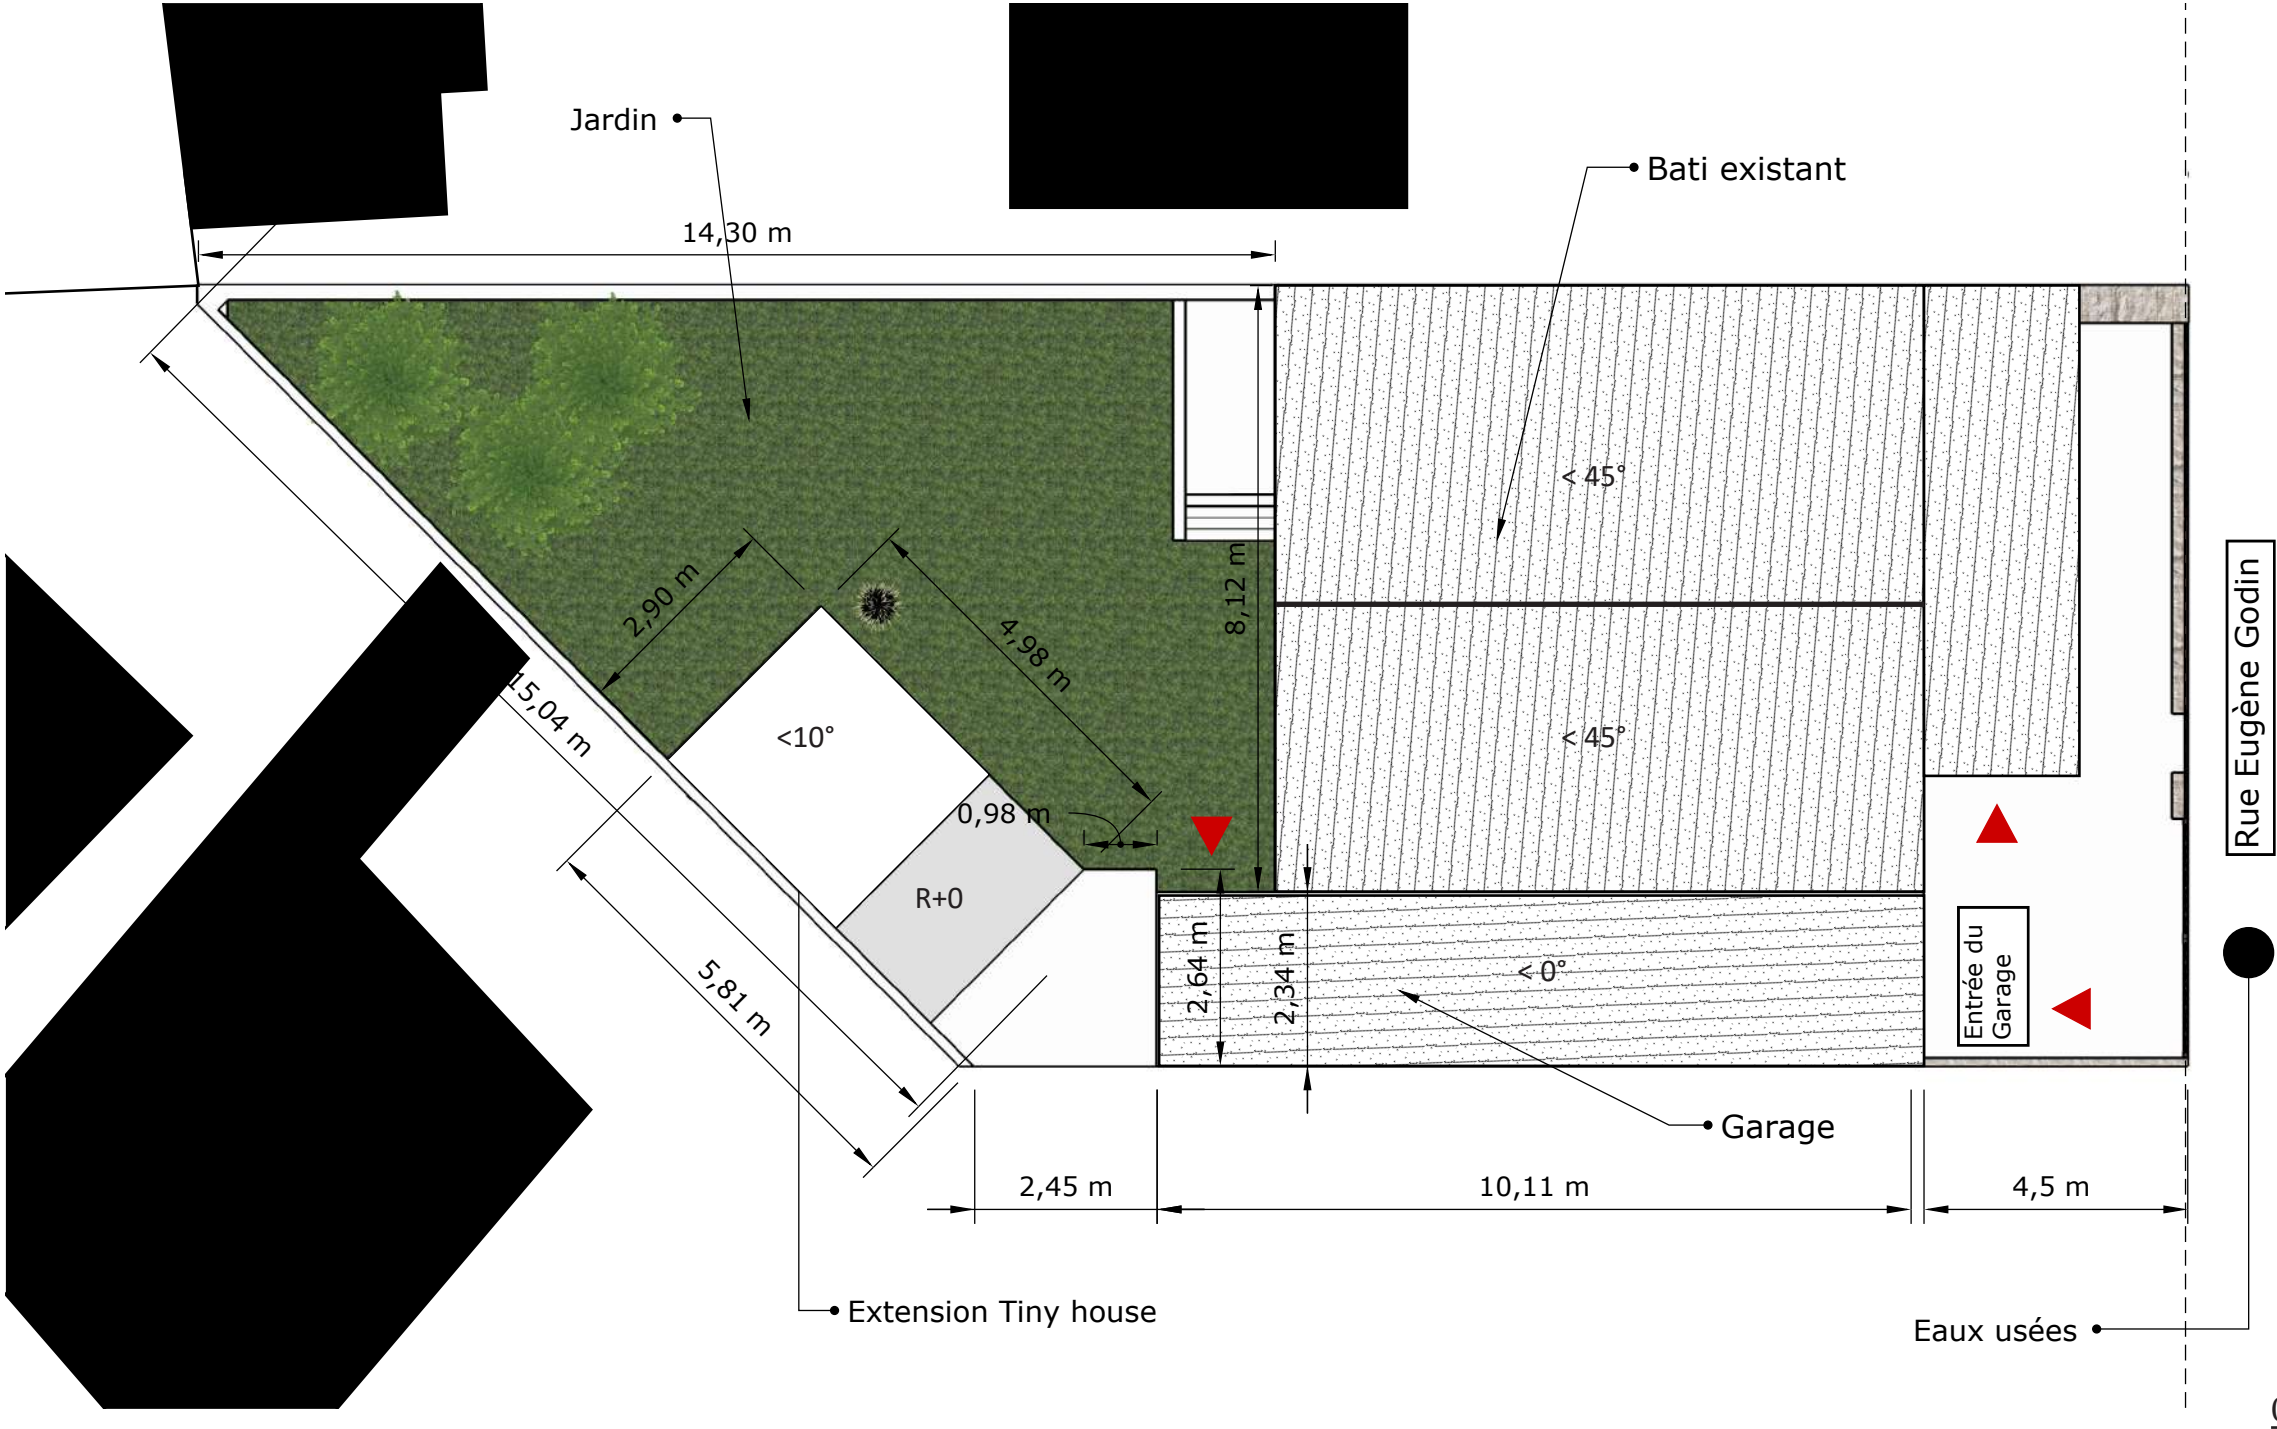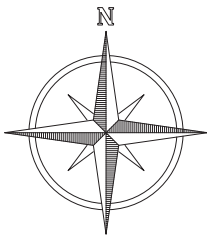



|                                                                |                      |                                              |  |                                                                                                |                              |
|----------------------------------------------------------------|----------------------|----------------------------------------------|--|------------------------------------------------------------------------------------------------|------------------------------|
| <b>Ouvrage</b><br>Tiny House<br>6 av Eugène Godin, 77000 Melun |                      | <b>Maitre d'ouvrage</b><br>Yacine Hadj Hamou |  | <b>Maitre D'oeuvre</b><br>Marec Alon / Distrophe Alan<br>12 rue Anatole France ,92000 Nanterre |                              |
| <b>Titre</b><br>Plan de masse                                  | <b>Echelle</b><br>A3 | <b>Format</b><br>1/100                       |  | <b>Date</b><br>15/06/2026                                                                      | <b>Etat du projet</b><br>APD |

# Tableau des surfaces

| Tableau des surfaces                                                                         |          |
|----------------------------------------------------------------------------------------------|----------|
| Surface plancher garage + extension (au-dessus de 1,80m, sans épaisseur des murs extérieurs) | 36,45 m2 |
| Emprise au sol de l'extension (bâti + débord toiture)                                        | 20,17 m2 |
| Surface pleine terre à l'échelle de la parcelle                                              | 72 m2    |
| Emprise au sol totale a l'échelle de la parcelle                                             | 44,18 m2 |

FACADE JARDIN



FACADE DE LA NOUVELLE EXTENTION VUE COTER JARDIN

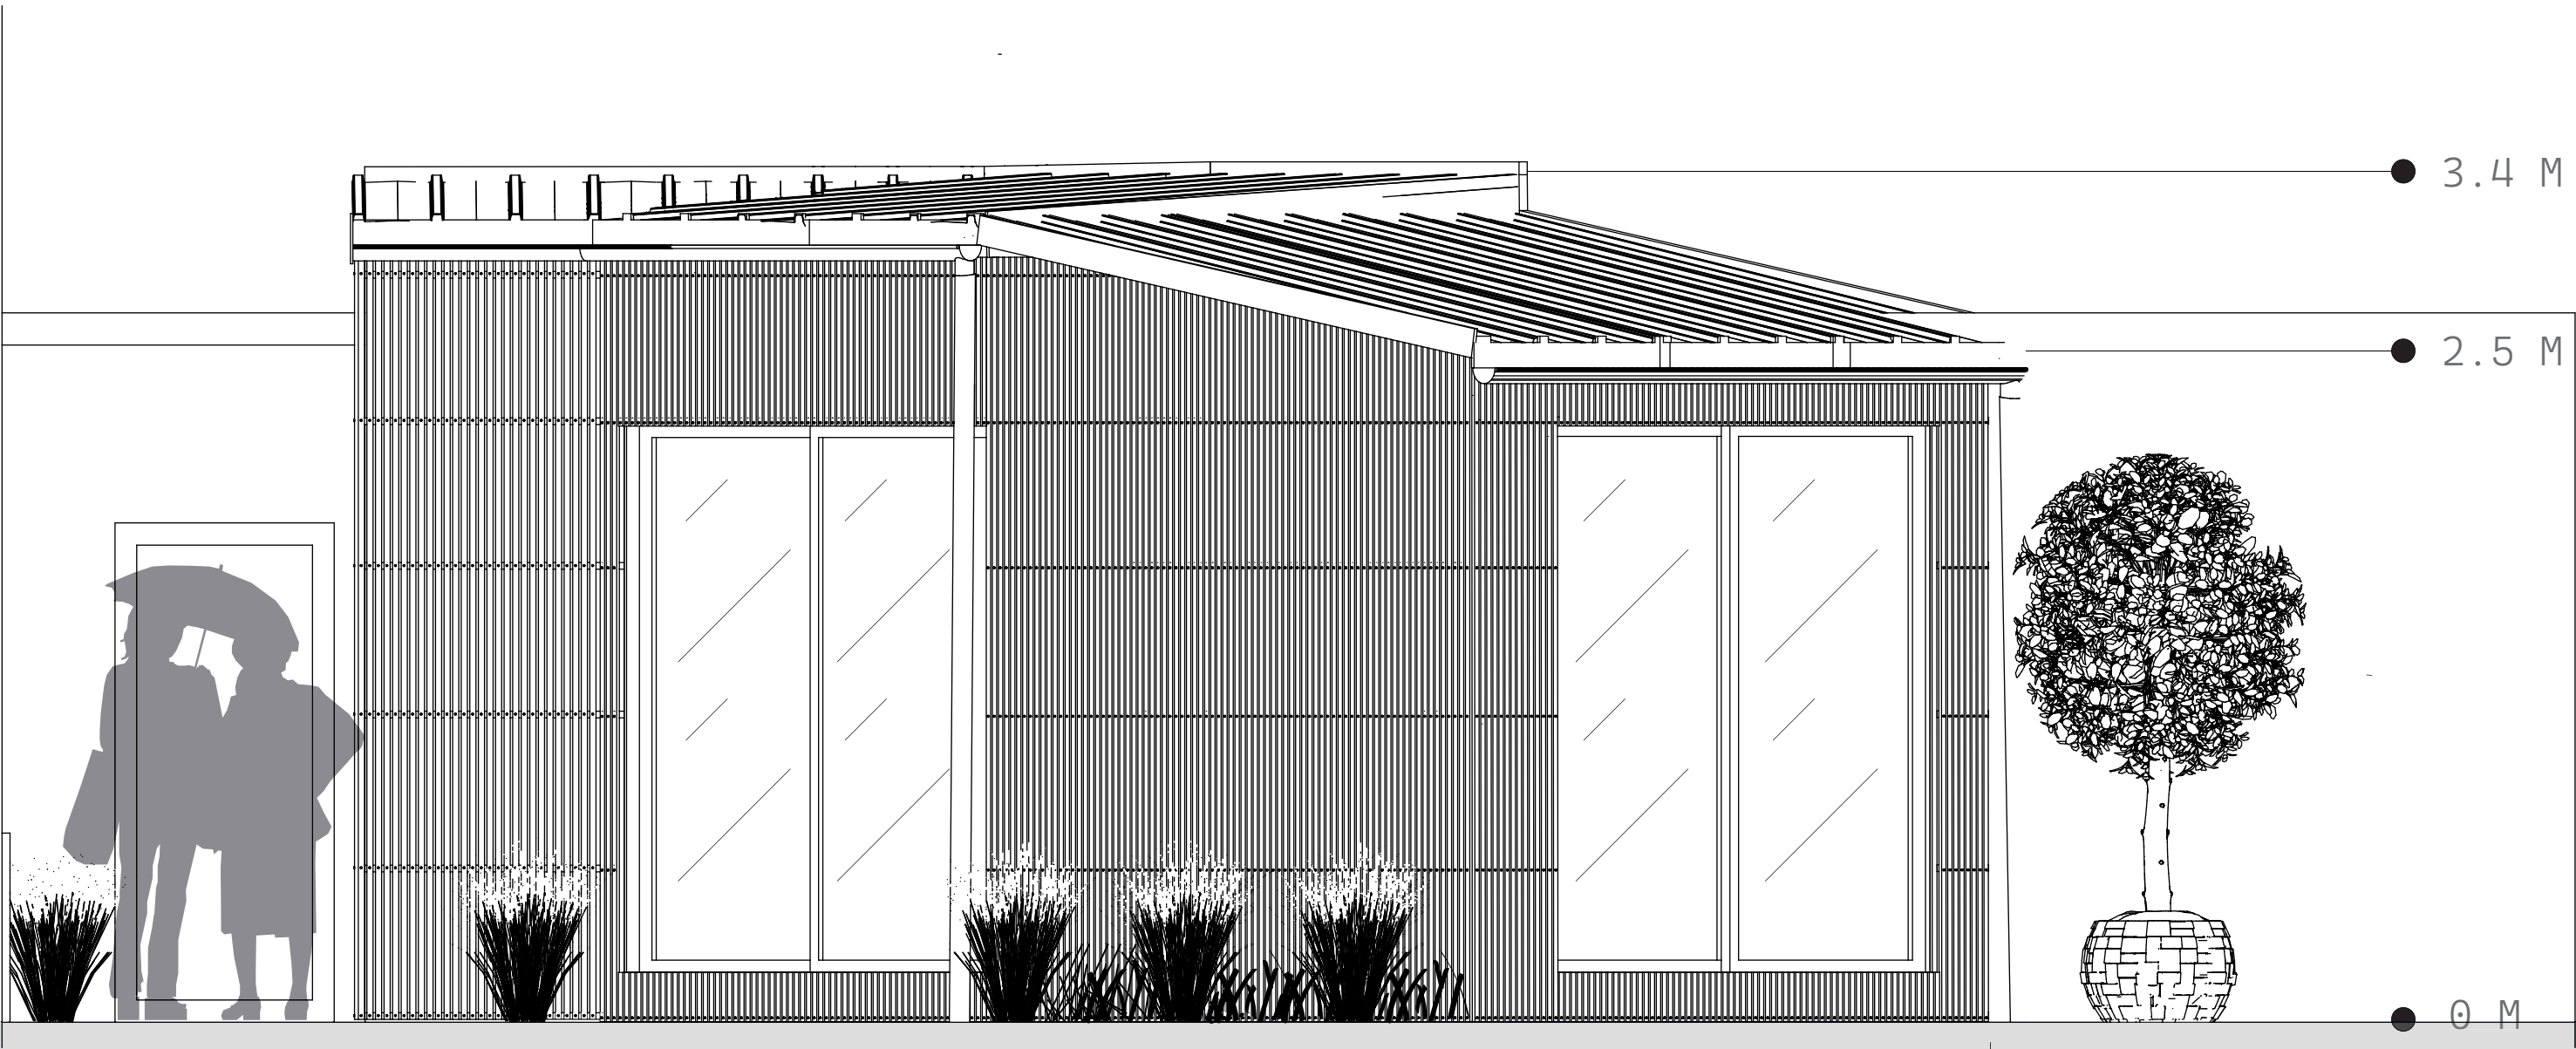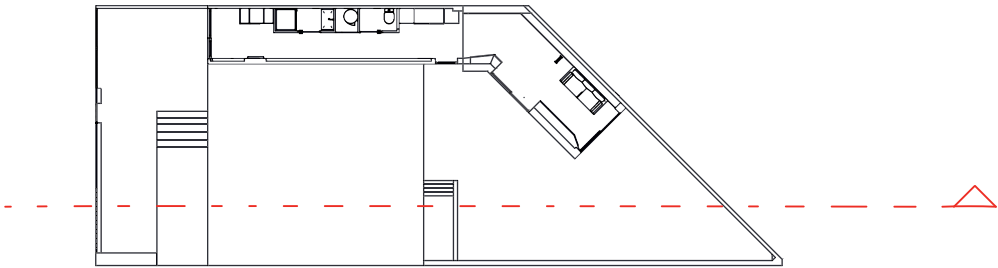

EXISTANT

PROJET

Plan projeté

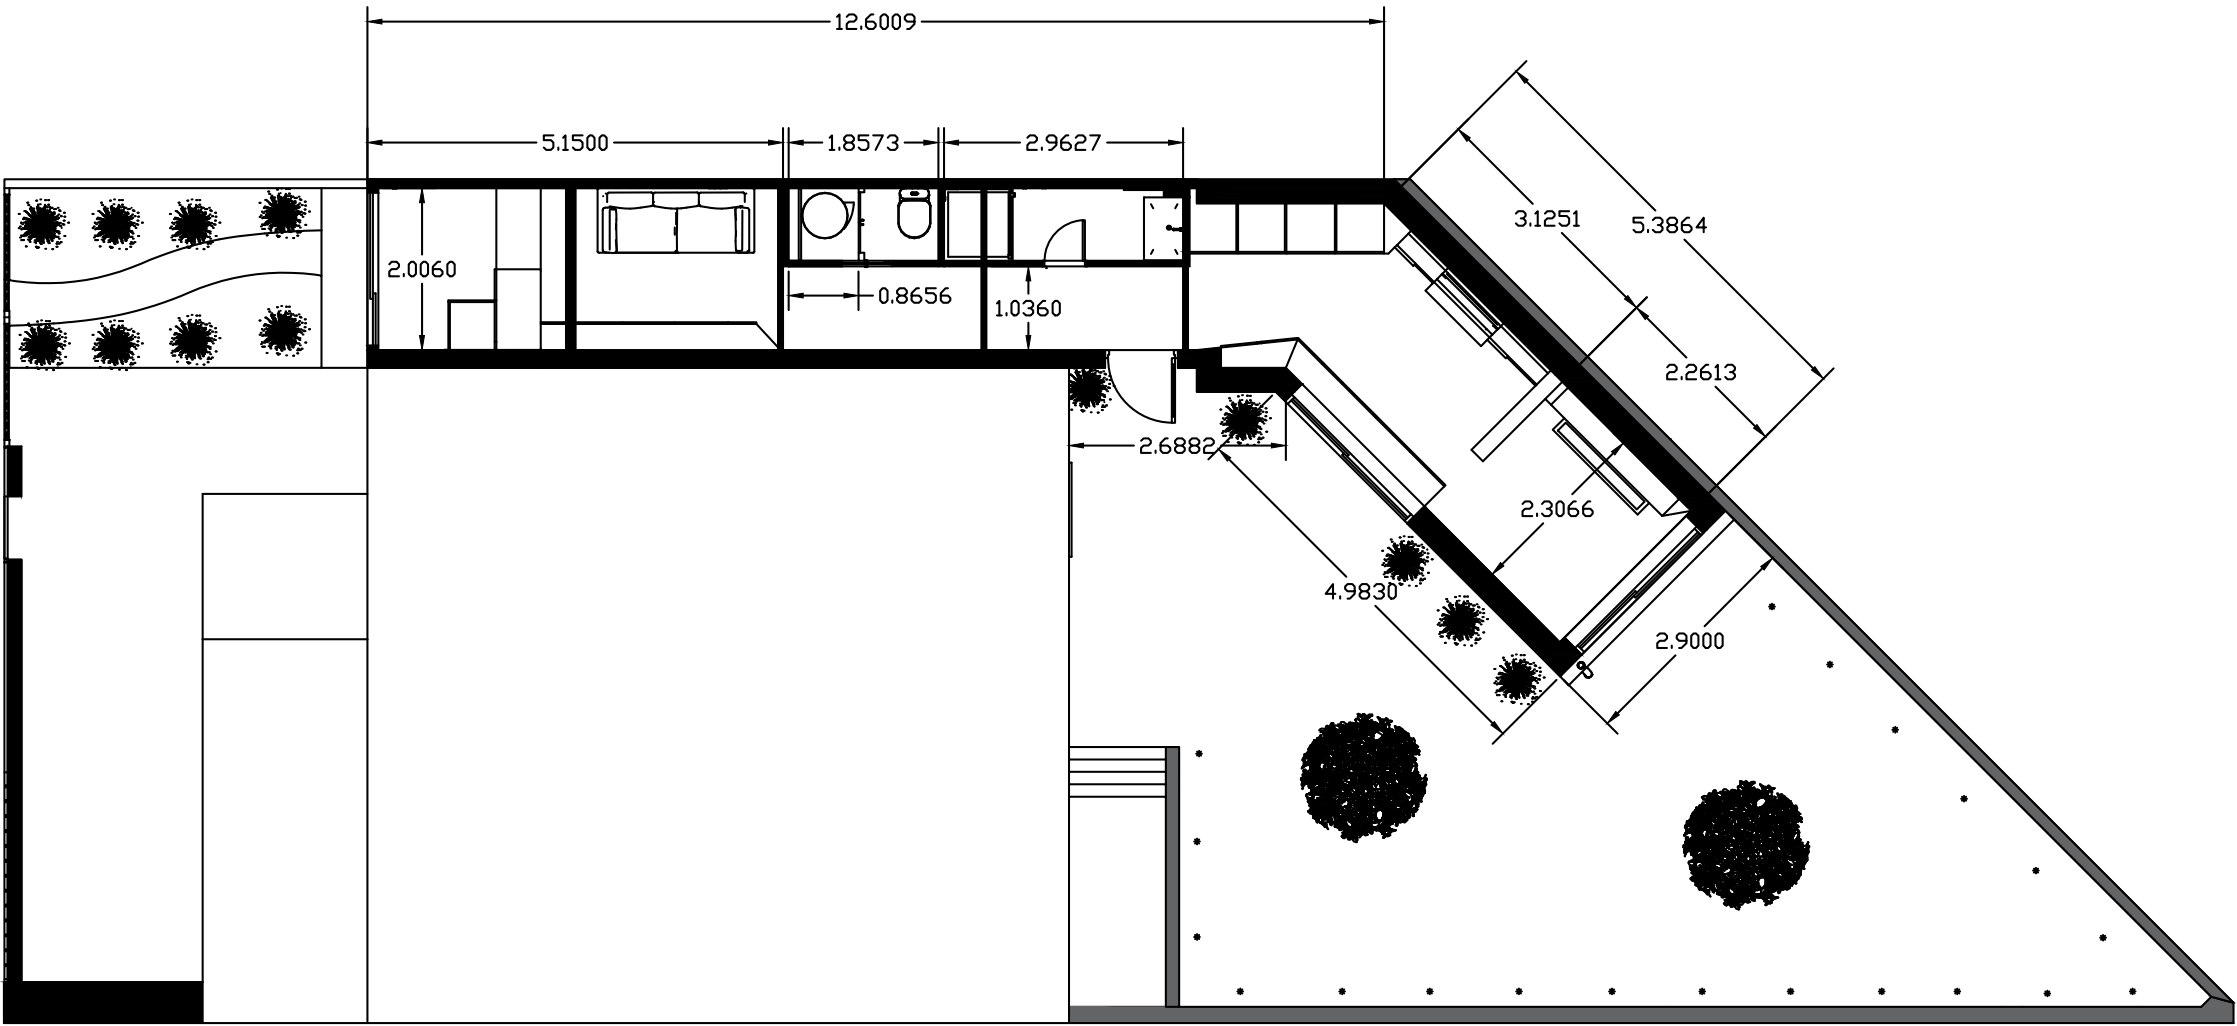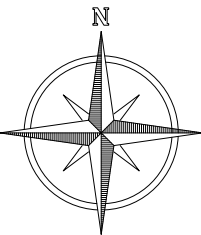


0 1

|                                                                |  |                                              |                        |                                                                                                |                              |
|----------------------------------------------------------------|--|----------------------------------------------|------------------------|------------------------------------------------------------------------------------------------|------------------------------|
| <b>Ouvrage</b><br>Tiny House<br>6 av Eugène Godin, 77000 Melun |  | <b>Maitre d'ouvrage</b><br>Yacine Hadj Hamou |                        | <b>Maitre d'oeuvre</b><br>Marec Alon / Distrophe Alan<br>12 rue Anatole France ,92000 Nanterre |                              |
| <b>Titre</b><br>Plan projeté                                   |  | <b>Echelle</b><br>A3                         | <b>Format</b><br>1/100 | <b>Date</b><br>15/06/2026                                                                      | <b>Etat du projet</b><br>APD |




Coupe AA

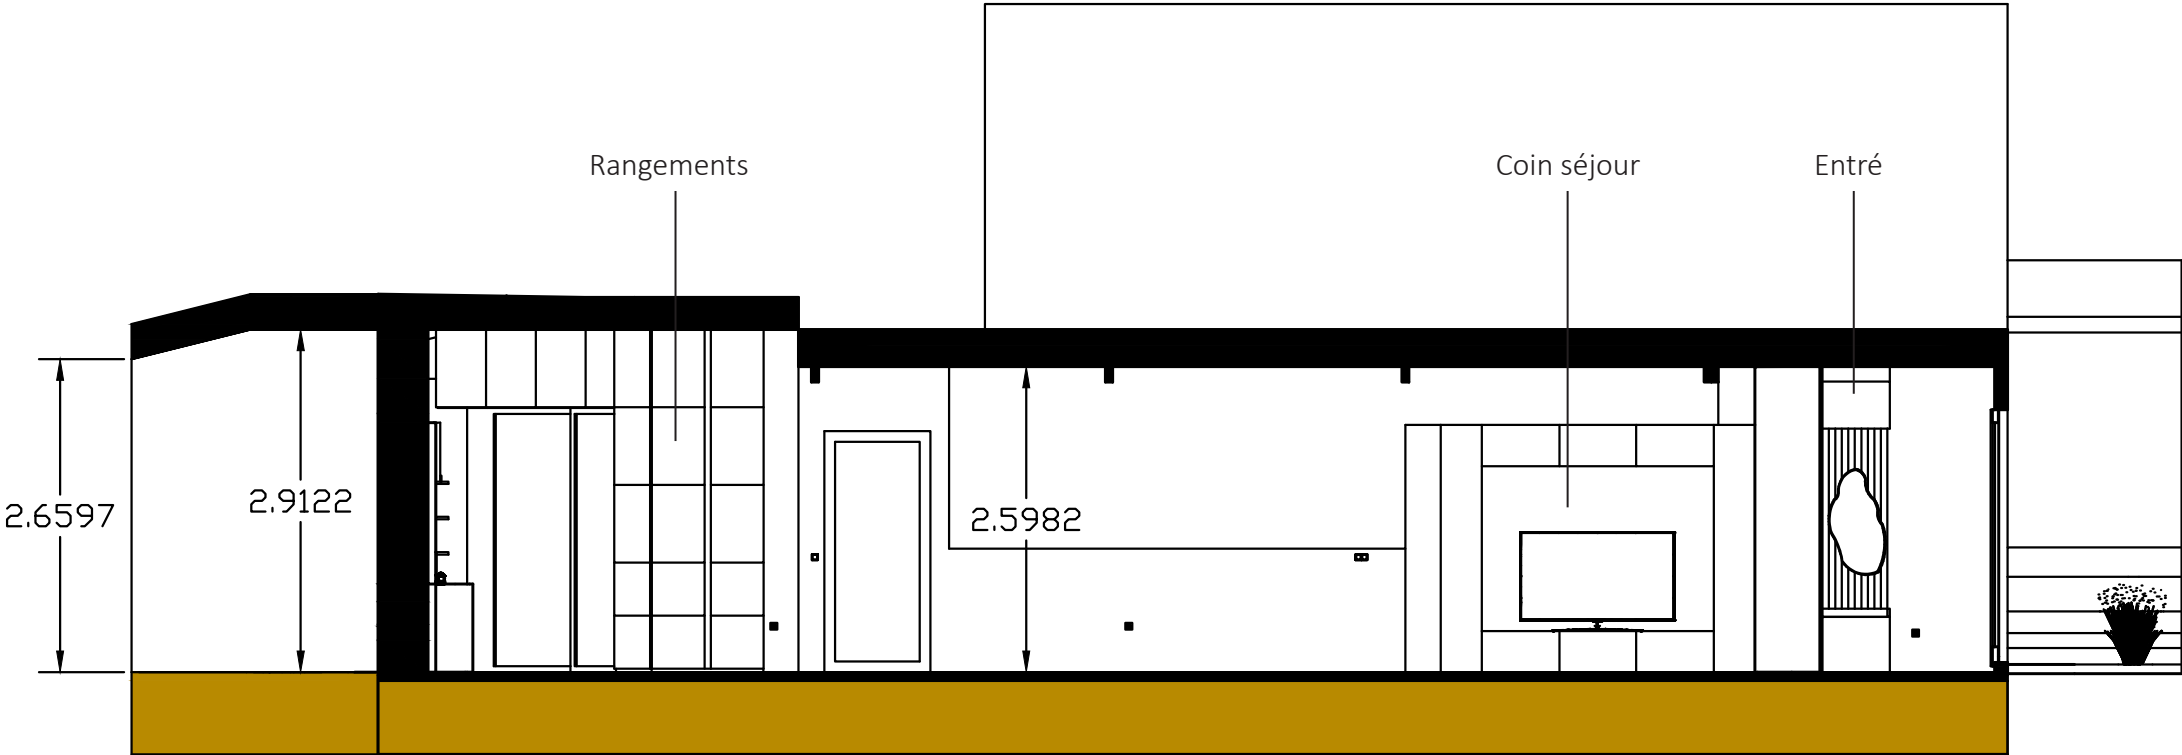

0 1

|                                                                |                                              |                        |                                                                                                |                              |
|----------------------------------------------------------------|----------------------------------------------|------------------------|------------------------------------------------------------------------------------------------|------------------------------|
| <b>Ouvrage</b><br>Tiny House<br>6 av Eugène Godin, 77000 Melun | <b>Maitre d’ouvrage</b><br>Yacine Hadj Hamou |                        | <b>Maitre d’oeuvre</b><br>Marec Alon / Distrophe Alan<br>12 rue Anatole France ,92000 Nanterre |                              |
| <b>Titre</b><br>Coupe AA                                       | <b>Echelle</b><br>A3                         | <b>Format</b><br>1/100 | <b>Date</b><br>15/06/2026                                                                      | <b>Etat du projet</b><br>APD |


Coupe BB

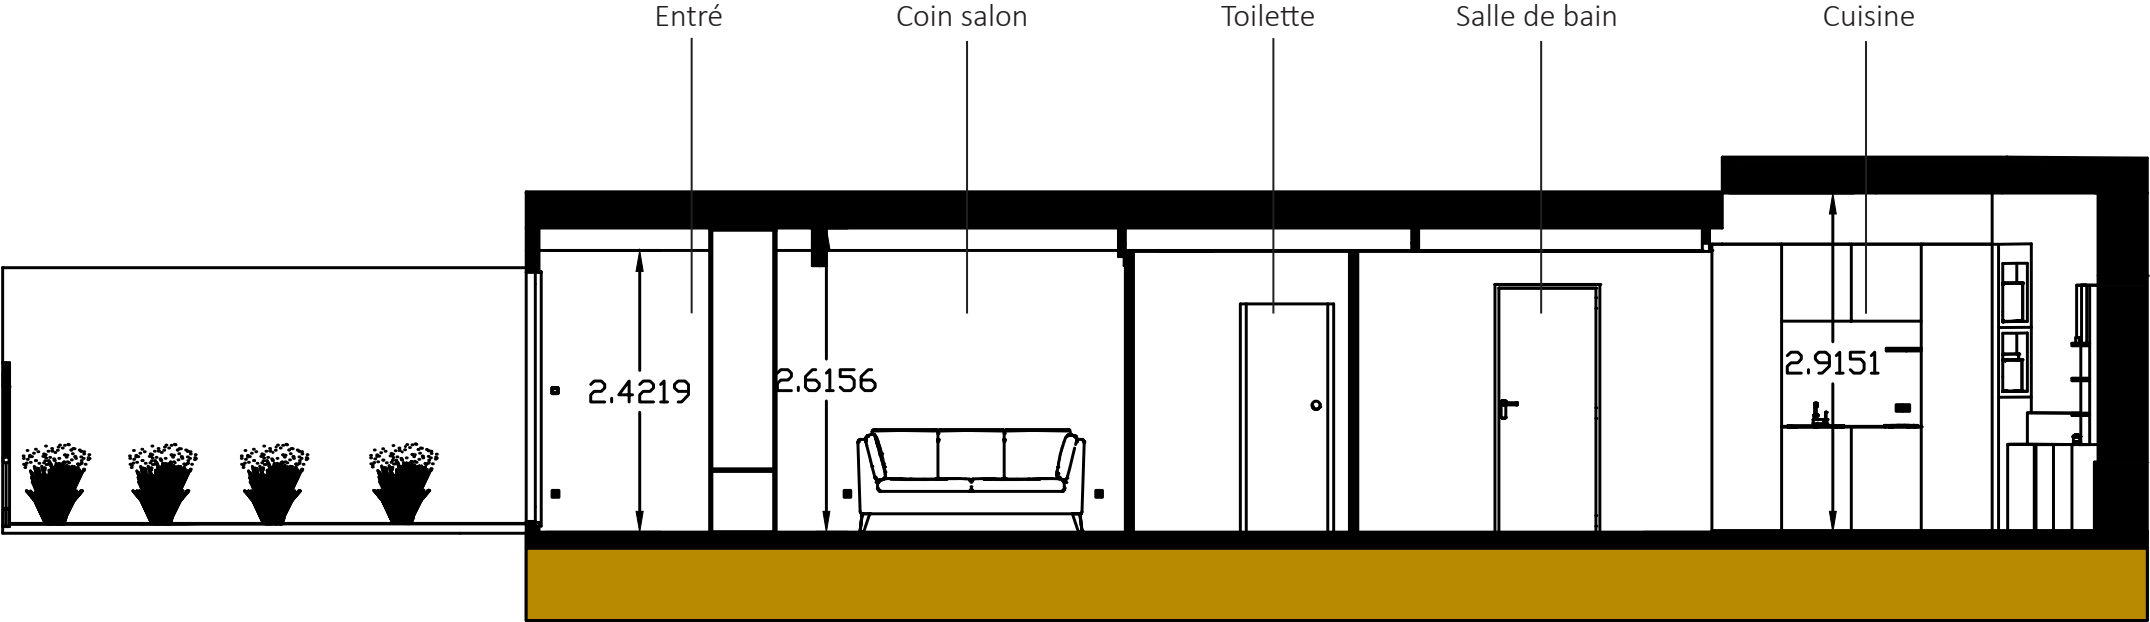

0 1

|                                                                |                                              |                        |                                                                                                |                              |
|----------------------------------------------------------------|----------------------------------------------|------------------------|------------------------------------------------------------------------------------------------|------------------------------|
| <b>Ouvrage</b><br>Tiny House<br>6 av Eugène Godin, 77000 Melun | <b>Maitre d’ouvrage</b><br>Yacine Hadj Hamou |                        | <b>Maitre d’oeuvre</b><br>Marec Alon / Distrophe Alan<br>12 rue Anatole France ,92000 Nanterre |                              |
| <b>Titre</b><br>Coupe BB                                       | <b>Echelle</b><br>A3                         | <b>Format</b><br>1/100 | <b>Date</b><br>15/06/2026                                                                      | <b>Etat du projet</b><br>APD |


Coupe CC

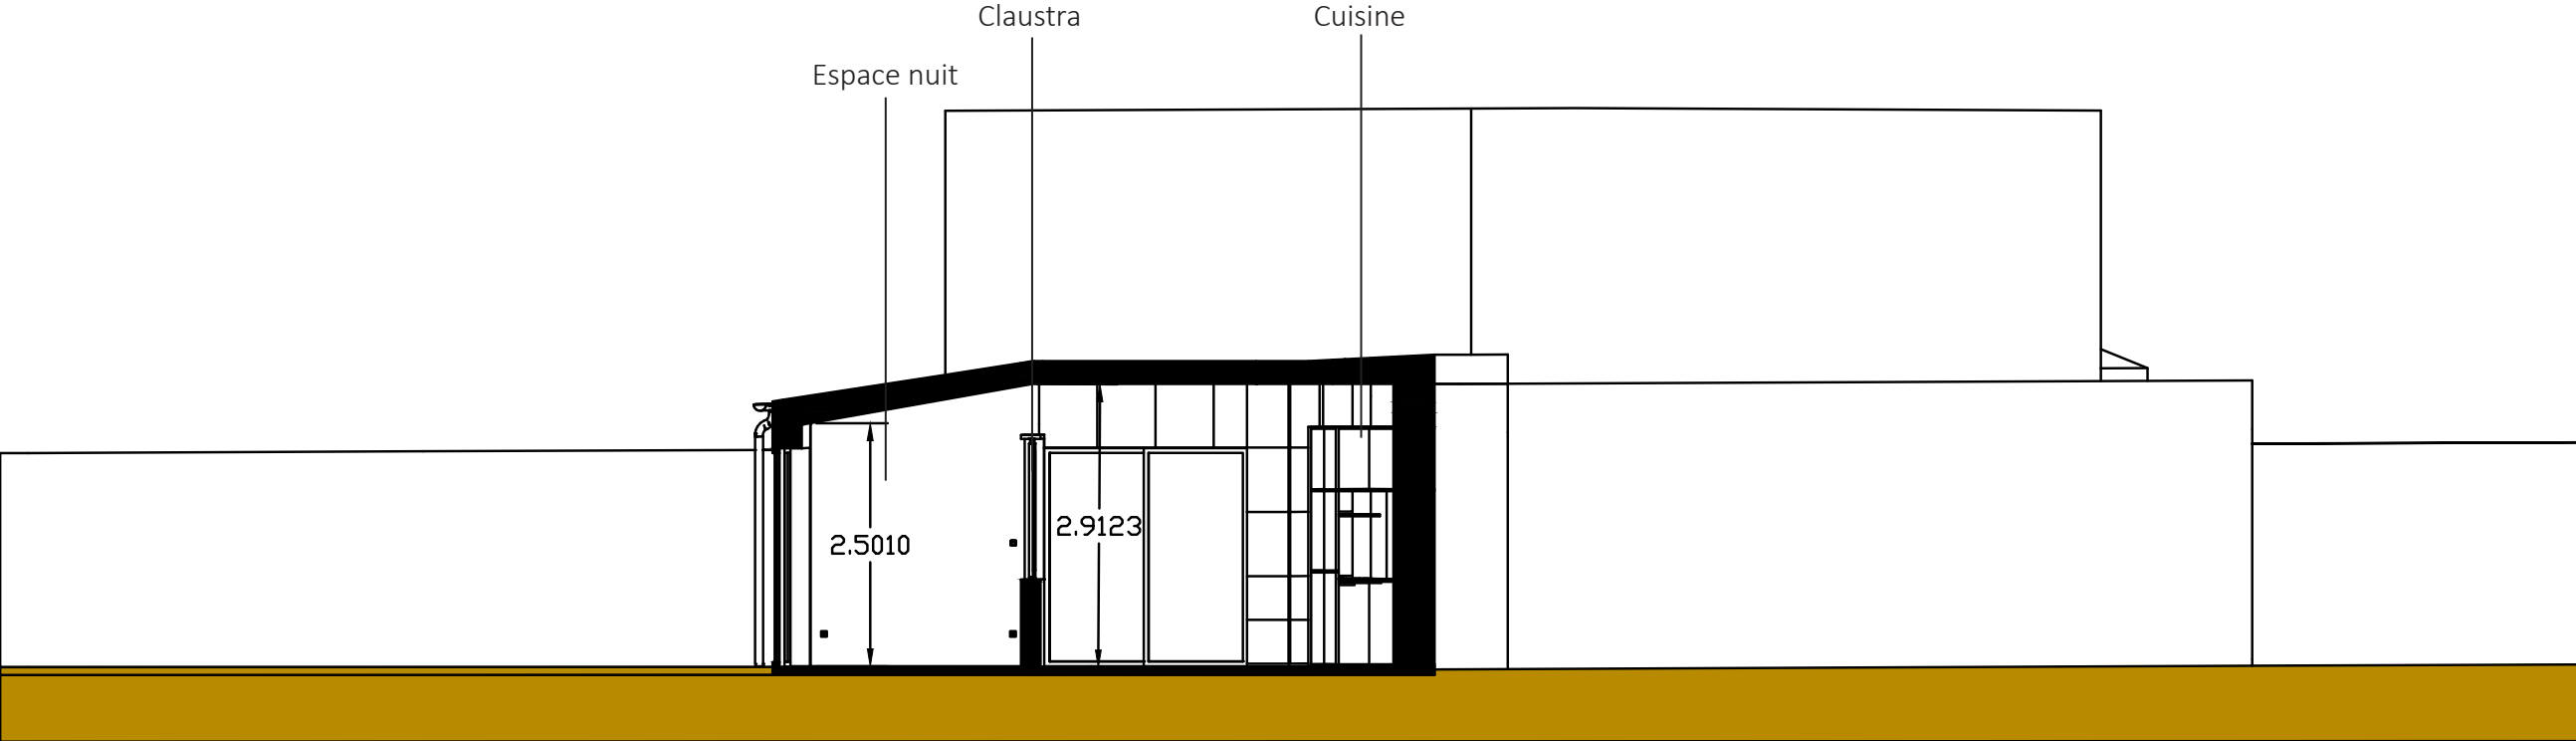

0 1

|                                                                |                                              |                        |                                                                                                |                              |
|----------------------------------------------------------------|----------------------------------------------|------------------------|------------------------------------------------------------------------------------------------|------------------------------|
| <b>Ouvrage</b><br>Tiny House<br>6 av Eugène Godin, 77000 Melun | <b>Maitre d’ouvrage</b><br>Yacine Hadj Hamou |                        | <b>Maitre d’oeuvre</b><br>Marec Alon / Distrophe Alan<br>12 rue Anatole France ,92000 Nanterre |                              |
| <b>Titre</b><br>Coupe CC                                       | <b>Echelle</b><br>A3                         | <b>Format</b><br>1/100 | <b>Date</b><br>15/06/2026                                                                      | <b>Etat du projet</b><br>APD |


Coupe DD

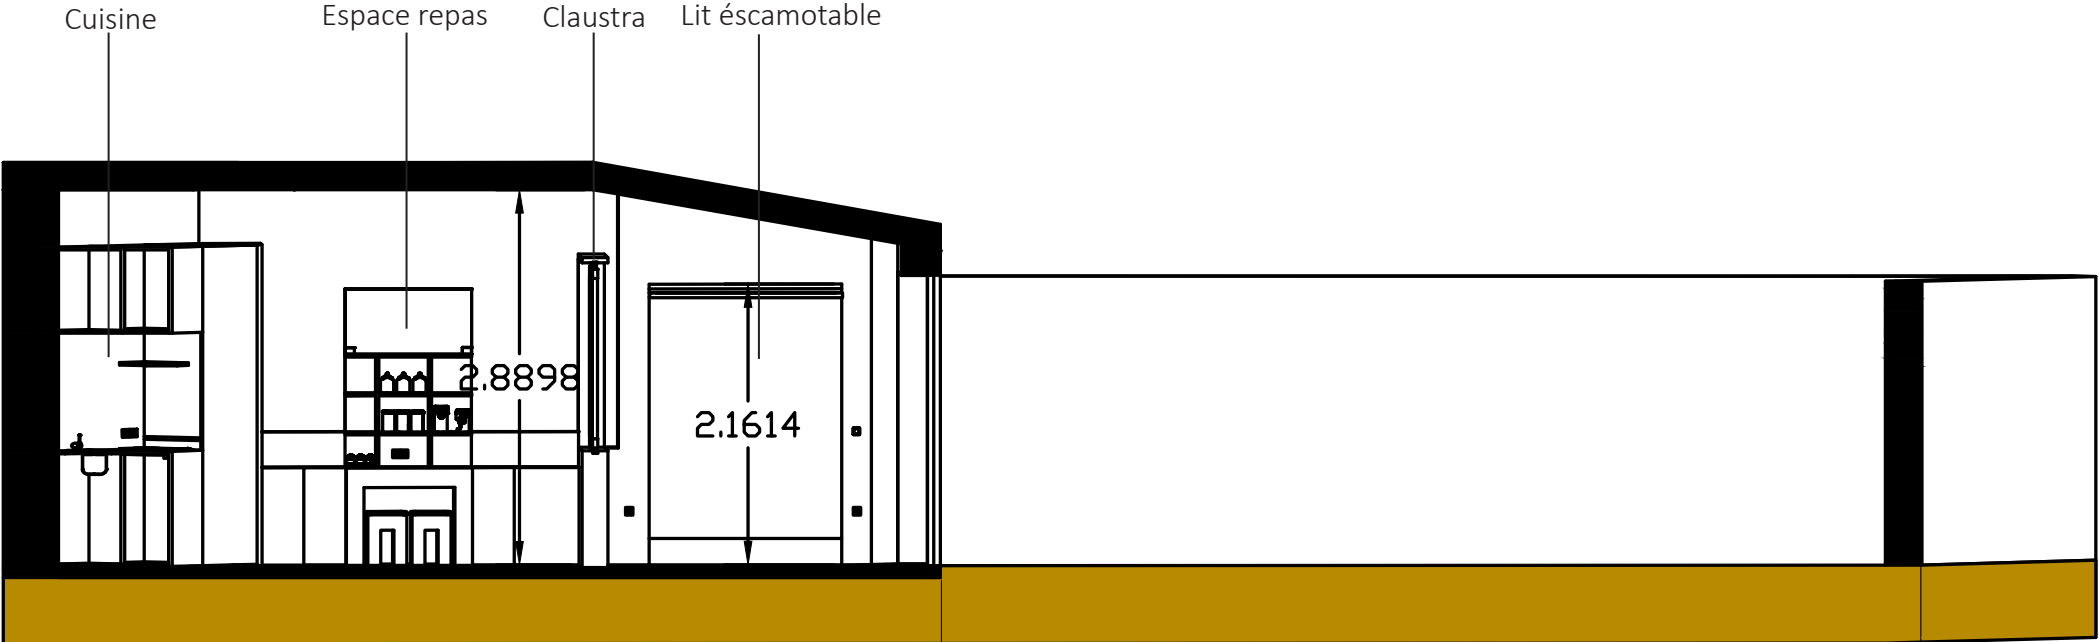

0 1

|                                                                |                                              |                        |                                                                                                |                              |
|----------------------------------------------------------------|----------------------------------------------|------------------------|------------------------------------------------------------------------------------------------|------------------------------|
| <b>Ouvrage</b><br>Tiny House<br>6 av Eugène Godin, 77000 Melun | <b>Maitre d’ouvrage</b><br>Yacine Hadj Hamou |                        | <b>Maitre d’oeuvre</b><br>Marec Alon / Distrophe Alan<br>12 rue Anatole France ,92000 Nanterre |                              |
| <b>Titre</b><br>Coupe DD                                       | <b>Echelle</b><br>A3                         | <b>Format</b><br>1/100 | <b>Date</b><br>15/06/2026                                                                      | <b>Etat du projet</b><br>APS |

Détail mobilier

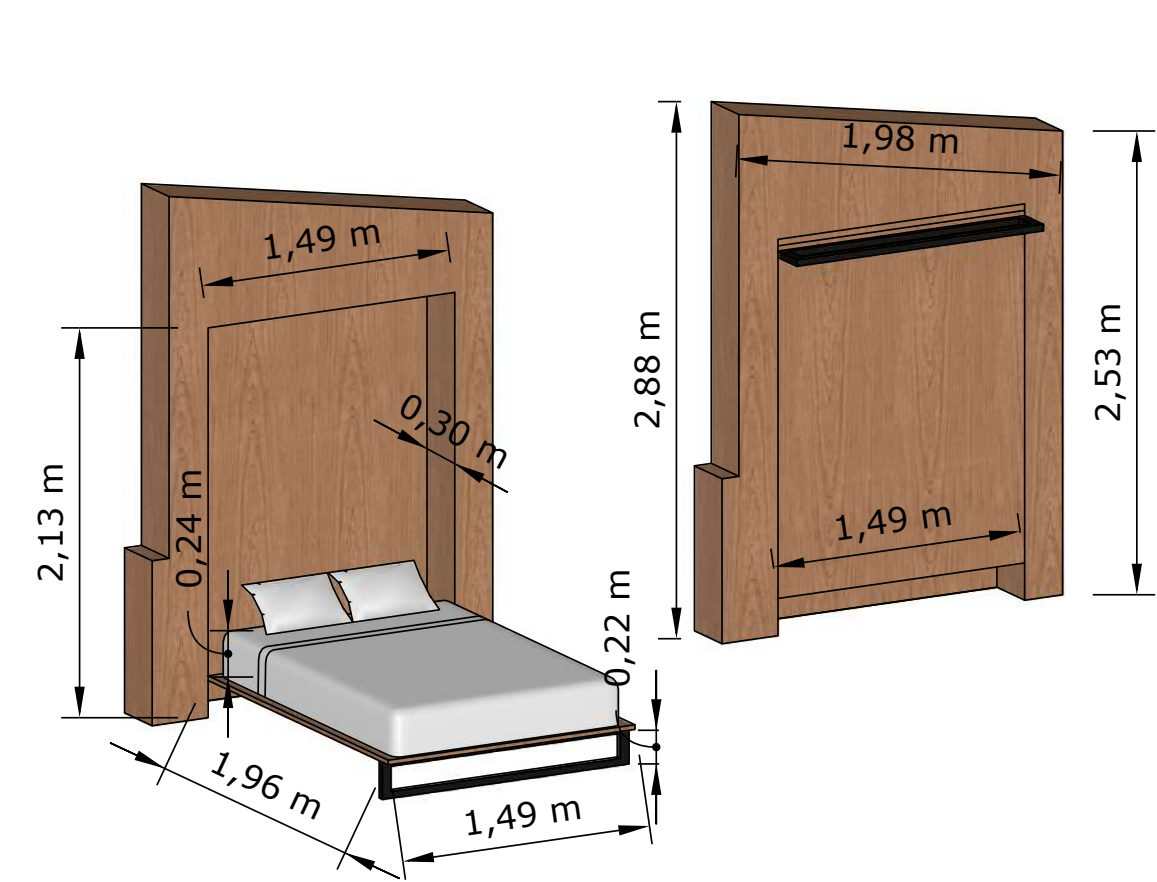

Lit escamotable


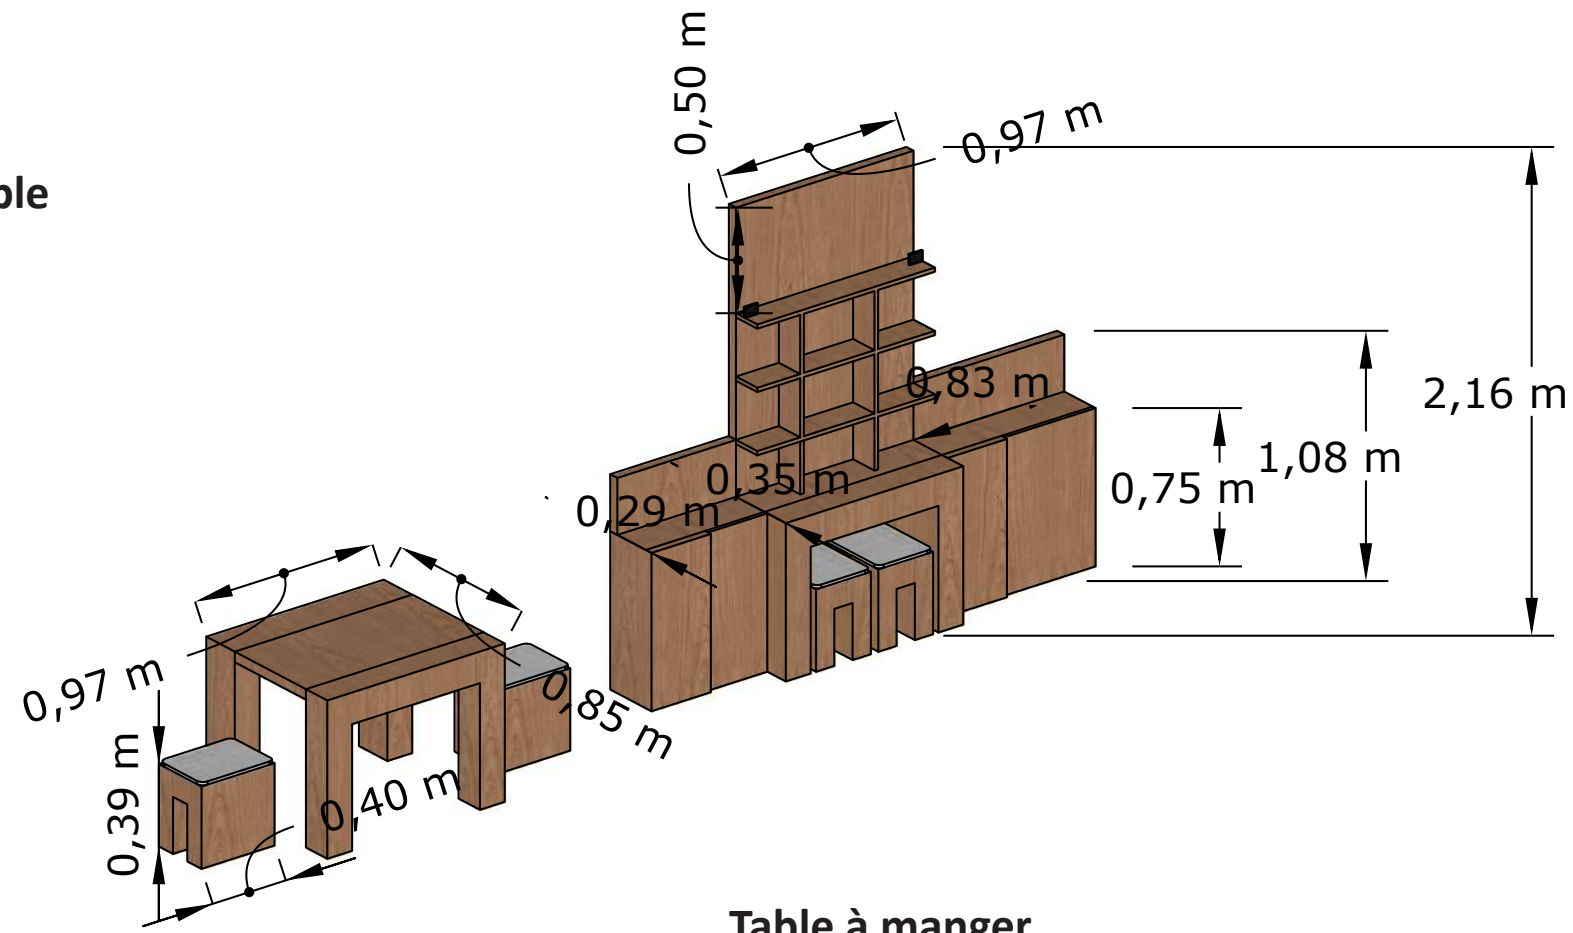


Table à manger

Clastra



# Planche matériaux intérieurs et extérieurs

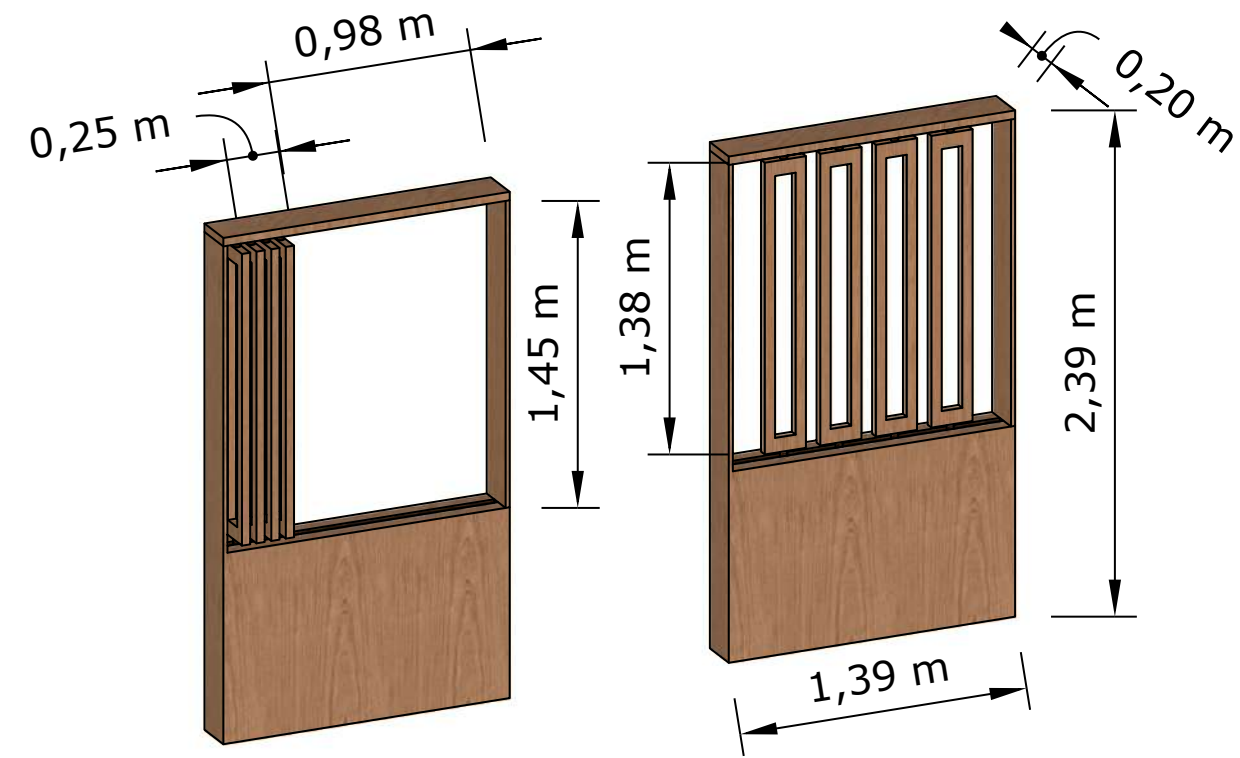

Parquet contrecollé Chêne Ivoire

Utilisé partout sauf  
pour les toilettes et la  
salle de bain

Placage Chêne

Utilisé pour tous les  
meubles présents dans  
le garage et la Tiny  
House

Zinc à joint debout

Utilisé sur toute la  
surface de la toiture



Bardage western red cedar

Utilisé pour la facade  
extérieure



# INCTRUSTATION A L'EXISTANT

poteaux sur disque + pieux acier galv + ossature bois + toiture

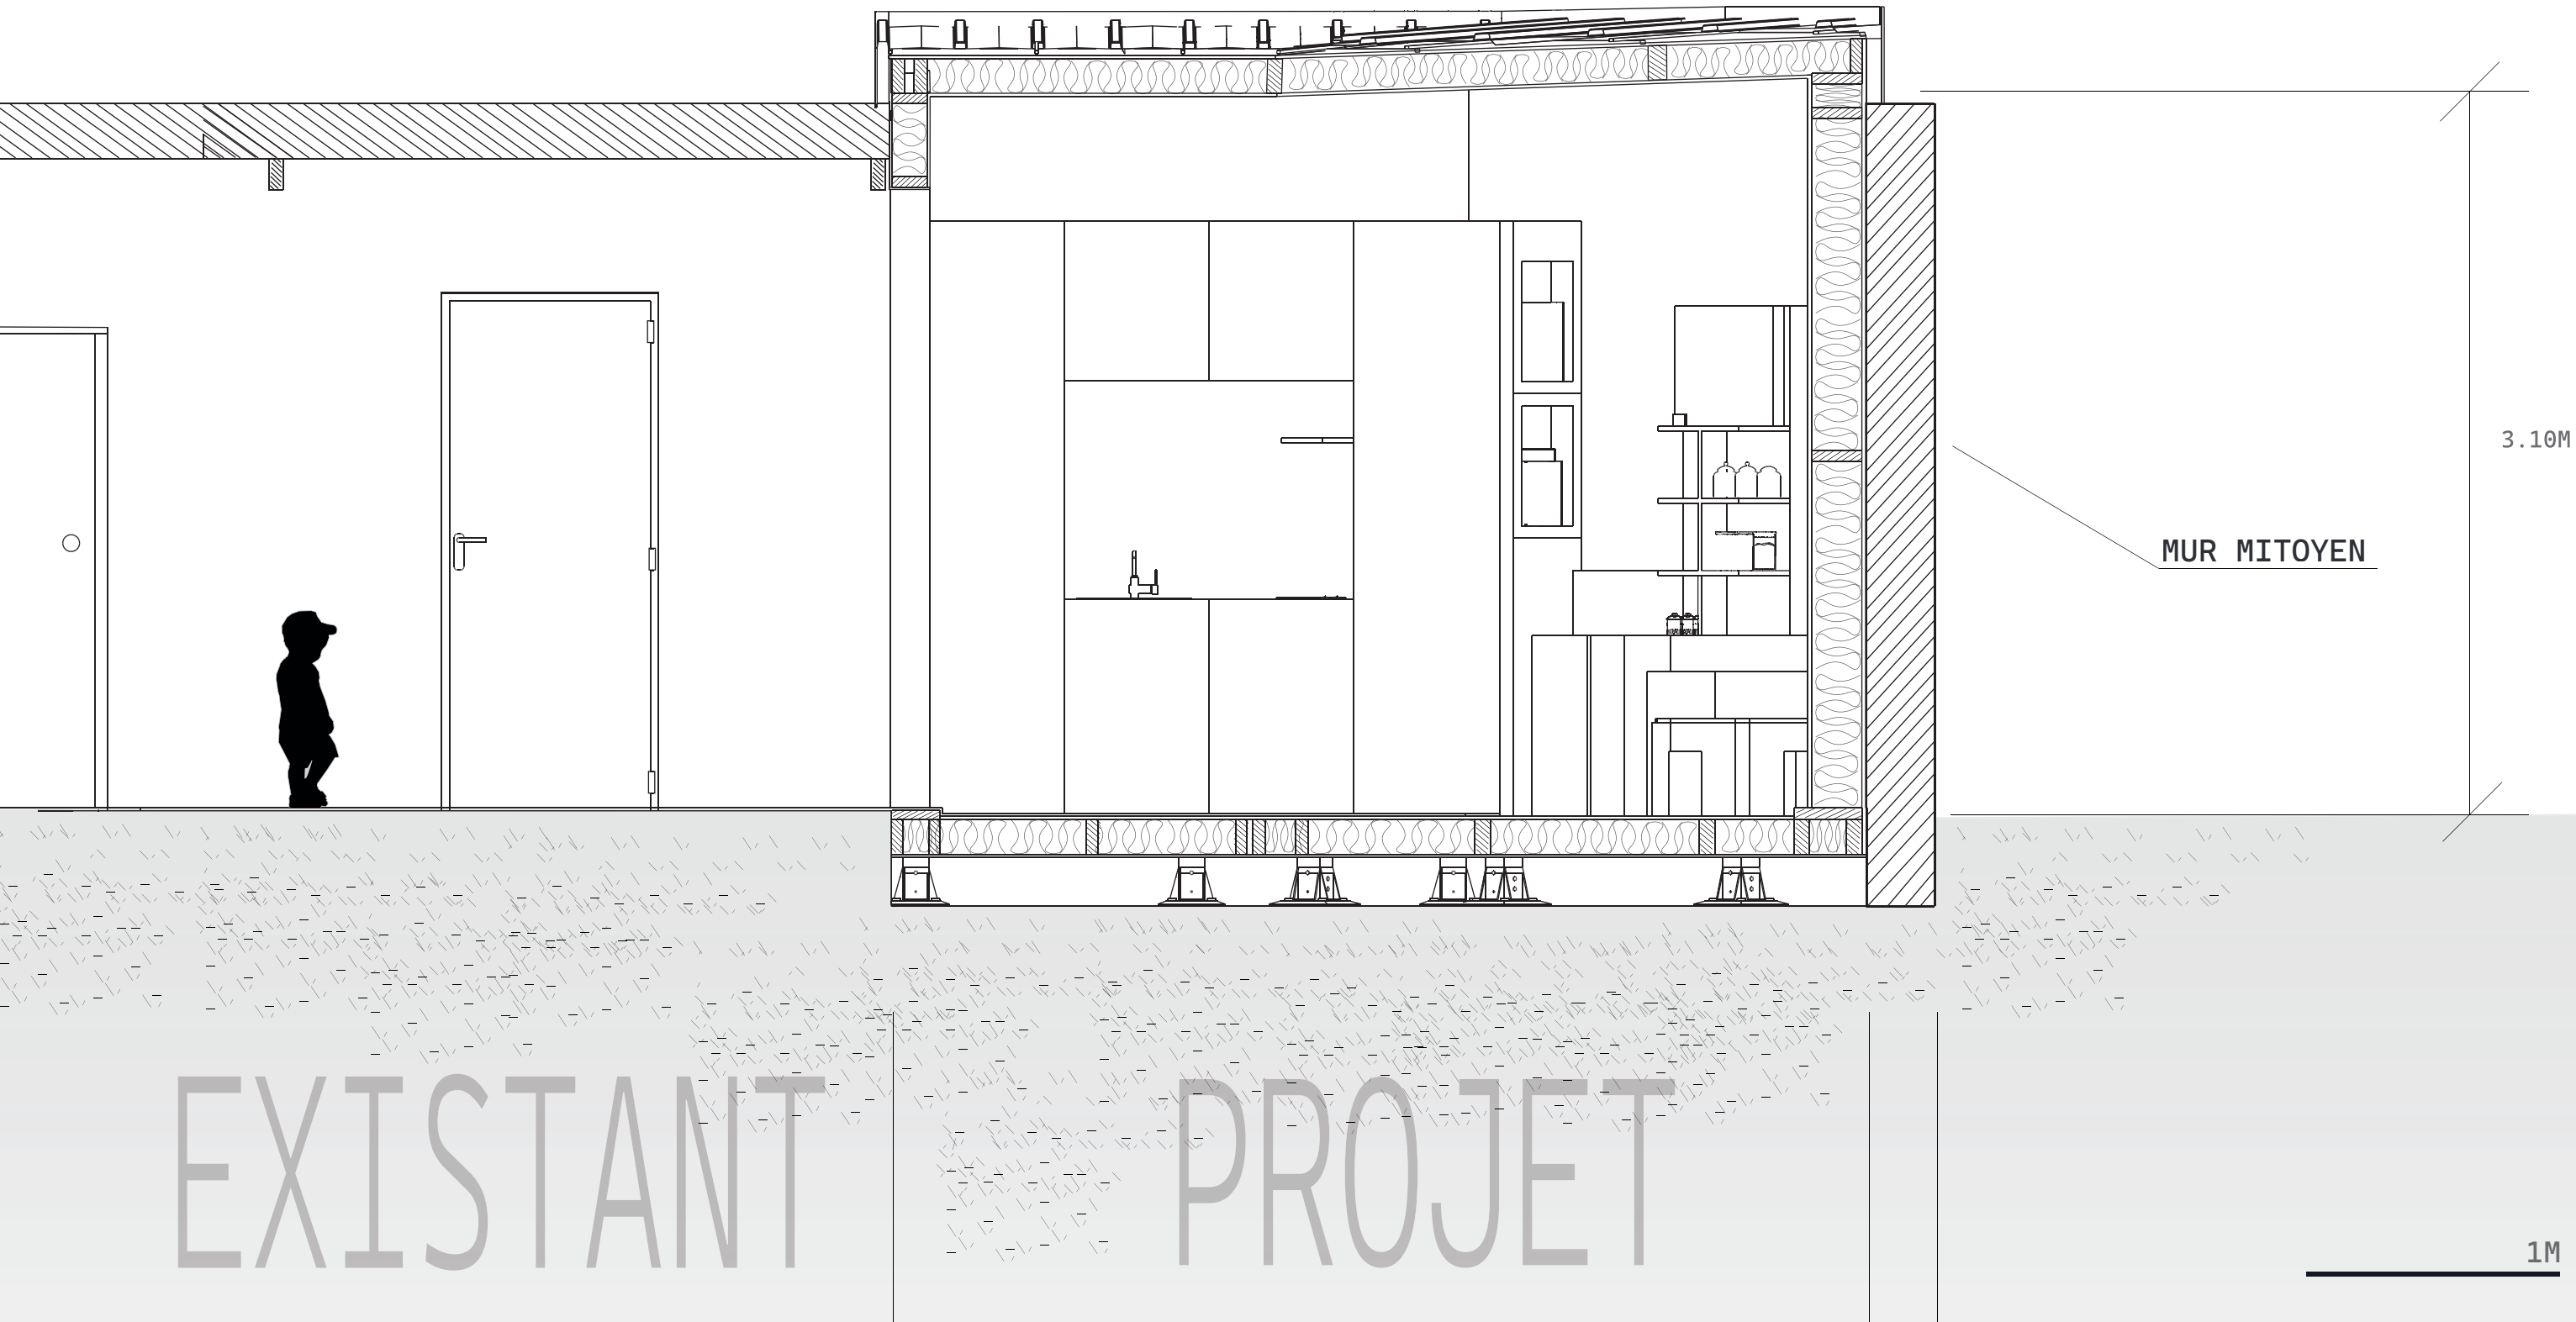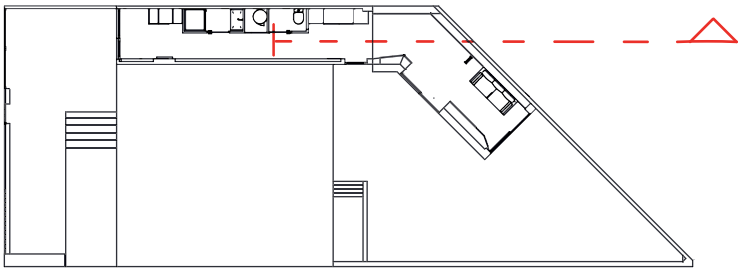



DETAIL STRUCTUREL ( Schéma )

pieux acier galv + ossature bois + toiture bac acier

Type de sol dominant Melun : LUVISOL(87%)

ZONING FONDATION

ZONE DE FONDATION

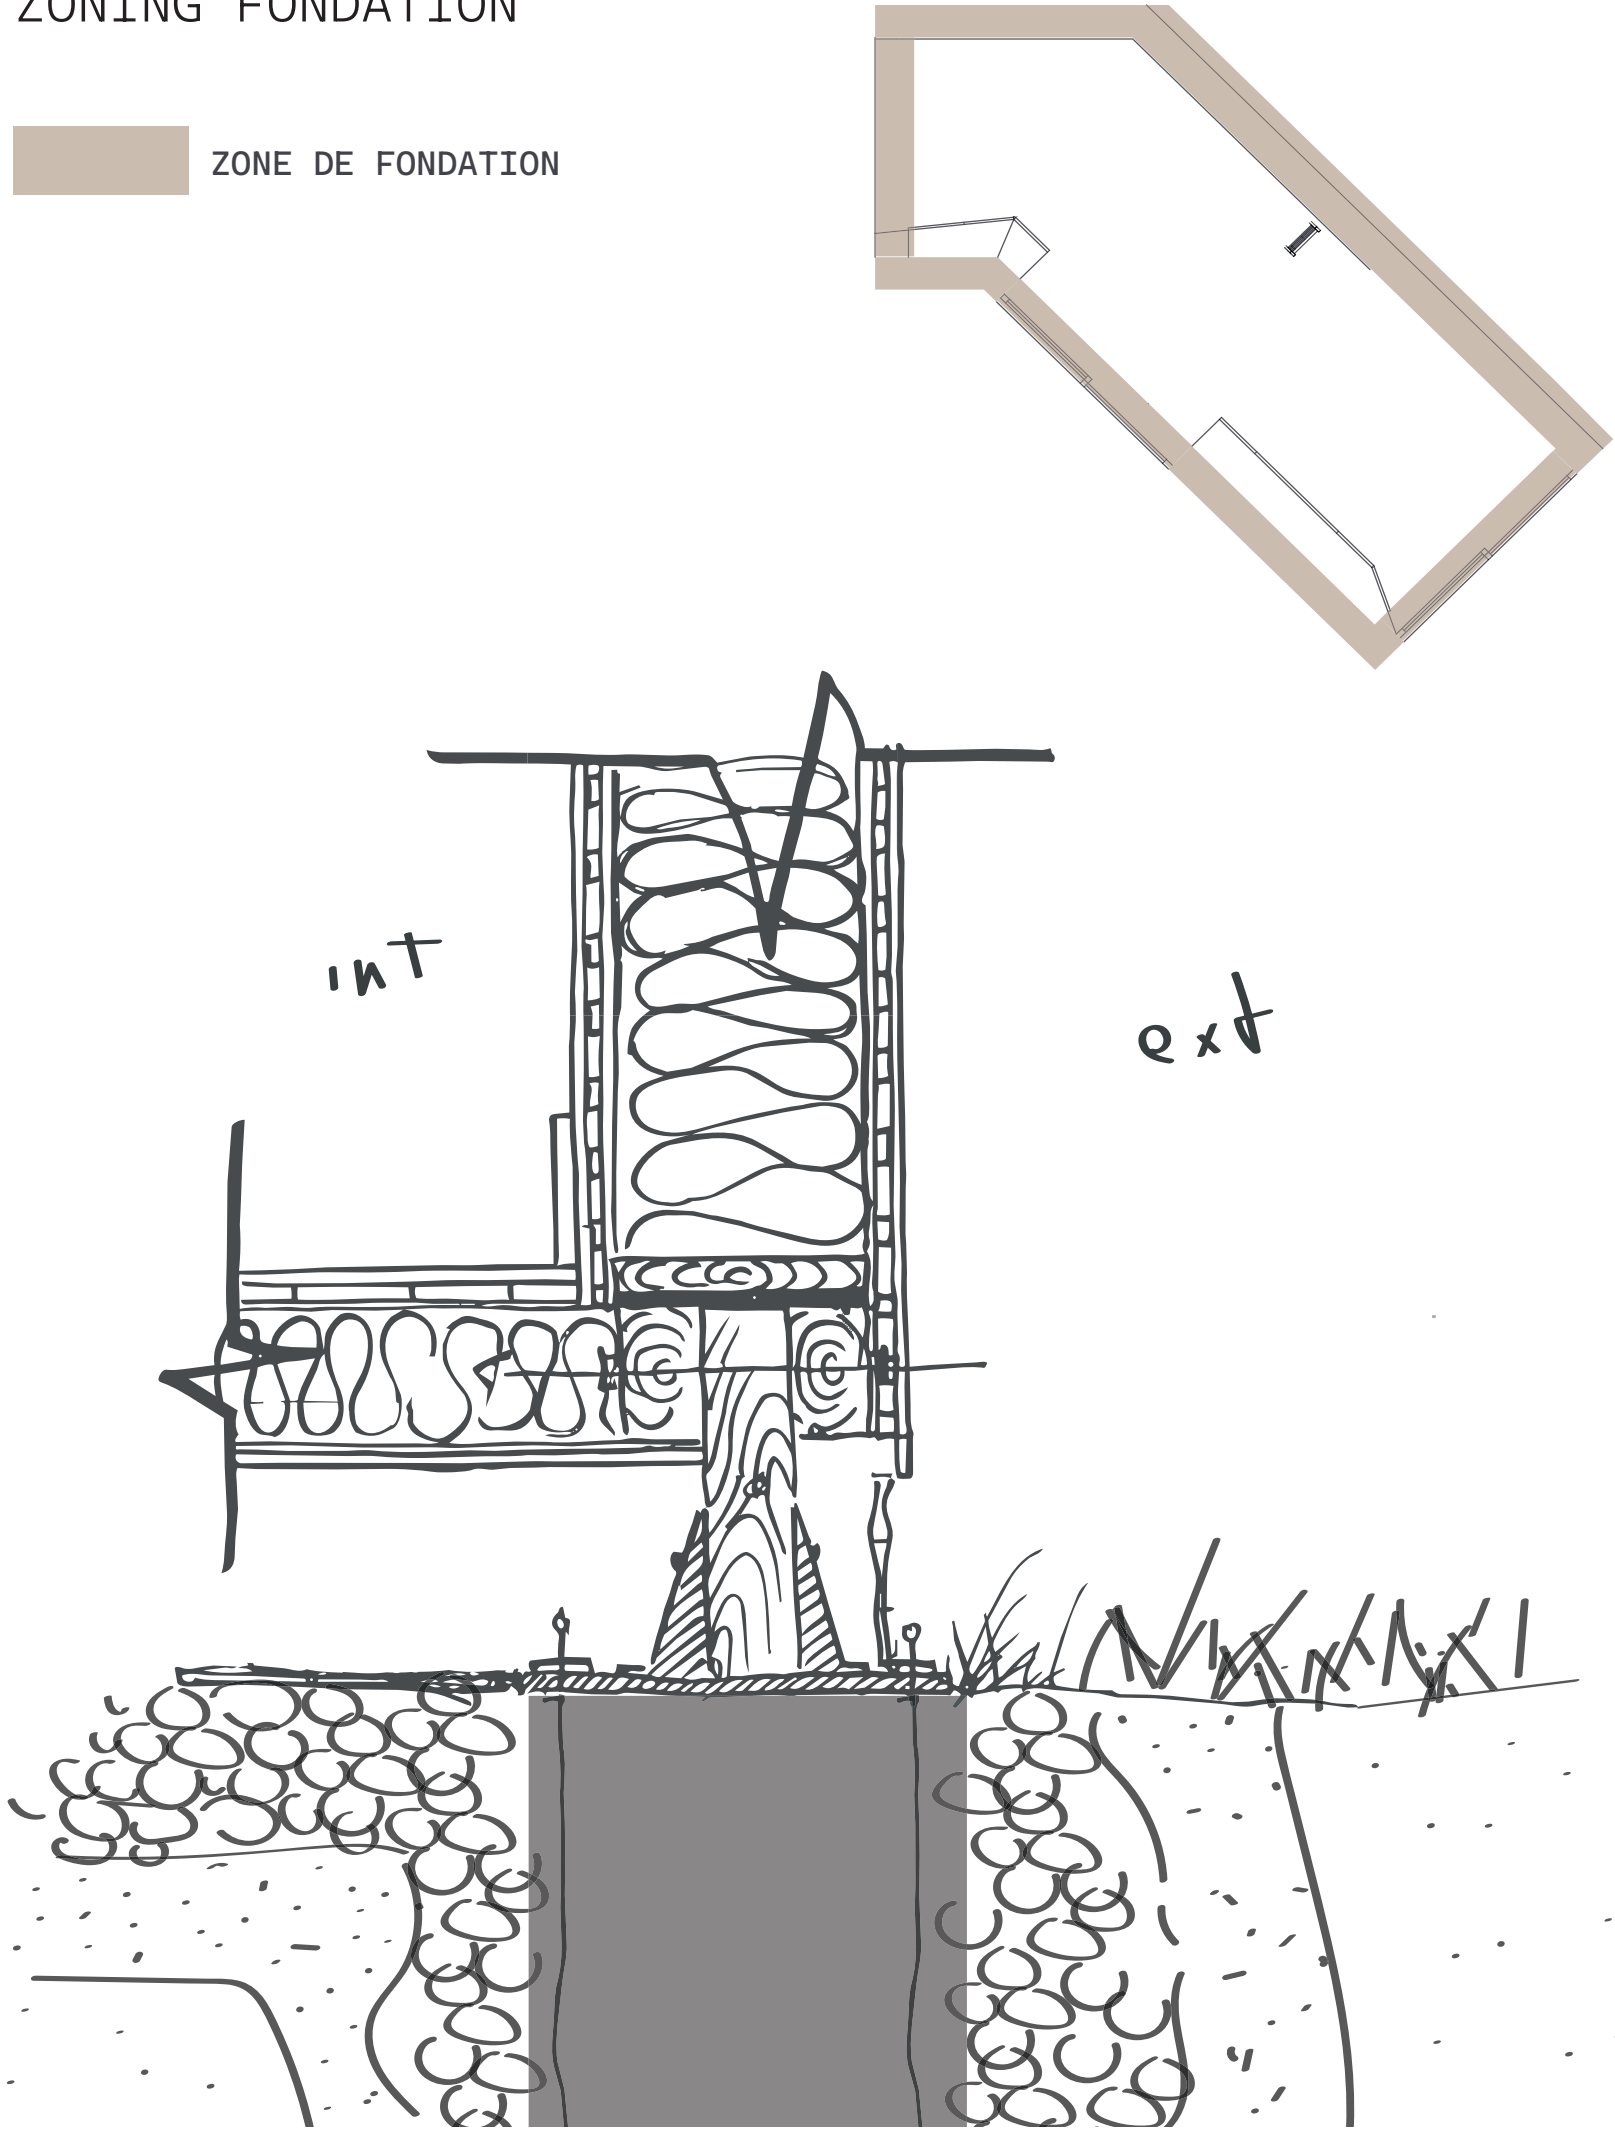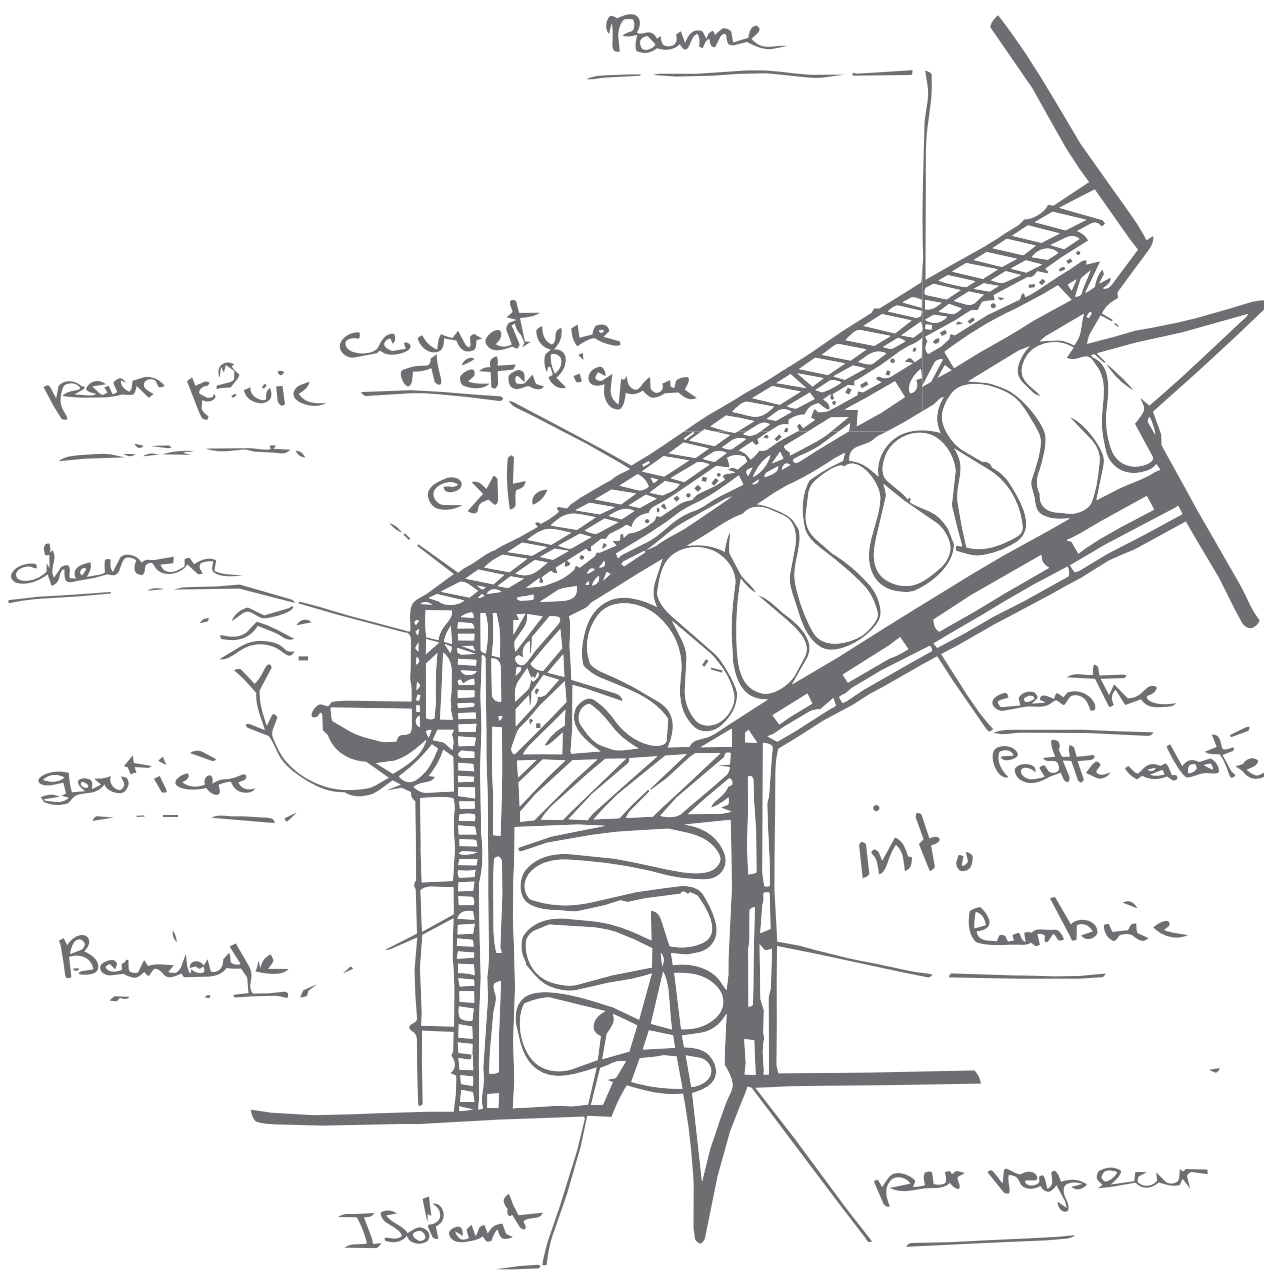



# DETAIL STRUCTUREL FACADE

poteaux sur disque + pieux acier galv + ossature bois + toiture

+ 2.50 ● — — — — —

0 ● — — — — —



− 1.10 ● — — — — —

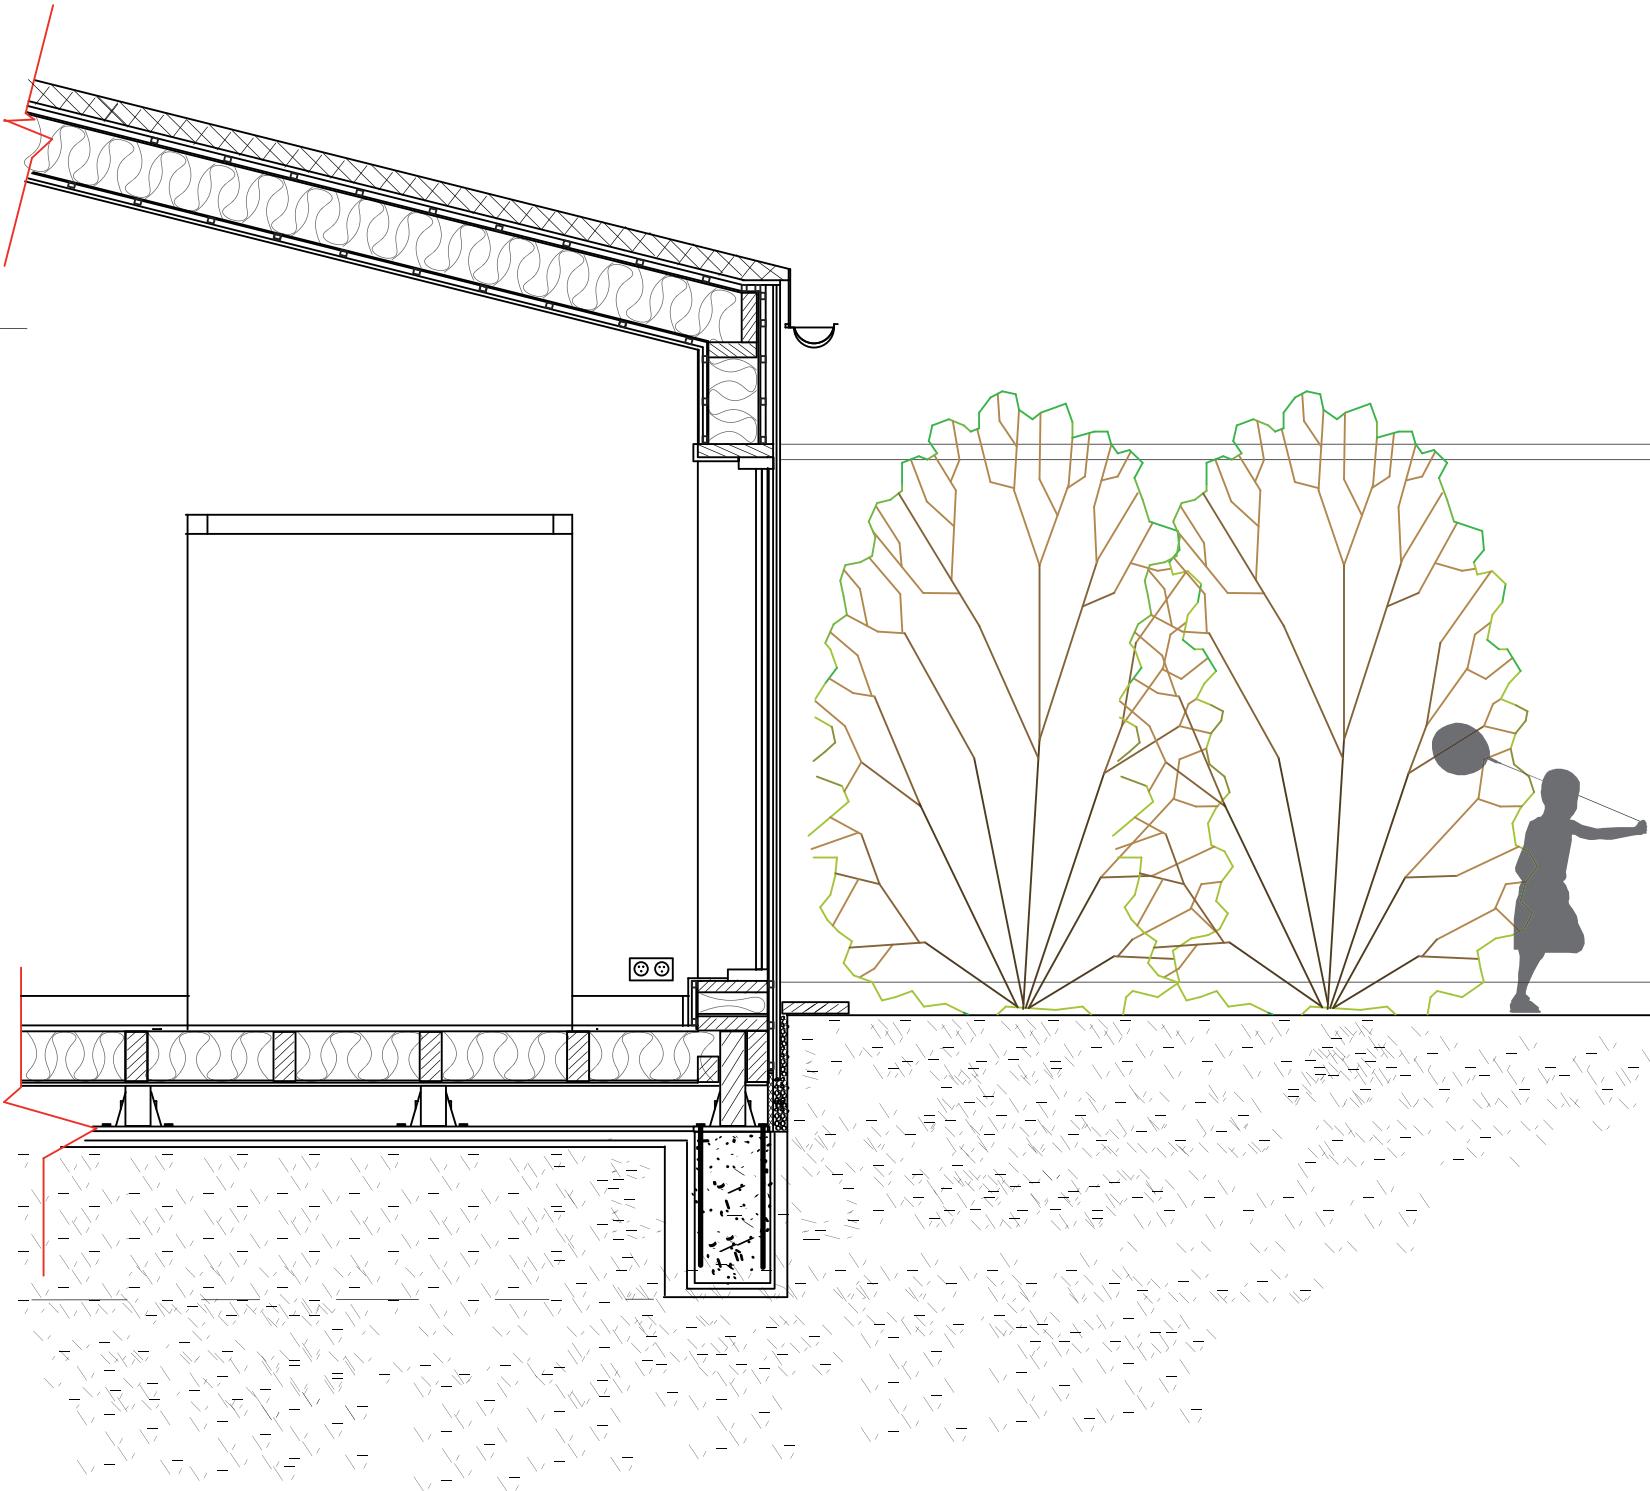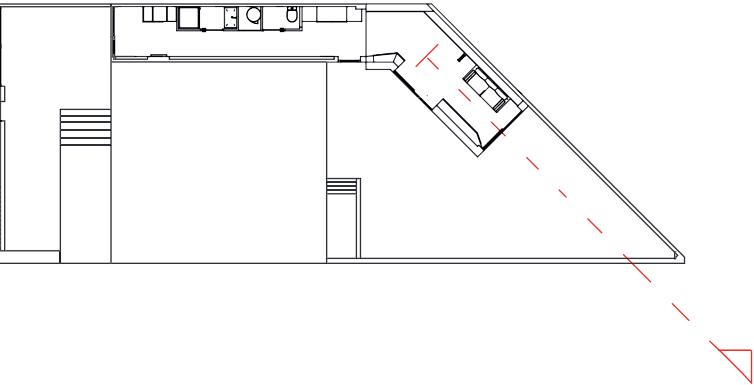

PROFONDEUR PIEUX ACIER 60CM + 25 CM VIDE SANITAIRE + 20 CM PLANCHER

# DETAIL TOITURE + MUR


ossature bois + charpante + toiture bac acier

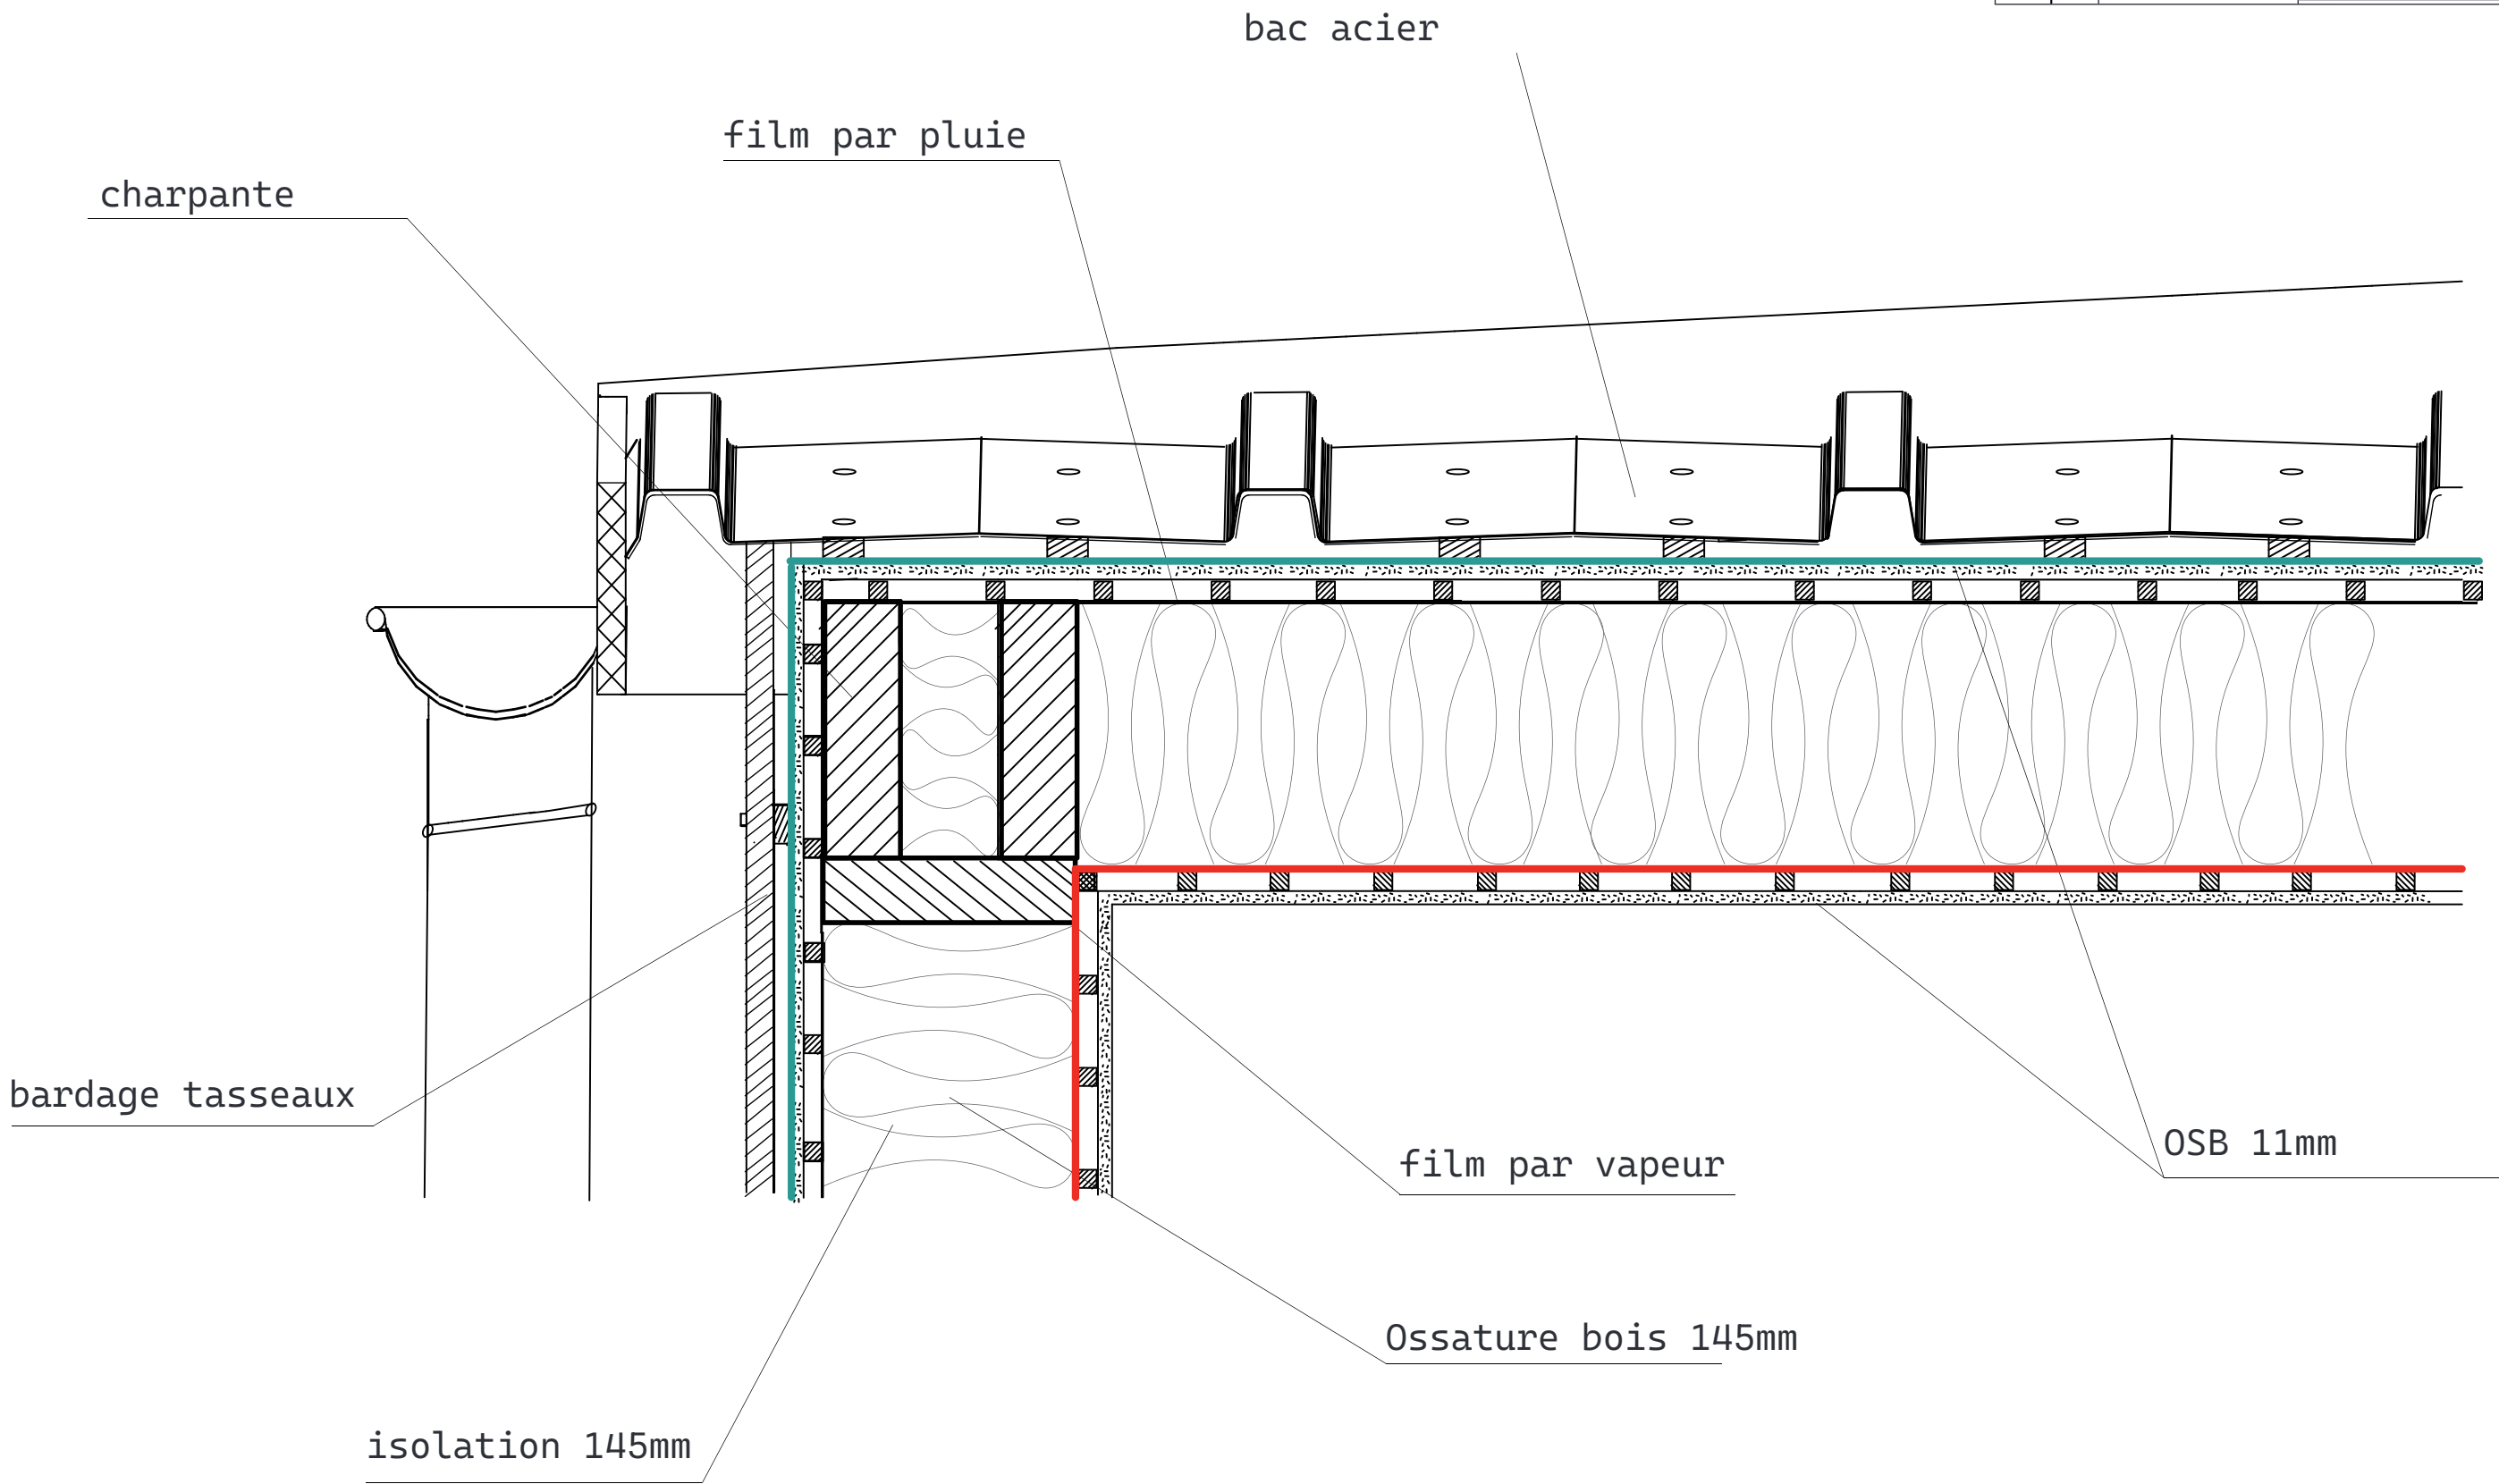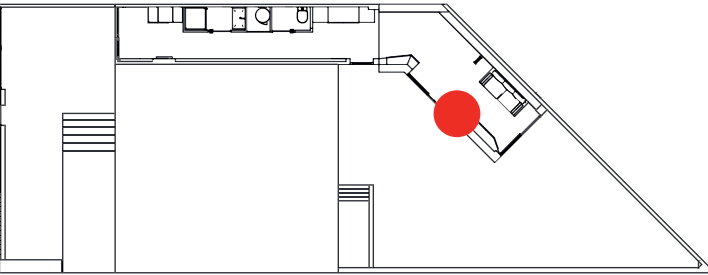

# DETAIL ISOLATION DANS OSSATURE

Ouate de cellulose -  $\lambda$  de 0,039 à 0,042 W/m·K

- Isolation entre montant 45x145

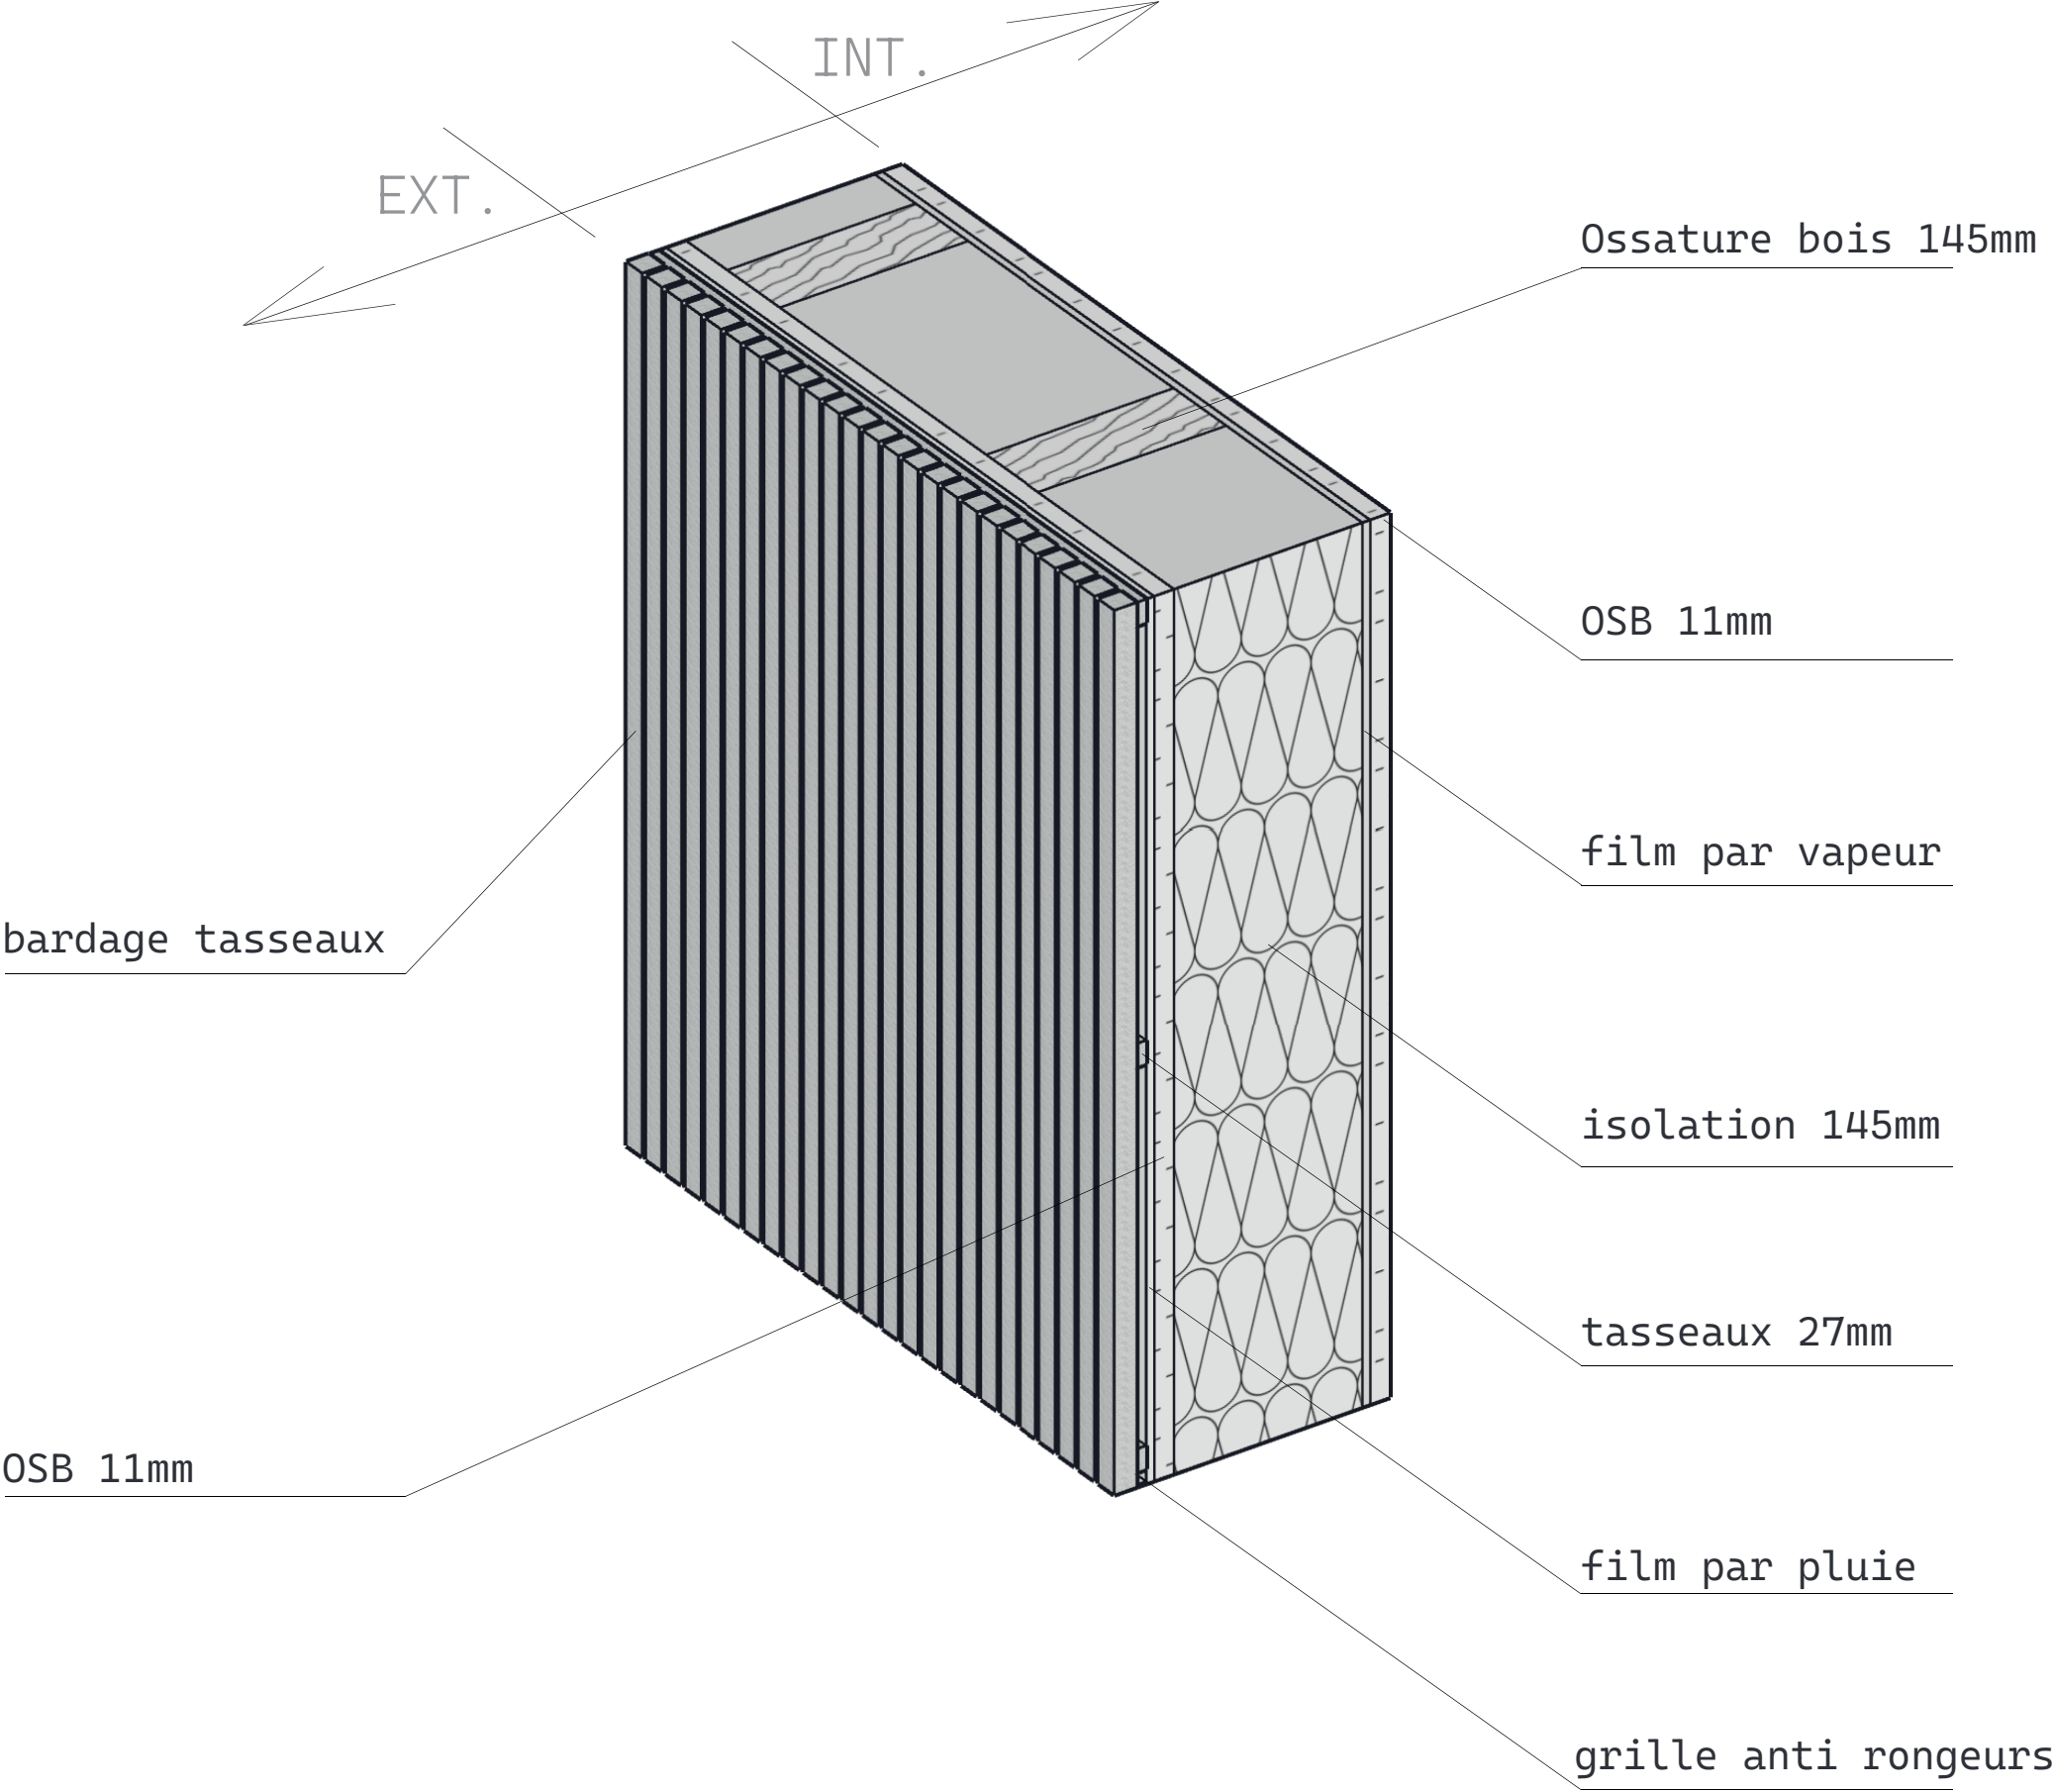

epaisseur finale 22cm





# ISOLATION ZONING

Ouate de cellulose - lambda de 0,039 à 0,042 W/m·K

- Isolation plancher
- Isolation mural
- Isolation toiture



ISOLANT THERMIQUE

PLAN PARCELLE

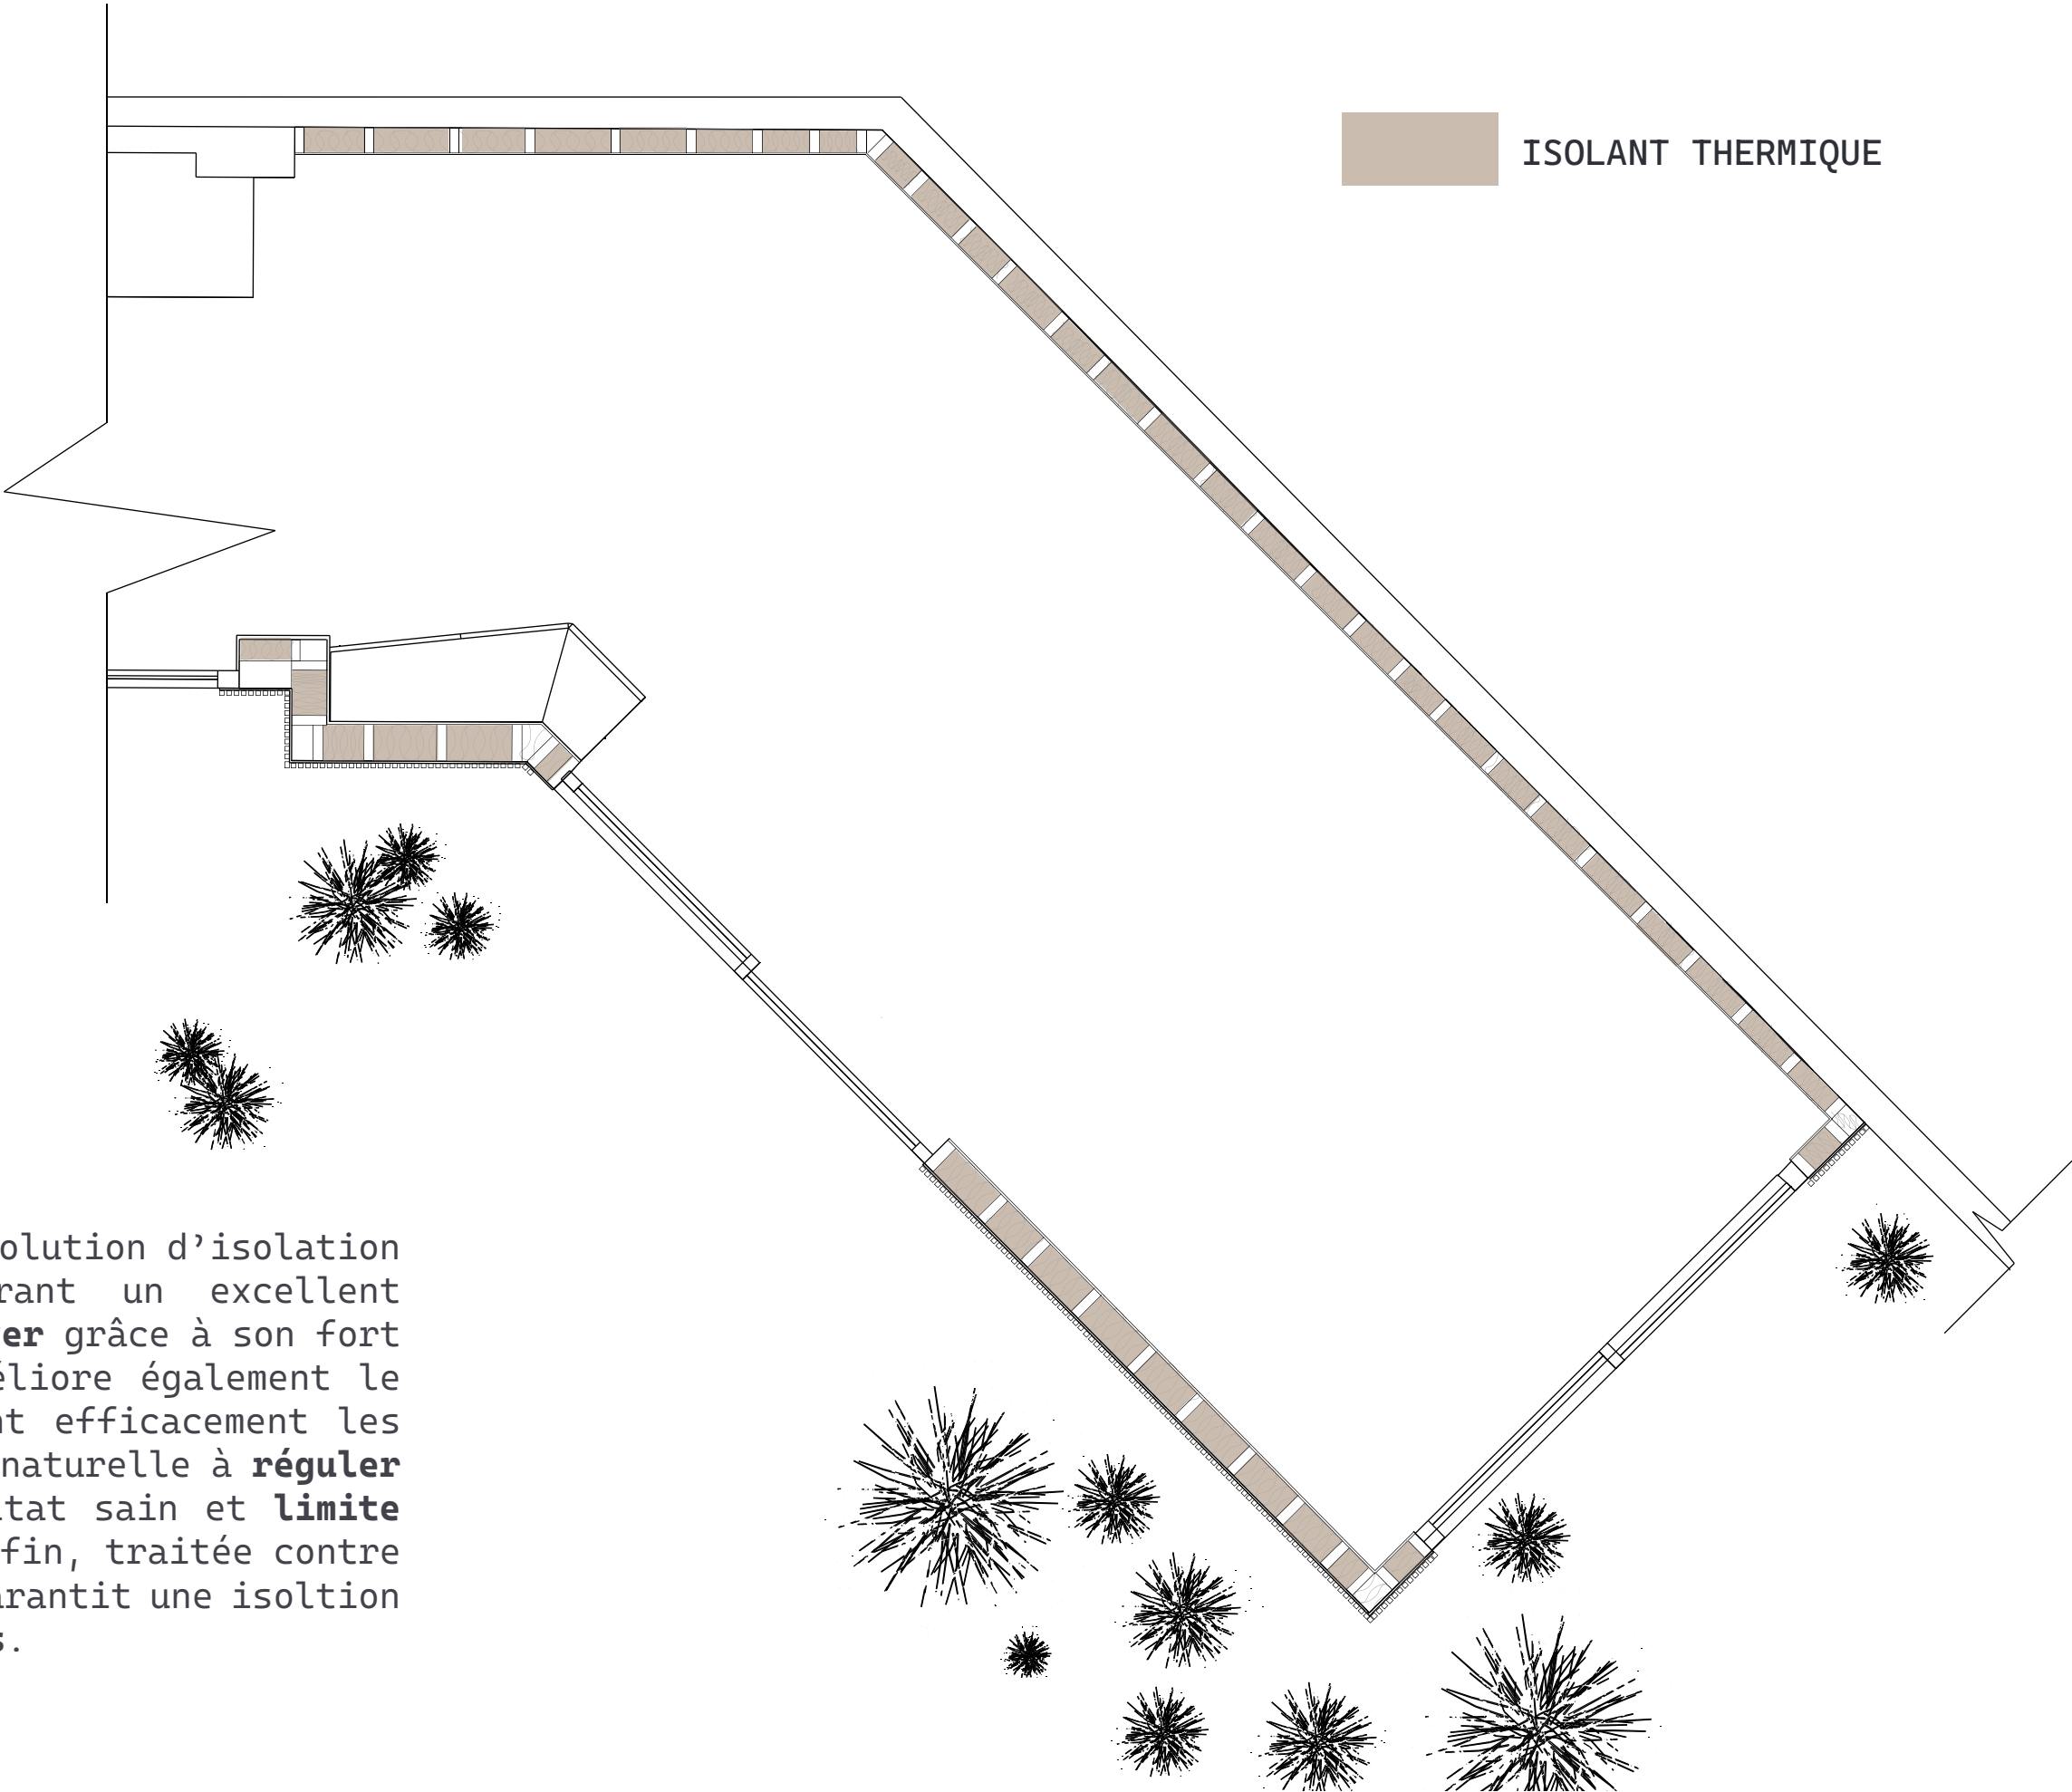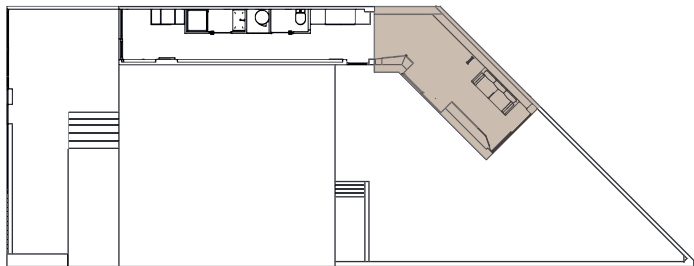

La **ouate de cellulose** est une solution d'isolation performante et durable, offrant un excellent confort **thermique été** comme **hiver** grâce à son fort pouvoir de **déphasage**. Elle améliore également le **confort acoustique** en réduisant efficacement les **nuisances sonores**. Sa capacité naturelle à **réguler l'humidité** contribue à un habitat sain et **limite les risques de condensation**. Enfin, traitée contre le feu et les nuisibles, elle garantit une isolation fiable et durable dans le **temps**.

Plan Électrique

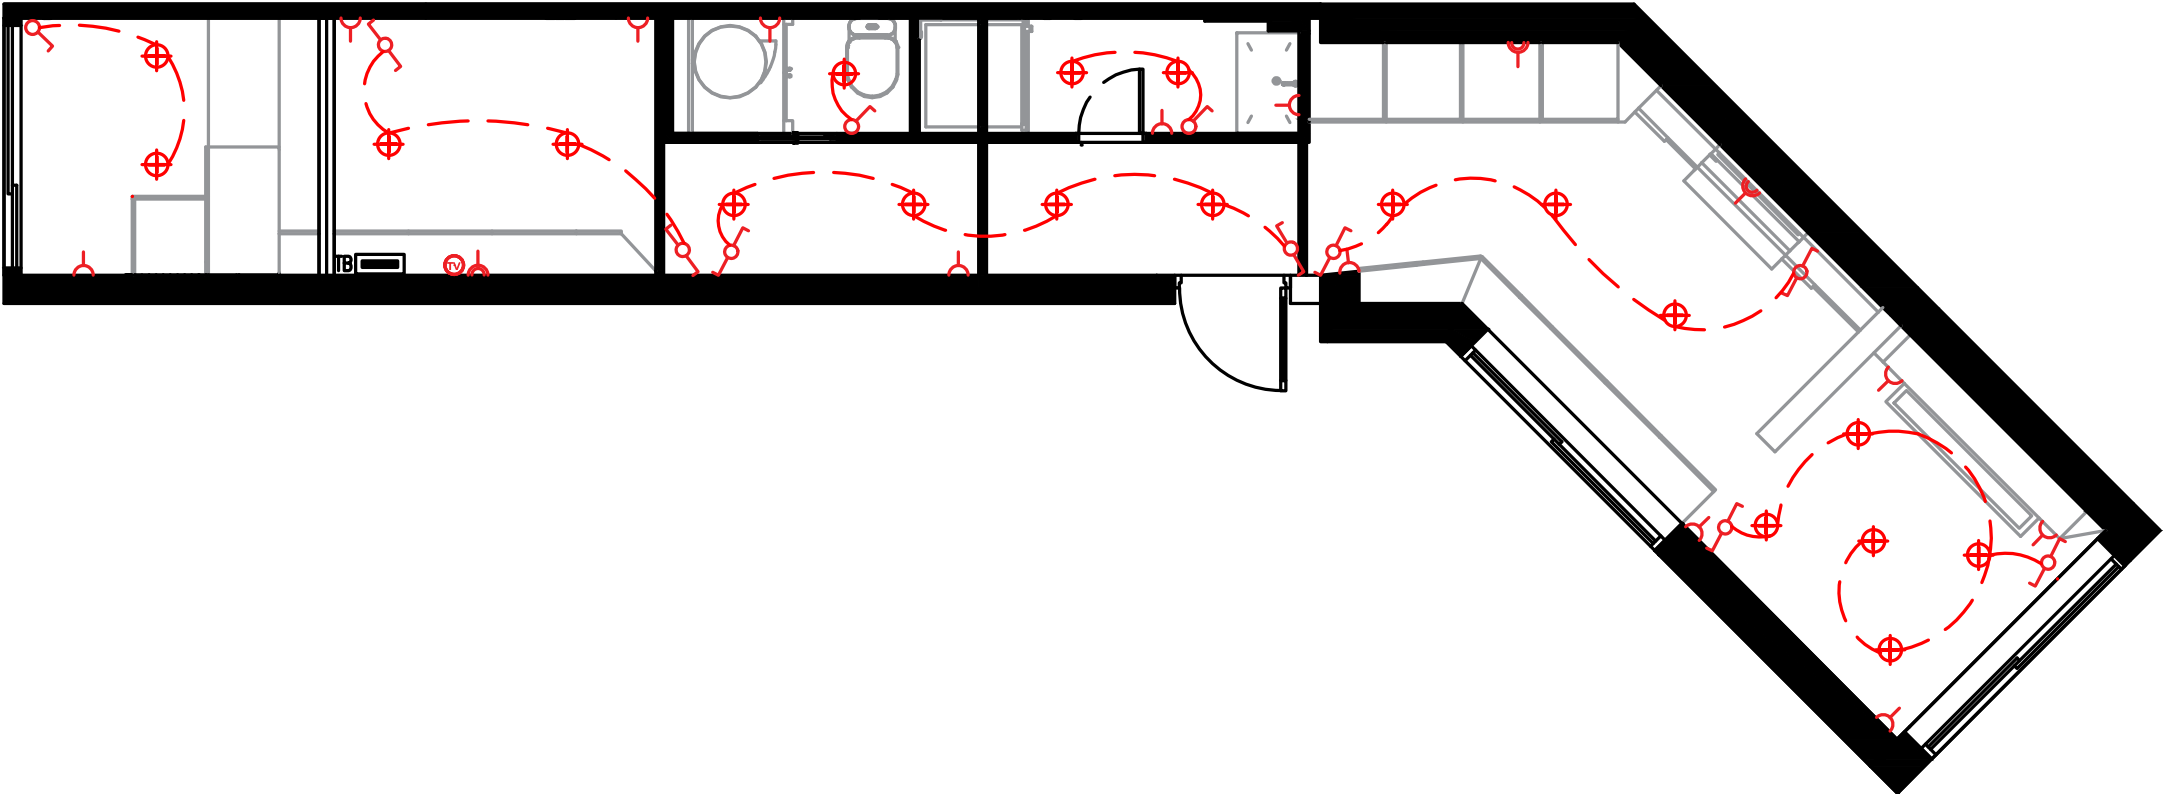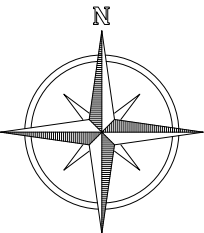

- Interrupteur va-et-viens
- Interrupteur
- Prise 16A
- Double prise 16A
- Prise TV
- Spot encastré



TB Tableau électrique

0 1

|                                                                |                      |                                              |  |                                                                                                |                              |
|----------------------------------------------------------------|----------------------|----------------------------------------------|--|------------------------------------------------------------------------------------------------|------------------------------|
| <b>Ouvrage</b><br>Tiny House<br>6 av Eugène Godin, 77000 Melun |                      | <b>Maitre d’ouvrage</b><br>Yacine Hadj Hamou |  | <b>Maitre d’oeuvre</b><br>Marec Alon / Distrophe Alan<br>12 rue Anatole France ,92000 Nanterre |                              |
| <b>Titre</b><br>Plan électrique                                | <b>Echelle</b><br>A3 | <b>Format</b><br>1/100                       |  | <b>Date</b><br>15/06/2026                                                                      | <b>Etat du projet</b><br>APS |





Plan d'arrivée d'eau

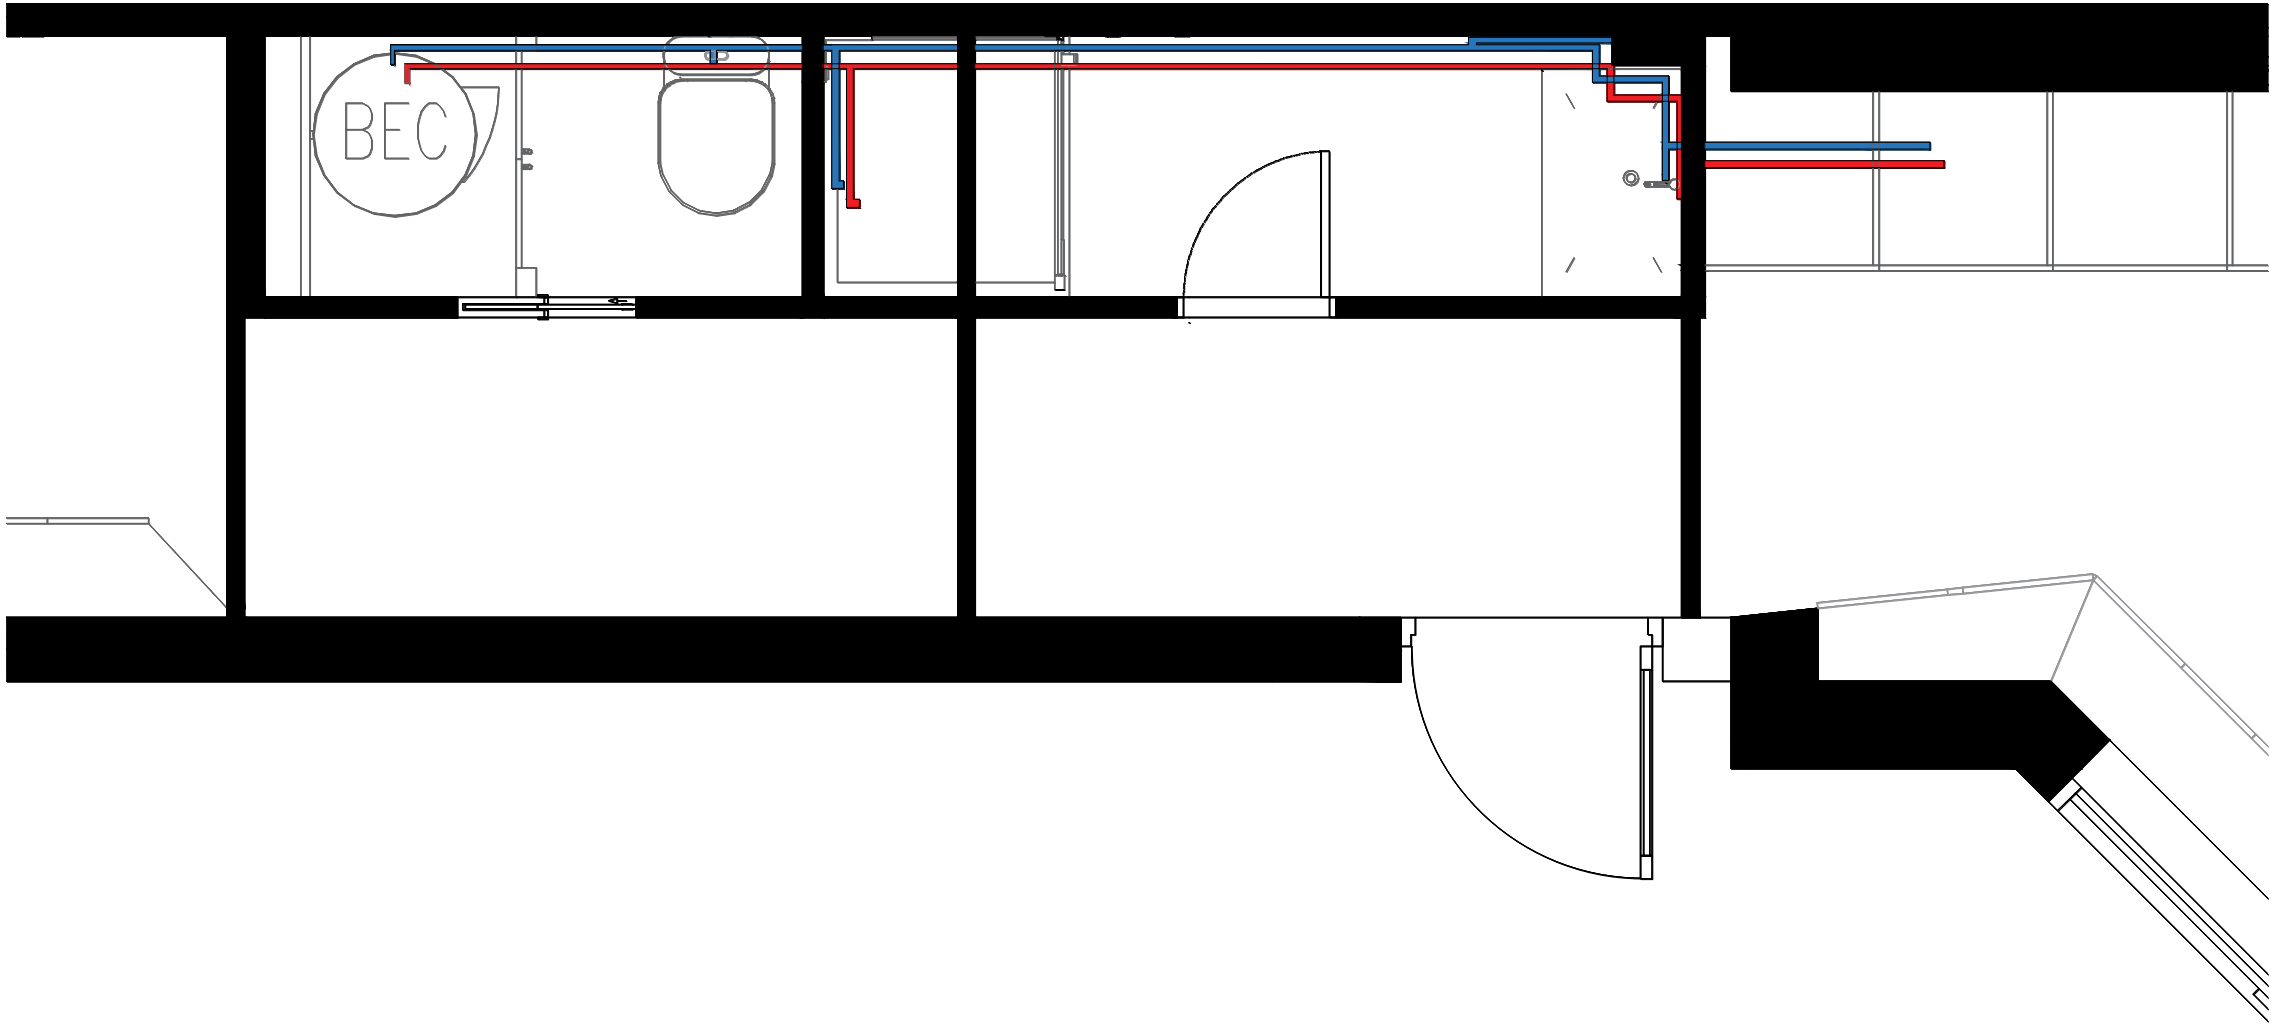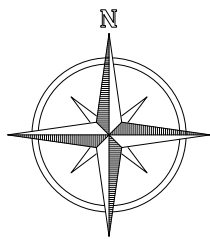

0 1

|                                                                |                                                                                       |                                              |                        |                                                                                                |                              |
|----------------------------------------------------------------|---------------------------------------------------------------------------------------|----------------------------------------------|------------------------|------------------------------------------------------------------------------------------------|------------------------------|
| <b>Ouvrage</b><br>Tiny House<br>6 av Eugène Godin, 77000 Melun |                                                                                       | <b>Maitre d'ouvrage</b><br>Yacine Hadj Hamou |                        | <b>Maitre d'oeuvre</b><br>Marec Alon / Distrophe Alan<br>12 rue Anatole France ,92000 Nanterre |                              |
| <b>Titre</b><br>Plan électrique                                | <b>Légende</b><br><div><div></div> Eau froide</div> <div><div></div> Eau chaude</div> | <b>Echelle</b><br>A3                         | <b>Format</b><br>1/100 | <b>Date</b><br>15/06/2026                                                                      | <b>Etat du projet</b><br>APS |

Plan d'évacuation

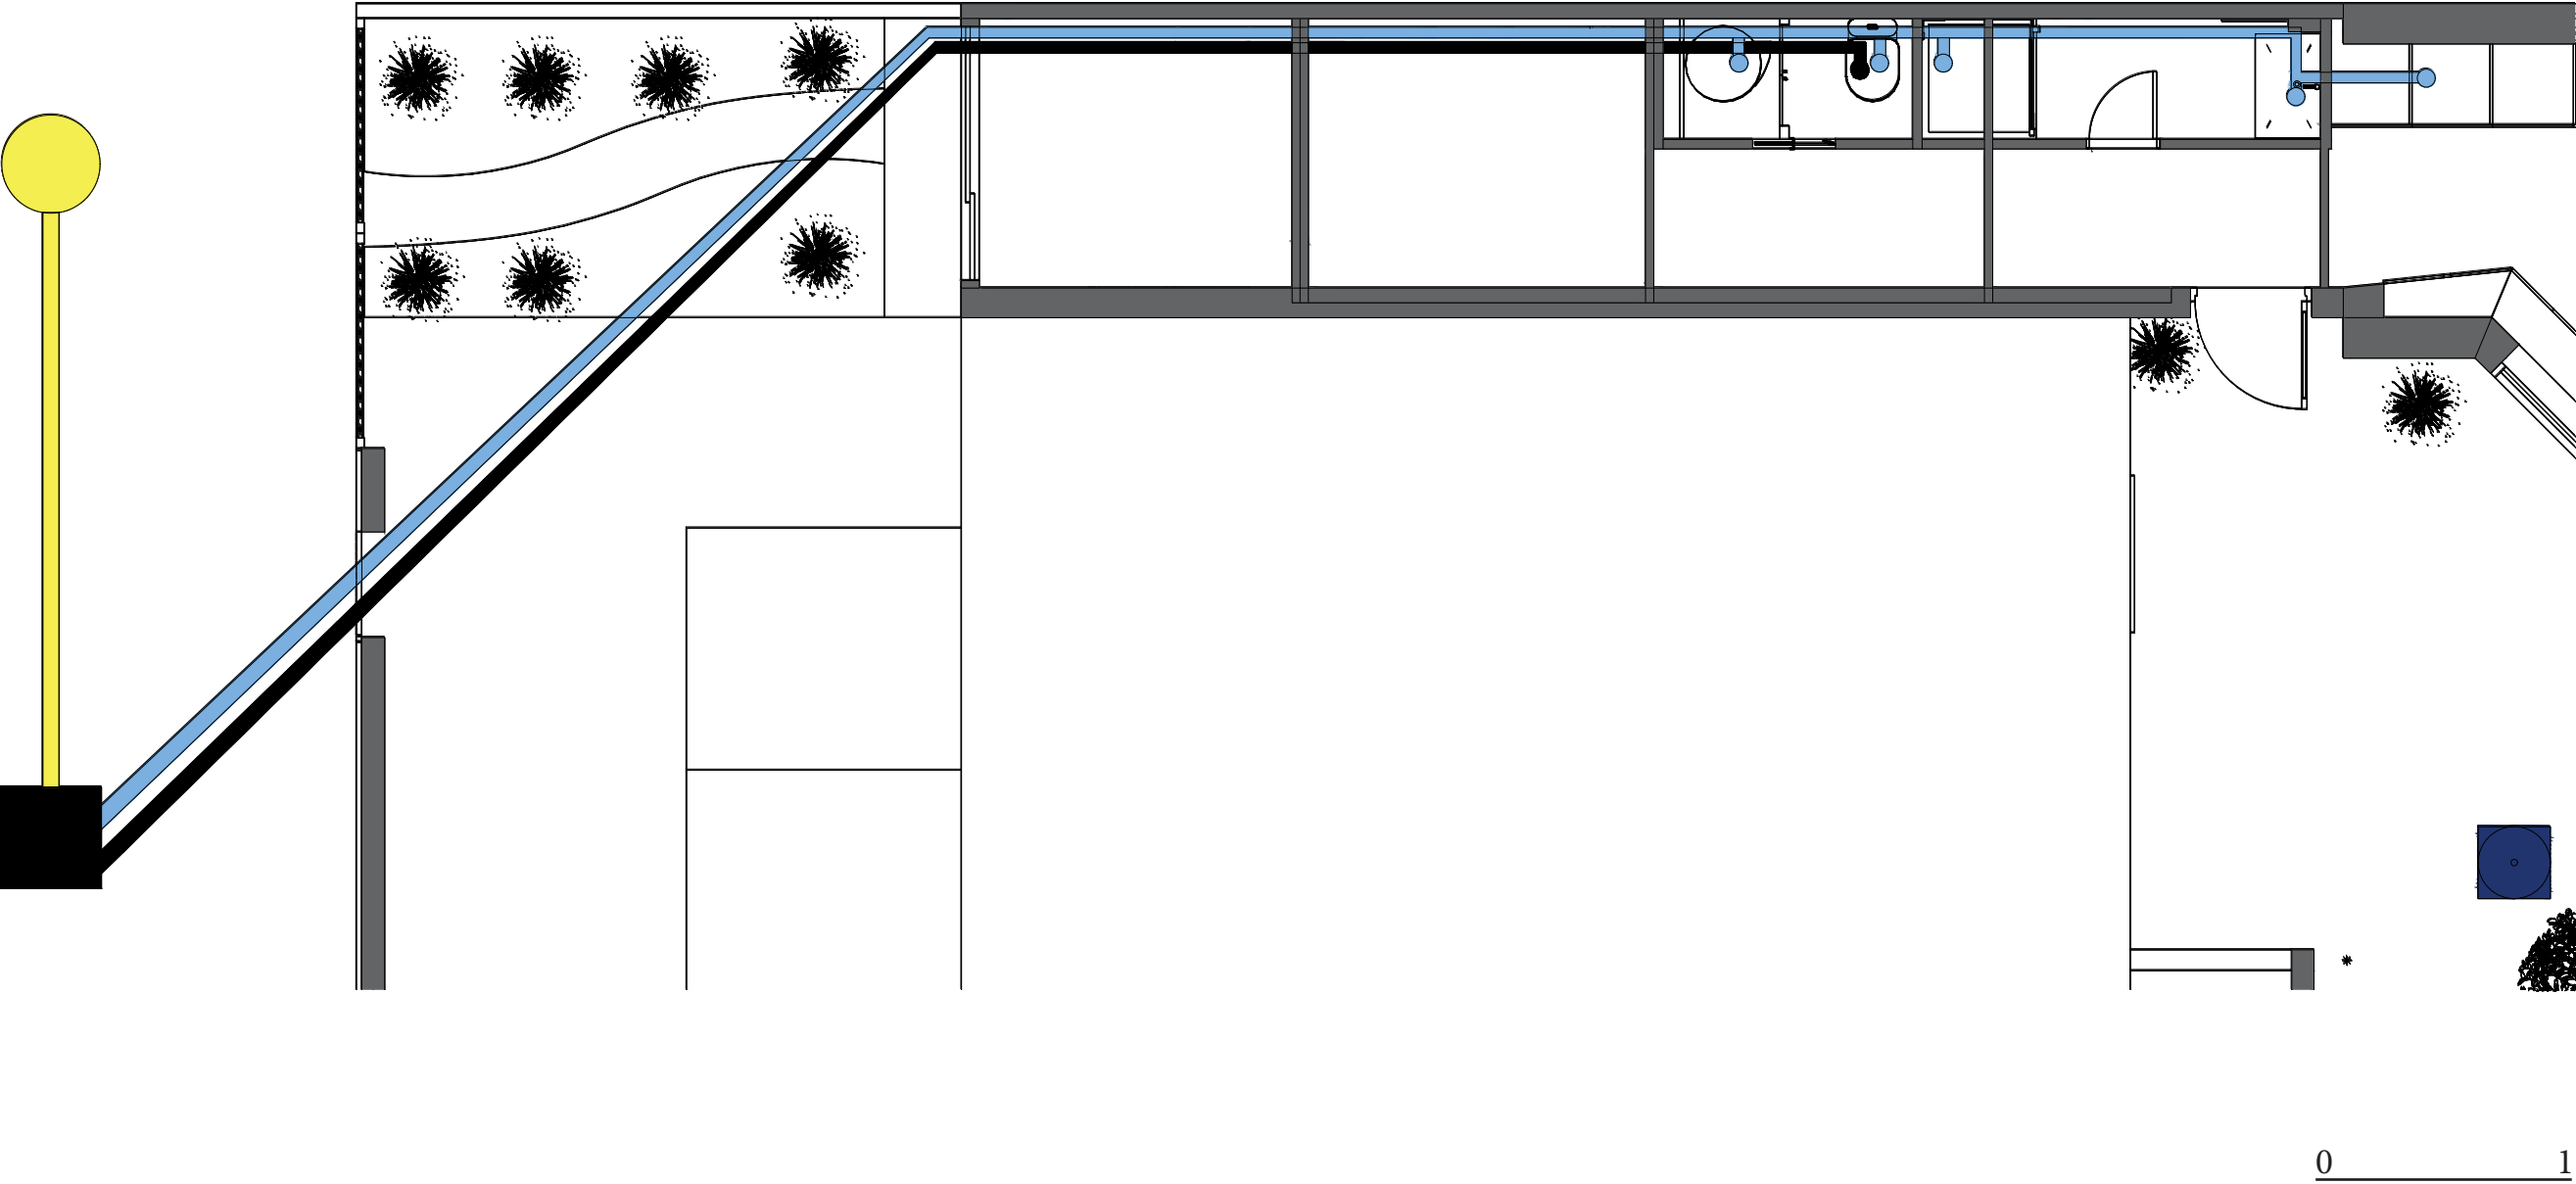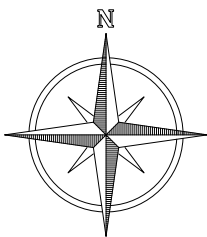

|                                                                |   |                                              |                        |                                                                                                |                              |
|----------------------------------------------------------------|---|----------------------------------------------|------------------------|------------------------------------------------------------------------------------------------|------------------------------|
| <b>Ouvrage</b><br>Tiny House<br>6 av Eugène Godin, 77000 Melun |   | <b>Maitre d'ouvrage</b><br>Yacine Hadj Hamou |                        | <b>Maitre d'oeuvre</b><br>Marec Alon / Distrophe Alan<br>12 rue Anatole France ,92000 Nanterre |                              |
| <b>Titre</b><br>Plan électrique                                | <b>Légende</b><br><div><div></div> Eau grise</div> <div><div></div> Eau noire</div> <div><div></div> Egout</div> <div><div></div> Collecteur</div> <div><div></div> EP</div> | <b>Echelle</b><br>A3                         | <b>Format</b><br>1/100 | <b>Date</b><br>15/06/2026                                                                      | <b>Etat du projet</b><br>APS |

# DQE

## 1. Fondations sur pieux + plancher

| Poste                         | Qté/Surface | Fourniture HT (€) | MO HT (€) | Total HT (€) |
|-------------------------------|-------------|-------------------|-----------|--------------|
| Pieux vissés galvanisés       | 12 u        | 2 400             | 1 200     | 3 600        |
| Poteaux hydrofuges 150x150    | 12 u        | 600               | 250       | 850          |
| Longrines et assemblages      | Forfait     | 900               | 600       | 1 500        |
| Hérisson 15 cm                | 22 m²       | 500               | 400       | 900          |
| Film anti-remontée d'humidité | 22 m²       | 80                | 70        | 150          |
| Ossature plancher 145x45      | 22 m²       | 900               | 700       | 1 600        |
| Isolation 145 mm              | 22 m²       | 500               | 250       | 750          |
| Pare-vapeur                   | 22 m²       | 90                | 120       | 210          |
| OSB 18 mm                     | 22 m²       | 350               | 250       | 600          |
| Parquet effet bois            | 22 m²       | 550               | 500       | 1 050        |
| Sous-total                    |             |                   |           | 11 210       |
| Majoration pertes 15 %        |             |                   |           | 1 682        |
| Total lot avec pertes         |             |                   |           | 12 892       |

## 2. Murs ossature bois 22 cm

| Poste                    | Qté/Surface | Fourniture HT (€) | MO HT (€) | Total HT (€) |
|--------------------------|-------------|-------------------|-----------|--------------|
| Ossature bois 145x45     | 48 m²       | 1 450             | 1 200     | 2 650        |
| Isolation 145 mm         | 48 m²       | 1 050             | 500       | 1 550        |
| OSB contreventement      | 48 m²       | 650               | 450       | 1 100        |
| Pare-pluie               | 48 m²       | 180               | 120       | 300          |
| Pare-vapeur              | 48 m²       | 170               | 150       | 320          |
| Bardage tasseaux douglas | 48 m²       | 2 300             | 2 100     | 4 400        |
| Peinture intérieure      | 48 m²       | 300               | 600       | 900          |
| Sous-total               |             |                   |           | 11 220       |
| Majoration pertes 15 %   |             |                   |           | 1 683        |
| Total lot avec pertes    |             |                   |           | 12 903       |

## 3. Toiture 3 pans

| Poste                  | Qté/Surface | Fourniture HT (€) | MO HT (€) | Total HT (€) |
|------------------------|-------------|-------------------|-----------|--------------|
| Charpente 145x45       | 32 m²       | 1 000             | 900       | 1 900        |
| Isolation 145 mm       | 32 m²       | 700               | 300       | 1 000        |
| OSB toiture            | 32 m²       | 450               | 250       | 700          |
| Pare-pluie             | 32 m²       | 120               | 100       | 220          |
| Pare-vapeur            | 32 m²       | 120               | 100       | 220          |
| Liteaux/tasseaux       | 32 m²       | 250               | 180       | 430          |
| Bac acier              | 32 m²       | 1 250             | 950       | 2 200        |
| Gouttières             | Forfait     | 300               | 250       | 550          |
| Corniches métalliques  | Forfait     | 350               | 250       | 600          |
| Sous-total             |             |                   |           | 7 820        |
| Majoration pertes 15 % |             |                   |           | 1 173        |
| Total lot avec pertes  |             |                   |           | 8 993        |

|                      |             |
|----------------------|-------------|
| Montant travaux HT   | 30 250.00 € |
| Pertes / chutes 15 % | 4 537.50 €  |
| TOTAL HT             | 34 787.50 € |

| DQE                                          | Désignation   | Unité | Quantiter     | prix U ht    | total ht    |
|----------------------------------------------|---|-------|---------------|--------------|-------------|
| LOT 1 - DEMOLITION/PREPARATION               | Démolition du mur du garage existant donnant sur le jardin   |       | 10-15% pertes | approximatif | 506,00 €    |
| LOT 2 - CHARPENTE                            | Tout les éléments de sturcture de la Tiny House   |       | 10-15% pertes | approximatif | 34 787,50 € |
| LOT 3 - ELECTRICITER                         | Travaux d'électricité comprenant la dépose des équipements existants, la fourniture et la pose d'un tableau électrique neuf, des appareillages (interrupteurs et prises de courant) ainsi que des points d'éclairage, avec raccordement et mise en service de l'ensemble de l'installation. |       | 10-15% pertes | approximatif | 2 508,00 €  |
| LOT 4 - PLOMBERIE                            | Travaux de plomberie et d'installation sanitaire comprenant la fourniture et la pose du lavabo, de l'évier, de la douche, du WC, du chauffe-eau ainsi que tous les raccordements, réglages et mises en service nécessaires.                                                                 |       | 10-15% pertes | approximatif | 2 145,00 €  |
| LOT 5 - SOL SOUPLE - PARQUET                 | Travaux de revêtement de sol en parquet comprenant la fourniture et la pose du parquet, les découpes, les accessoires de finition et toutes les sujétions nécessaires à la bonne mise en œuvre de l'ouvrage.                                                                                |       | 10-15% pertes | approximatif | 3 300,00 €  |
| LOT 6 - SOL DURE - CARRELAGE                 | Travaux de revêtement de sol en carrelage comprenant la fourniture et la pose du carrelage, la préparation du support, les découpes, les joints et les finitions nécessaires à la parfaite exécution de l'ouvrage.                                                                          |       | 10-15% pertes | approximatif | 368,50 €    |
| LOT 7 - PEINTURE REVETEMENT MURAL int.       | Travaux de peinture comprenant la préparation des supports, les reprises éventuelles, l'application d'un enduit de lissage ainsi que la fourniture et l'application de deux couches de peinture mate sur l'ensemble des surfaces concernées.                                                |       | 10-15% pertes | approximatif | 2 365,00 €  |
| LOT 8 - MENUISERIE int.                      | Travaux de menuiserie intérieure comprenant la fourniture et la pose des portes, portes coulissantes, portes de placard et autres ouvrages de menuiserie, avec quincaillerie, réglages et finitions nécessaires à leur parfaite mise en œuvre.                                              |       | 10-15% pertes | approximatif | 5 445,00 €  |
| LOT 10 - MENUISERIE mobilier sur mesure int. | Fourniture, fabrication et pose de mobilier sur mesure en panneaux décor bois, comprenant l'ensemble des découpes, assemblages, quincailleries, finitions et ajustements nécessaires à la parfaite exécution des ouvrages.                                                                  |       | 10-15% pertes | approximatif | 11 000,00 € |
| TOTAL HT                                     |   |       | 10-15% pertes | approximatif | 62 425,00 € |

## Rendu photo réaliste





## Rendu photo réaliste



# RENDU PHOTO REALISTES

SKETCHUP + D5 + IA



Vue interieur depuis l'existant vers l'extention



# RENDU PHOTO REALISTES

SKETCHUP + D5 + IA



Vue exterieur de la facade de la tiny house



**MERCI !**